

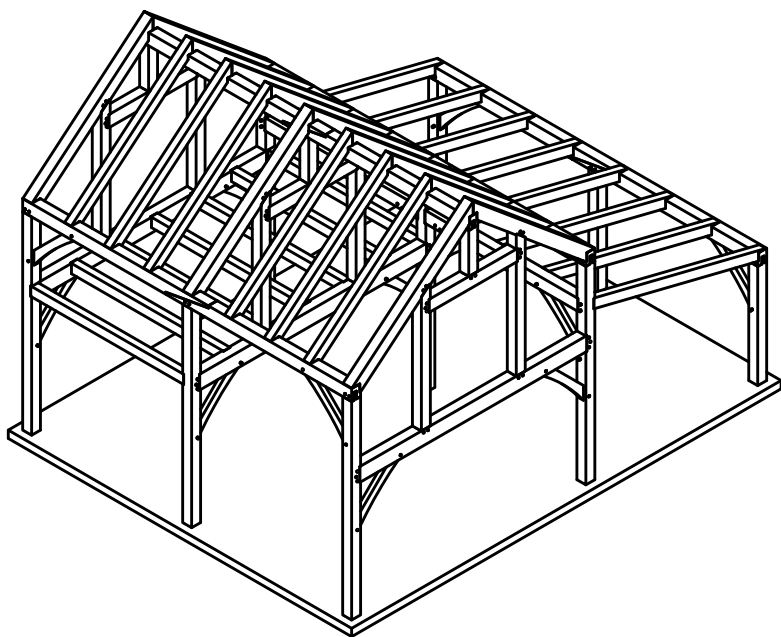


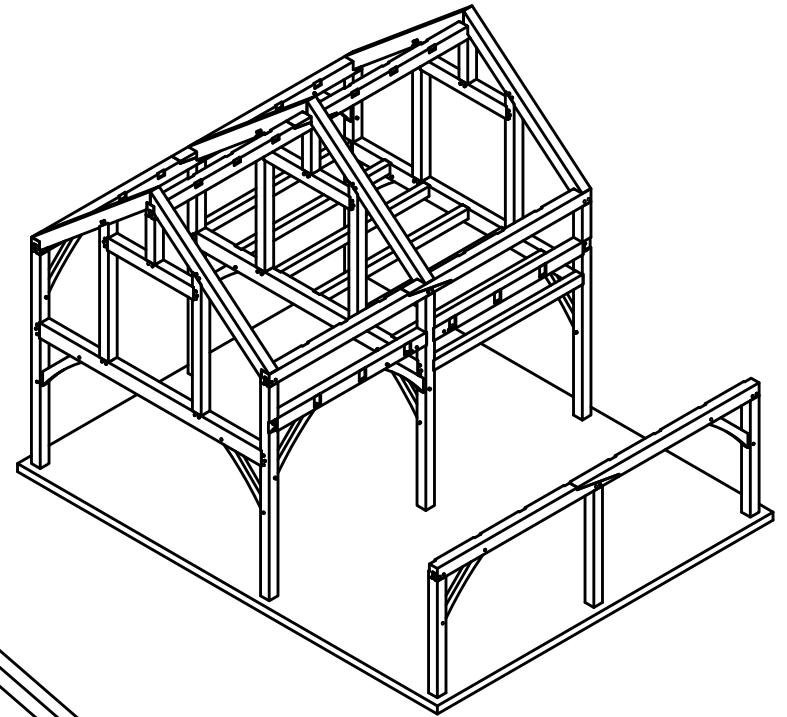



30x24 Timber Frame Cabin

Index of Drawings

- | | |
|--------------------------------------|-----------------------------------|
| 1. CS-1 - COVER SHEET/3D PERSPECTIVE | 23. PD-7 - GRID LINE 1C POST |
| 2. CS-2 - 3D PERSPECTIVES | 22. PD-8 - GRID LINE 2C POST |
| 3. CS-3 - 3D PERSPECTIVES | 23. PD-9 - GRID LINE 3C POST |
| 4. CS-4 - 3D PERSPECTIVES | 24. PD-10 - GRID LINE 1 GIRT |
| 5. CS-5 - 3D PERSPECTIVE | 25. PD-11 - GRID LINE 2 GIRT |
| 6. CS-6 - TIMBER/ SCHEDULE | 26. PD-12 - GRID LINE 3 GIRT |
| 7. TF-1 - POST PLAN | 27. PD-13 - QUEEN POST |
| 8. TF-2 - LOFT PLAN | 28. PD-14 - KING POST |
| 9. TF-3 - ROOF PLAN | 29. PD-15 - TIE BEAM |
| 10. TF-4 - FRONT ELEVATION | 30. PD-16 - SHED HEADER/PLATE 1-2 |
| 11. TF-5 - RIGHT SIDE ELEVATION | 31. PD-17 - SHED HEADER/PLATE 2-3 |
| 12. TF-6 - REAR ELEVATION | 32. PD-18 - GRID LINE A/1-2 PLATE |
| 13. TF-7 - LEFT SIDE ELEVATION | 33. PD-19 - GRID LINE A/2-3 PLATE |
| 14. TF-8 - SECTION VIEW | 34. PD-20 - GRID LINE B/1-2 PLATE |
| 15. TF-9 - SECTION VIEW | 35. PD-21 - GRID LINE B/2-3 PLATE |
| 16. TF-10 - SECTION VIEW | 35. PD-22 - GRID LINE C/1-2 PLATE |
| 17. PD-1 - GRID LINE 1A POST | 35. PD-23 - GRID LINE C/2-3 PLATE |
| 18. PD-2 - GRID LINE 2A POST | 35. PD-24 - GRID LINE 1-2 RIDGE |
| 19. PD-3 - GRID LINE 3A POST | 35. PD-25 - GRID LINE 2-3 RIDGE |
| 20. PD-4 - GRID LINE 1B POST | 36. PD-26 - KNEE BRACE |
| 21. PD-5 - GRID LINE 2B POST | 37. PD-27 - JOIST |
| 22. PD-6 - GRID LINE 3B POST | 38. PD-28 - PRINCIPAL RAFTER |
| | 39. PD-29 - COMMON RAFTER |
| | 40. PD-30 - SHED RAFTER |

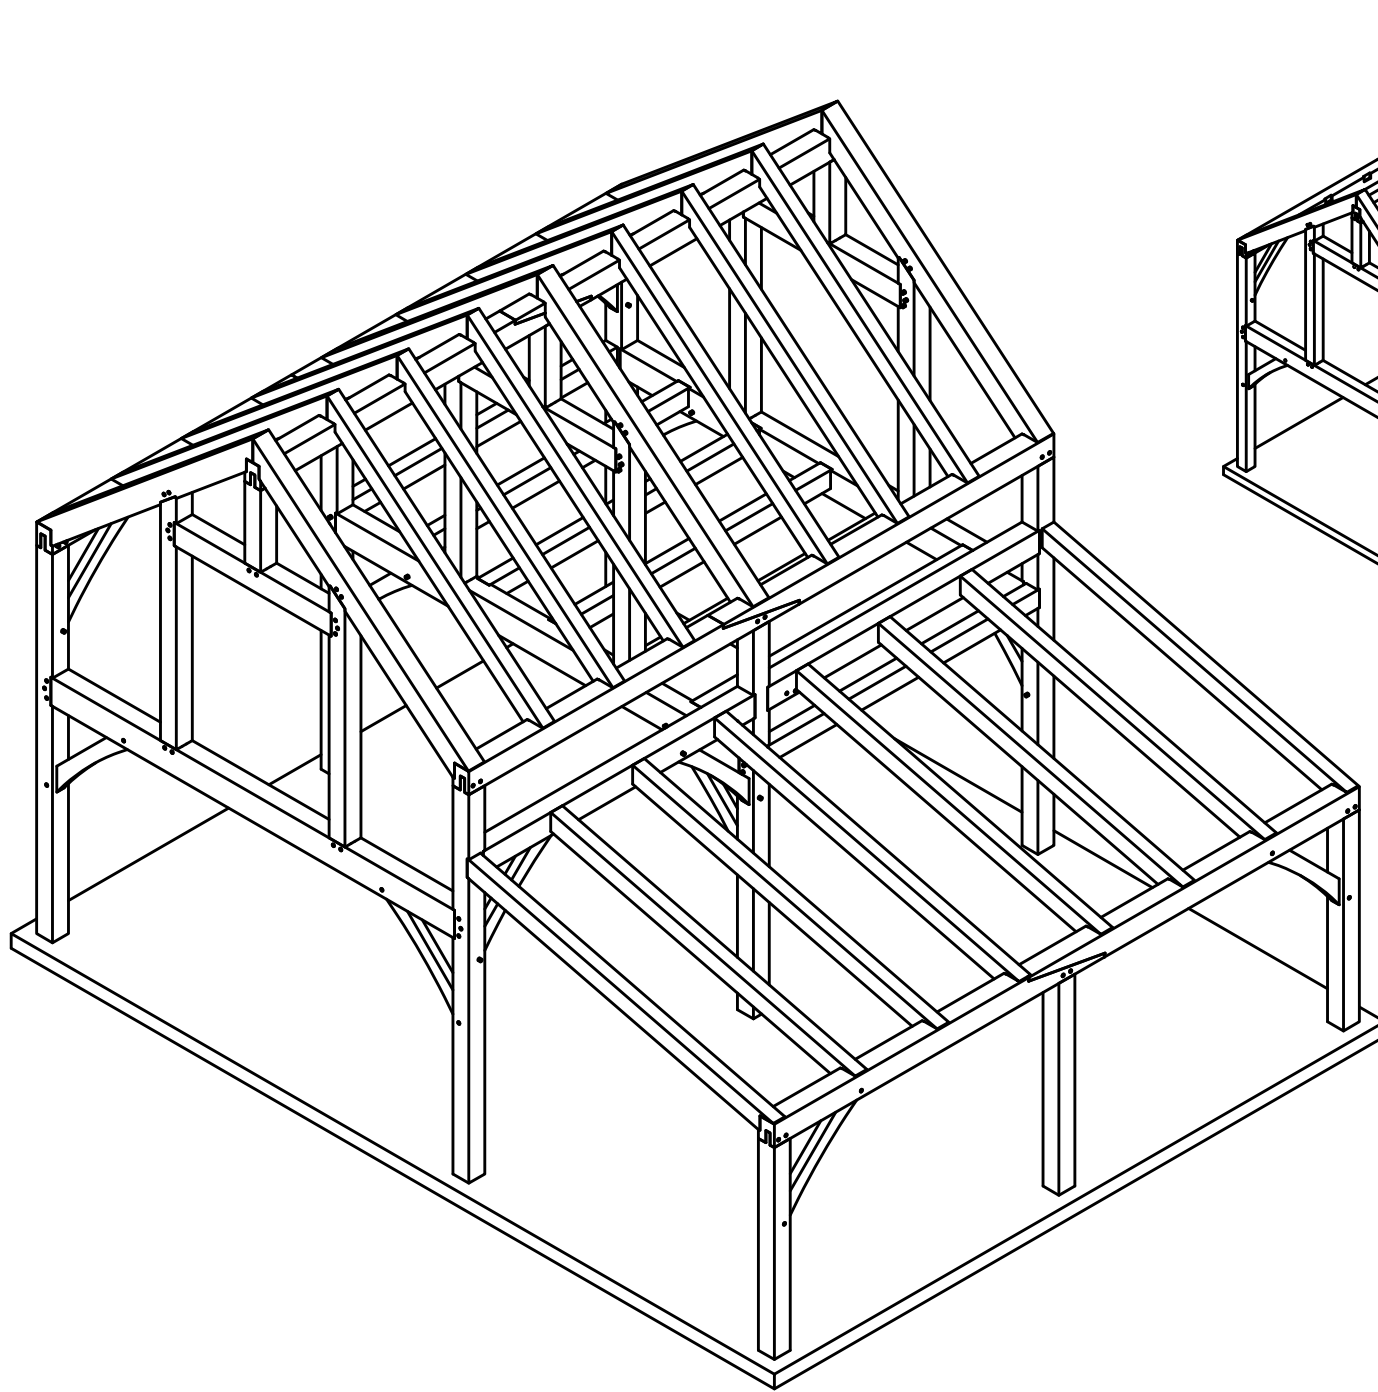

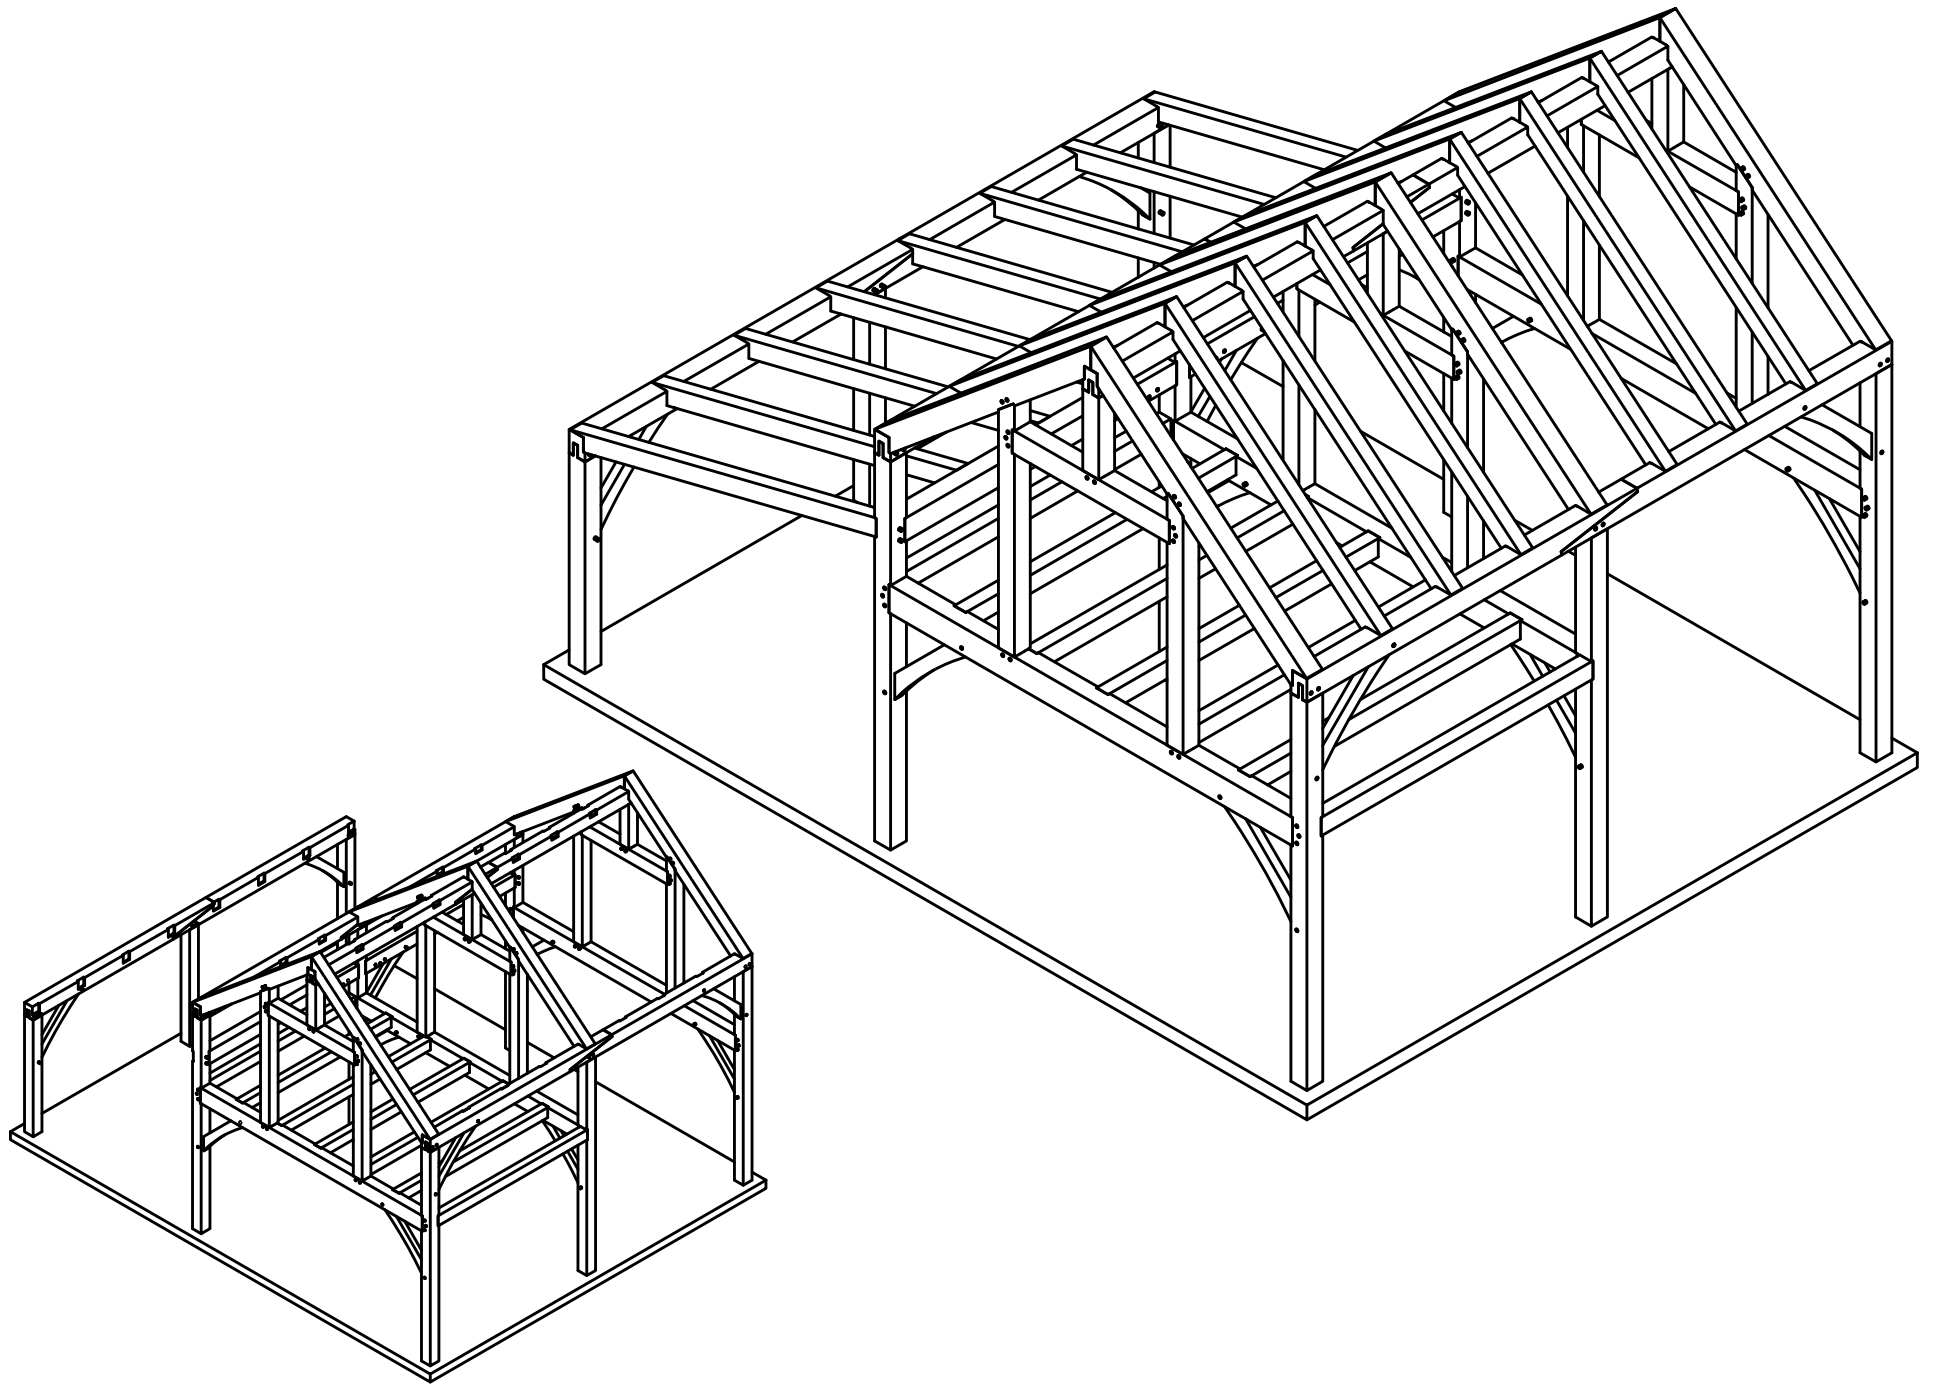

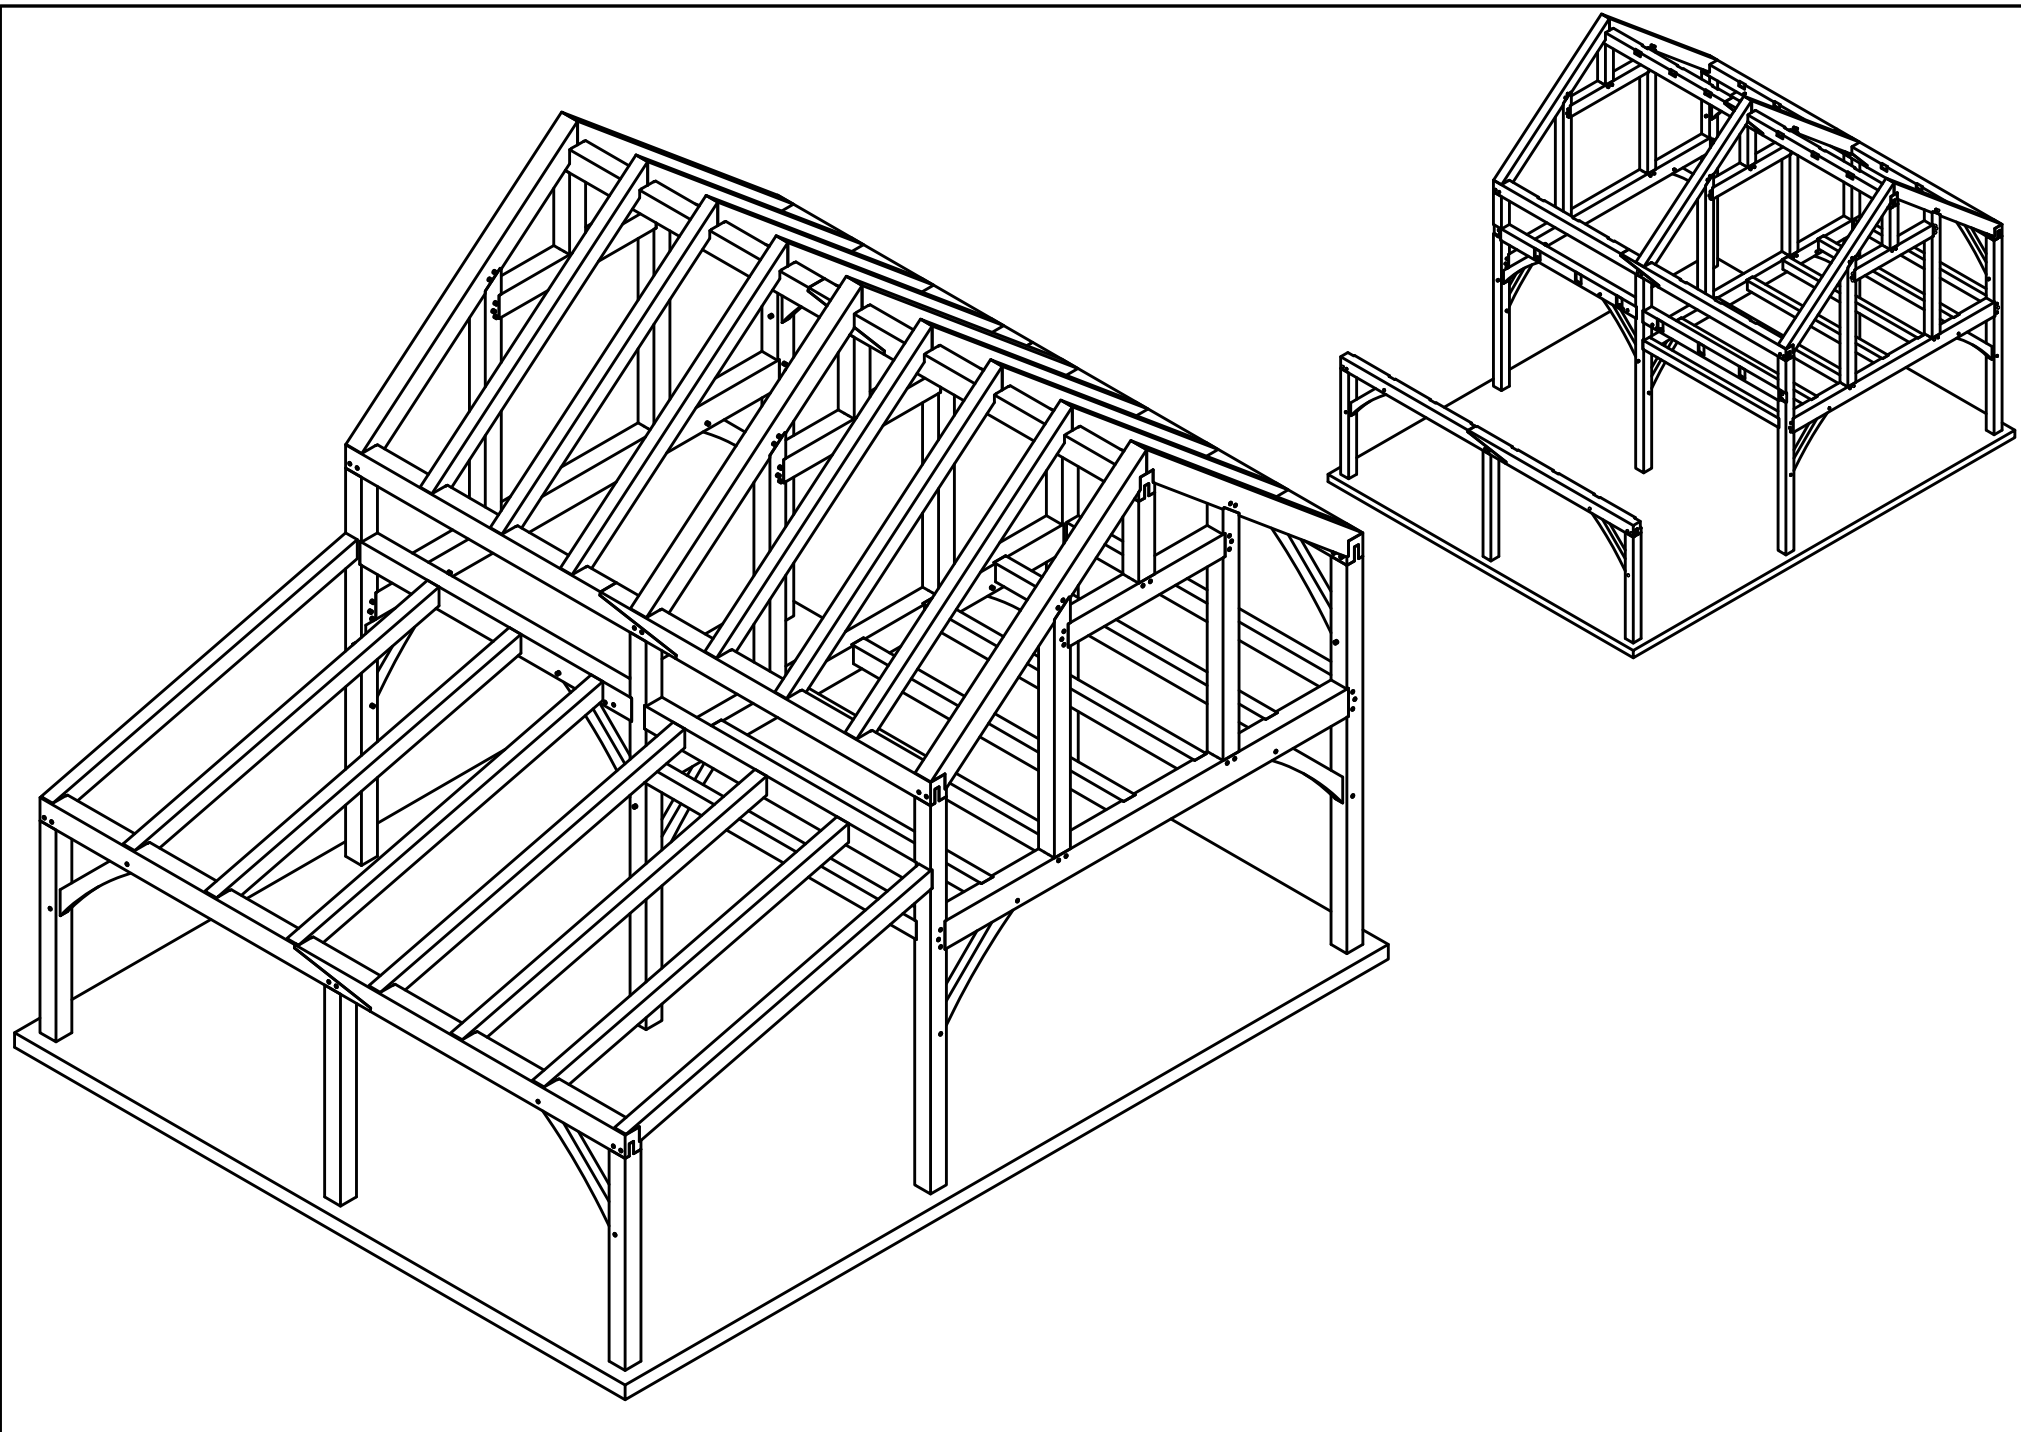

GENERAL NOTES:

1. THE CONTRACTOR AND EACH SUBCONTRACTOR SHALL BE REQUIRED TO CHECK AND VERIFY THAT THE PLANS CONFORM WITH ALL REQUIREMENTS AND LOCAL BUILDING CODES, AND MANUFACTURER'S RECOMMENDATIONS PRIOR TO SIGNING CONTRACT OR BEGINNING WORK.
2. THE DRAWINGS ARE DIAGRAMMATIC, INTENDED TO OUTLINE GENERAL REQUIREMENTS ONLY, AND NOT INTENDED TO BE COMPLETE IN ALL DETAILS. SPECIFIC IMPLEMENTATION OF THE PLANS SHALL BE THE RESPONSIBILITY OF THE CONTRACTOR WHO REPRESENTS HE/SHE HAS THE SKILL AND EXPERT KNOWLEDGE TO EXECUTE THE WORK REQUIRED.
3. THE CONTRACTOR AND EACH SUBCONTRACTOR SHALL VERIFY DIMENSIONS AND DETAILS SHOWN ON THE DRAWINGS BEFORE LAYING OUT OR PROCEEDING WITH WORK AND SHALL BE HELD RESPONSIBLE FOR ANY ERROR RESULTING FROM HIS/HER FAILURE TO EXERCISE SUCH VERIFICATION.
5. TIMBER FRAME HQ ASSUMES NO RESPONSIBILITY FOR ANY CHANGES OR MODIFICATIONS THAT MAY BE MADE TO THE PLANS BY THE OWNER OR THE OWNERS CONTRACTOR OR SUBCONTRACTOR.
6. THESE ARE "DESIGN ONLY" PLANS AND ARE NOT ENGINEERED PLANS. IT IS THE SOLE AND EXCLUSIVE RESPONSIBILITY OF THE OWNER AND THE OWNER'S CONTRACTOR OR SUBCONTRACTOR'S TO DETERMINE IF ENGINEERED PLANS ARE NECESSARY PURSUANT TO LOCAL OR STATE CODE REQUIREMENTS AND WHETHER STATE OR LOCAL BUILDING CODE REQUIREMENTS REQUIRE MODIFICATIONS OF MATERIALS OR STRUCTURAL SPECIFICATIONS ON THESE PLANS. TIMBER FRAME HQ ASSUMES NO RESPONSIBILITY AND DOES NOT WARRANTY THAT THESE PLANS SATISFY THE REQUIREMENTS OF STATE AND/OR LOCAL BUILDING CODES.


PLEASE NOTE:

IN THE TIMBER LIST, WE ADD SOME LENGTH TO ACCOMMODATE TWO THINGS.

1- YOU CAN END UP WITH A ROUGH TIMBER THAT IS TOO SHORT FOR WHAT YOU NEED IN YOUR ORDER.

2- THE EXTRA LENGTH ALLOWS YOU TO MOVE THE FINAL PIECE UP OR DOWN ON THE TIMBER SO THAT YOU DON'T END UP WITH A KNOT OR OTHER DEFECT WHERE THE JOINERY WILL BE. THIS MAKES IT EASIER/MORE ENJOYABLE TO CUT.

FOR CONCRETE TO POST CONNECTION SEE:
<https://timberframehq.com/construction-details/masonryconcrete-to-timber/>

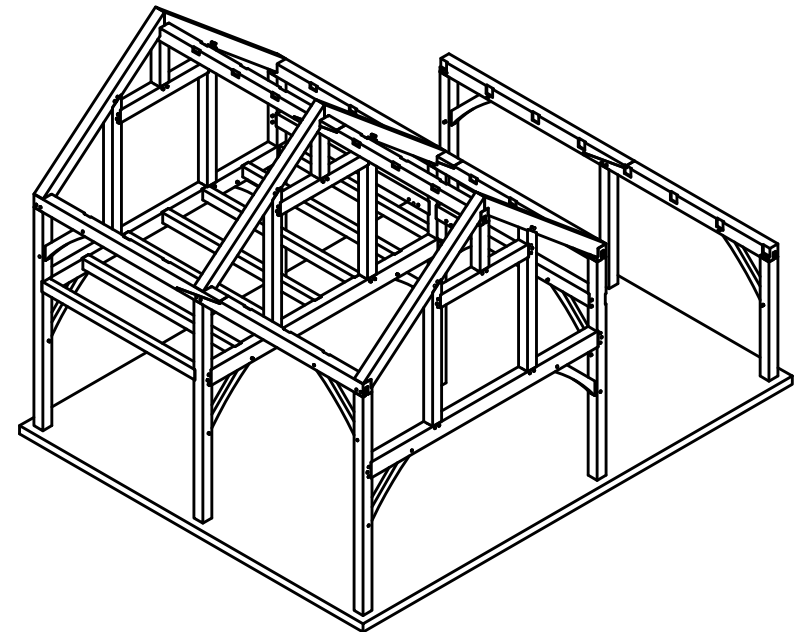



Timber List


Type	Qty.	Act. Width	Act. Height	Act. Length	Nom. Width	Nom. Height	Nom. Length		Board Footage	Total Board Footage	Total Linear Feet
Post	6	7 1/2"	7 1/2"	13'-8 1/4"	8	8	16		85.33	512.00	96
Post	3	7 1/2"	7 1/2"	7'-7 1/2"	8	8	10		53.33	160.00	30
Tie Beam	3	7 1/2"	11 1/2"	16'-8 1/4"	8	12	18		144.00	432.00	54
Queen Post	6	7 1/2"	7 1/2"	9'-2 1/8"	8	8	12		64.00	384.00	72
King Post	3	7 1/2"	7 1/2"	3'-7 3/8"	8	8	4		21.33	64.00	12
Tie Beam	3	7 1/2"	9 1/2"	7'-0"	8	10	8		53.33	160.00	24
Shed Roof Header	2	7 1/2"	9 1/2"	11'-1 1/8"	8	10	14		93.33	186.67	28
Plates/Ridge	8	7 1/2"	9 1/2"	12'-11 7/8"	8	10	14		93.33	746.67	112
Knee Brace	14	3 1/2"	7 1/2"	4'-9 5/8"	4	8	6		16.00	224.00	84
Joist	7	3 1/2"	7 1/2"	10'-8 1/8"	4	8	12		32.00	224.00	84
Principal Rafter	6	7 1/2"	9 1/2"	11'-0 7/16"	8	10	12		80.00	480.00	72
Common Rafter	12	5 1/2"	7 1/2"	11'-0 3/8"	6	8	12		48.00	576.00	144
Common Shed Rafter	8	5 1/2"	7 1/2"	12'-4 5/8"	6	8	14		56.00	448.00	112
Totals	81									3573.33	668


Fastener Schedule


Type	Quantity
Rothoblaas TBS EVO 8mm x 200mm (6") (for Joists)	28
Rothoblaas TBS EVO 8mm x 200mm (for Rafters and Scarf Joints)	58
1"x10" White Oak Pegs	124
1"x8" White Oak Pegs	27
Post Bases - TBD (See URL)	9
Hardwood Spline - 3'-11 1/2" x 6 1/2" x 1 1/2"	1

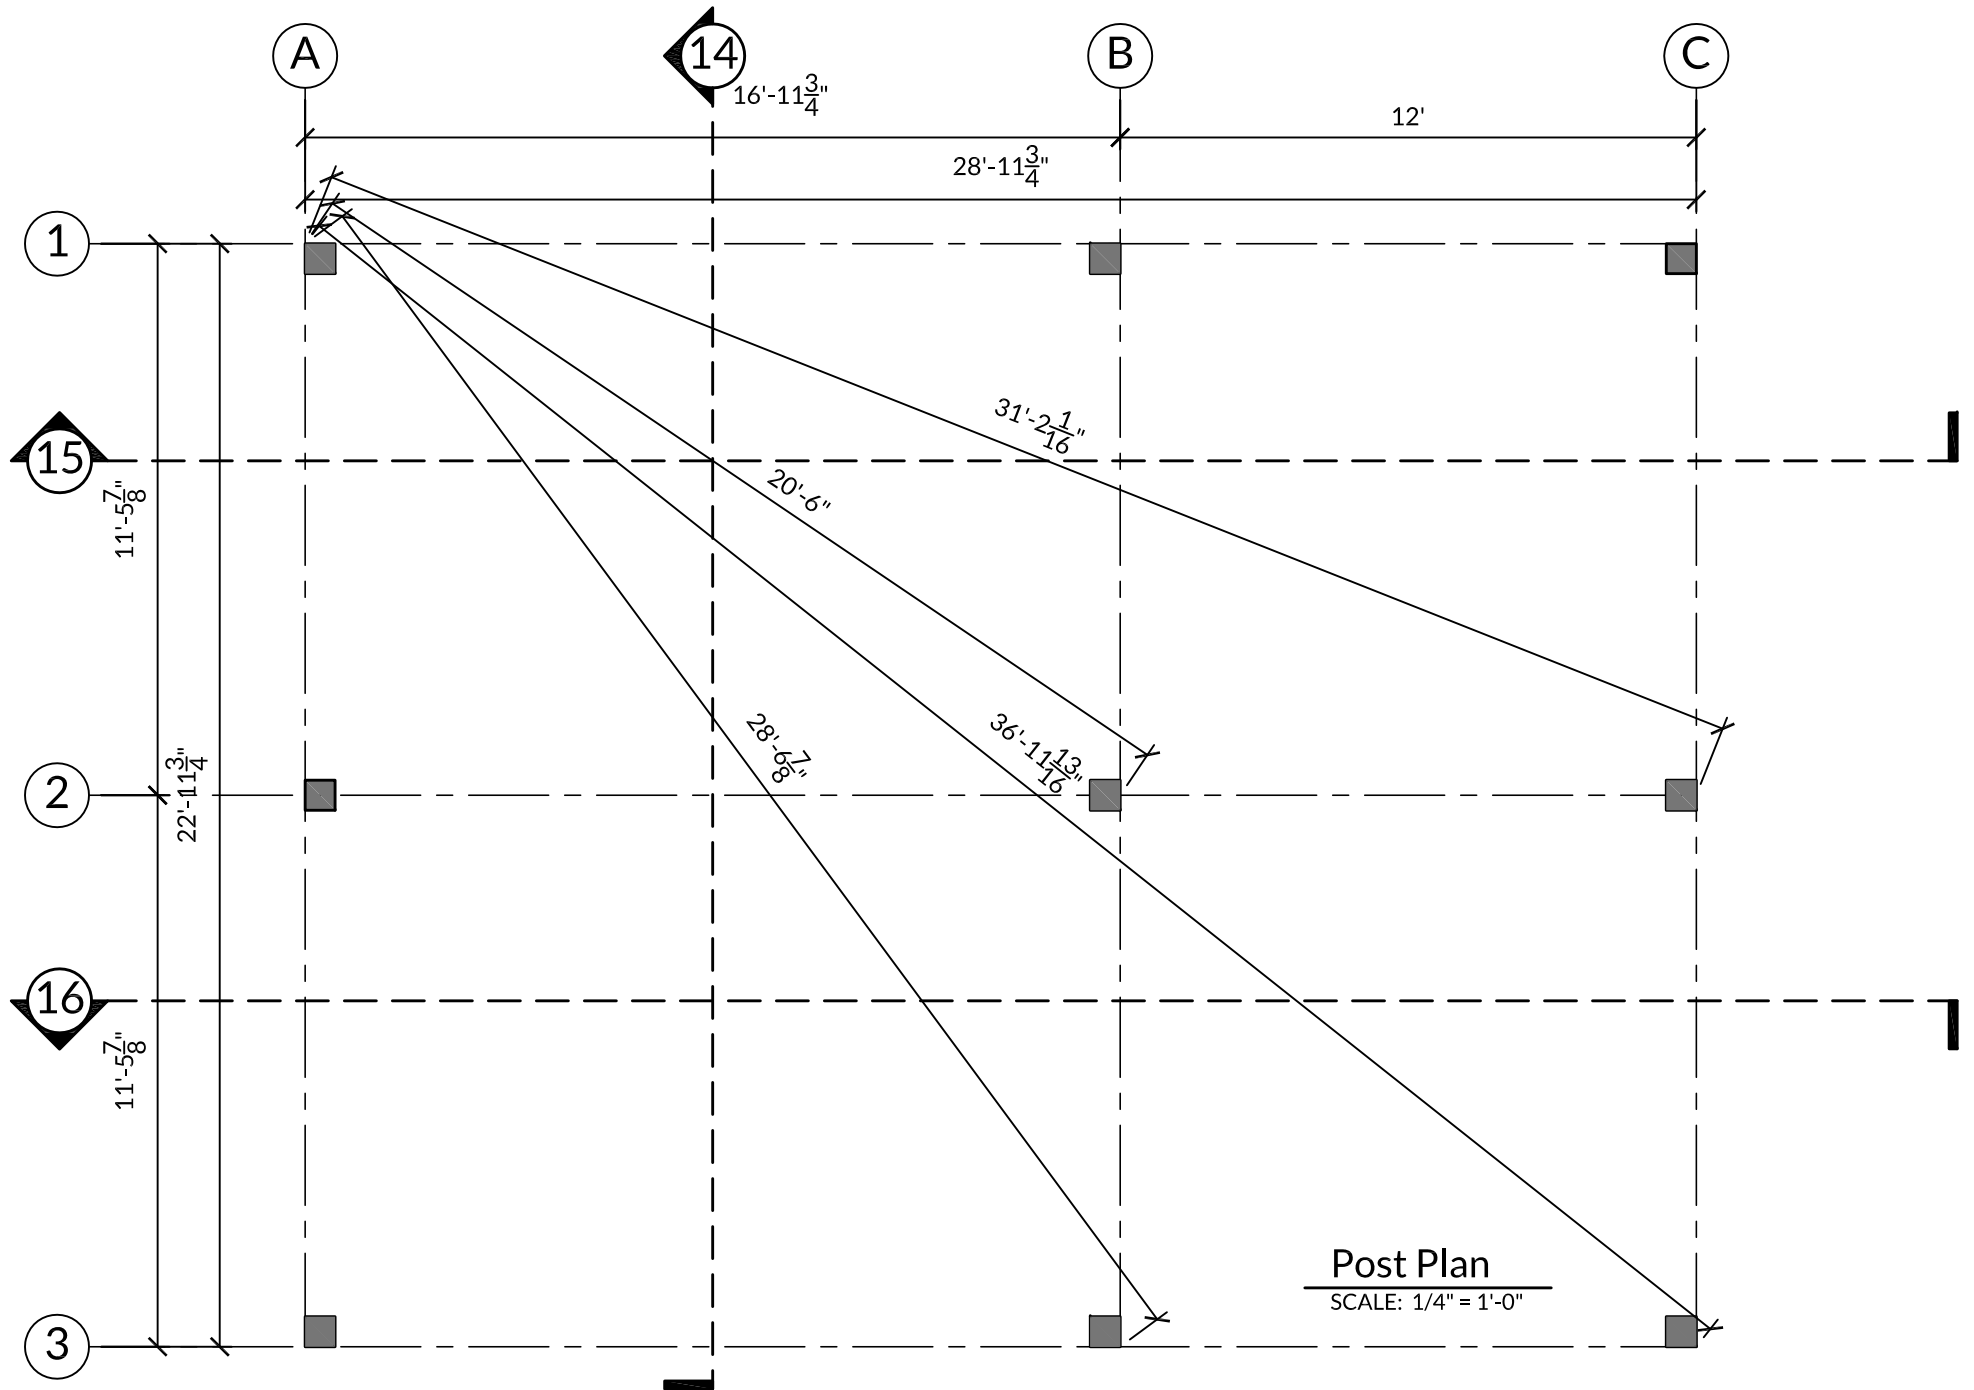

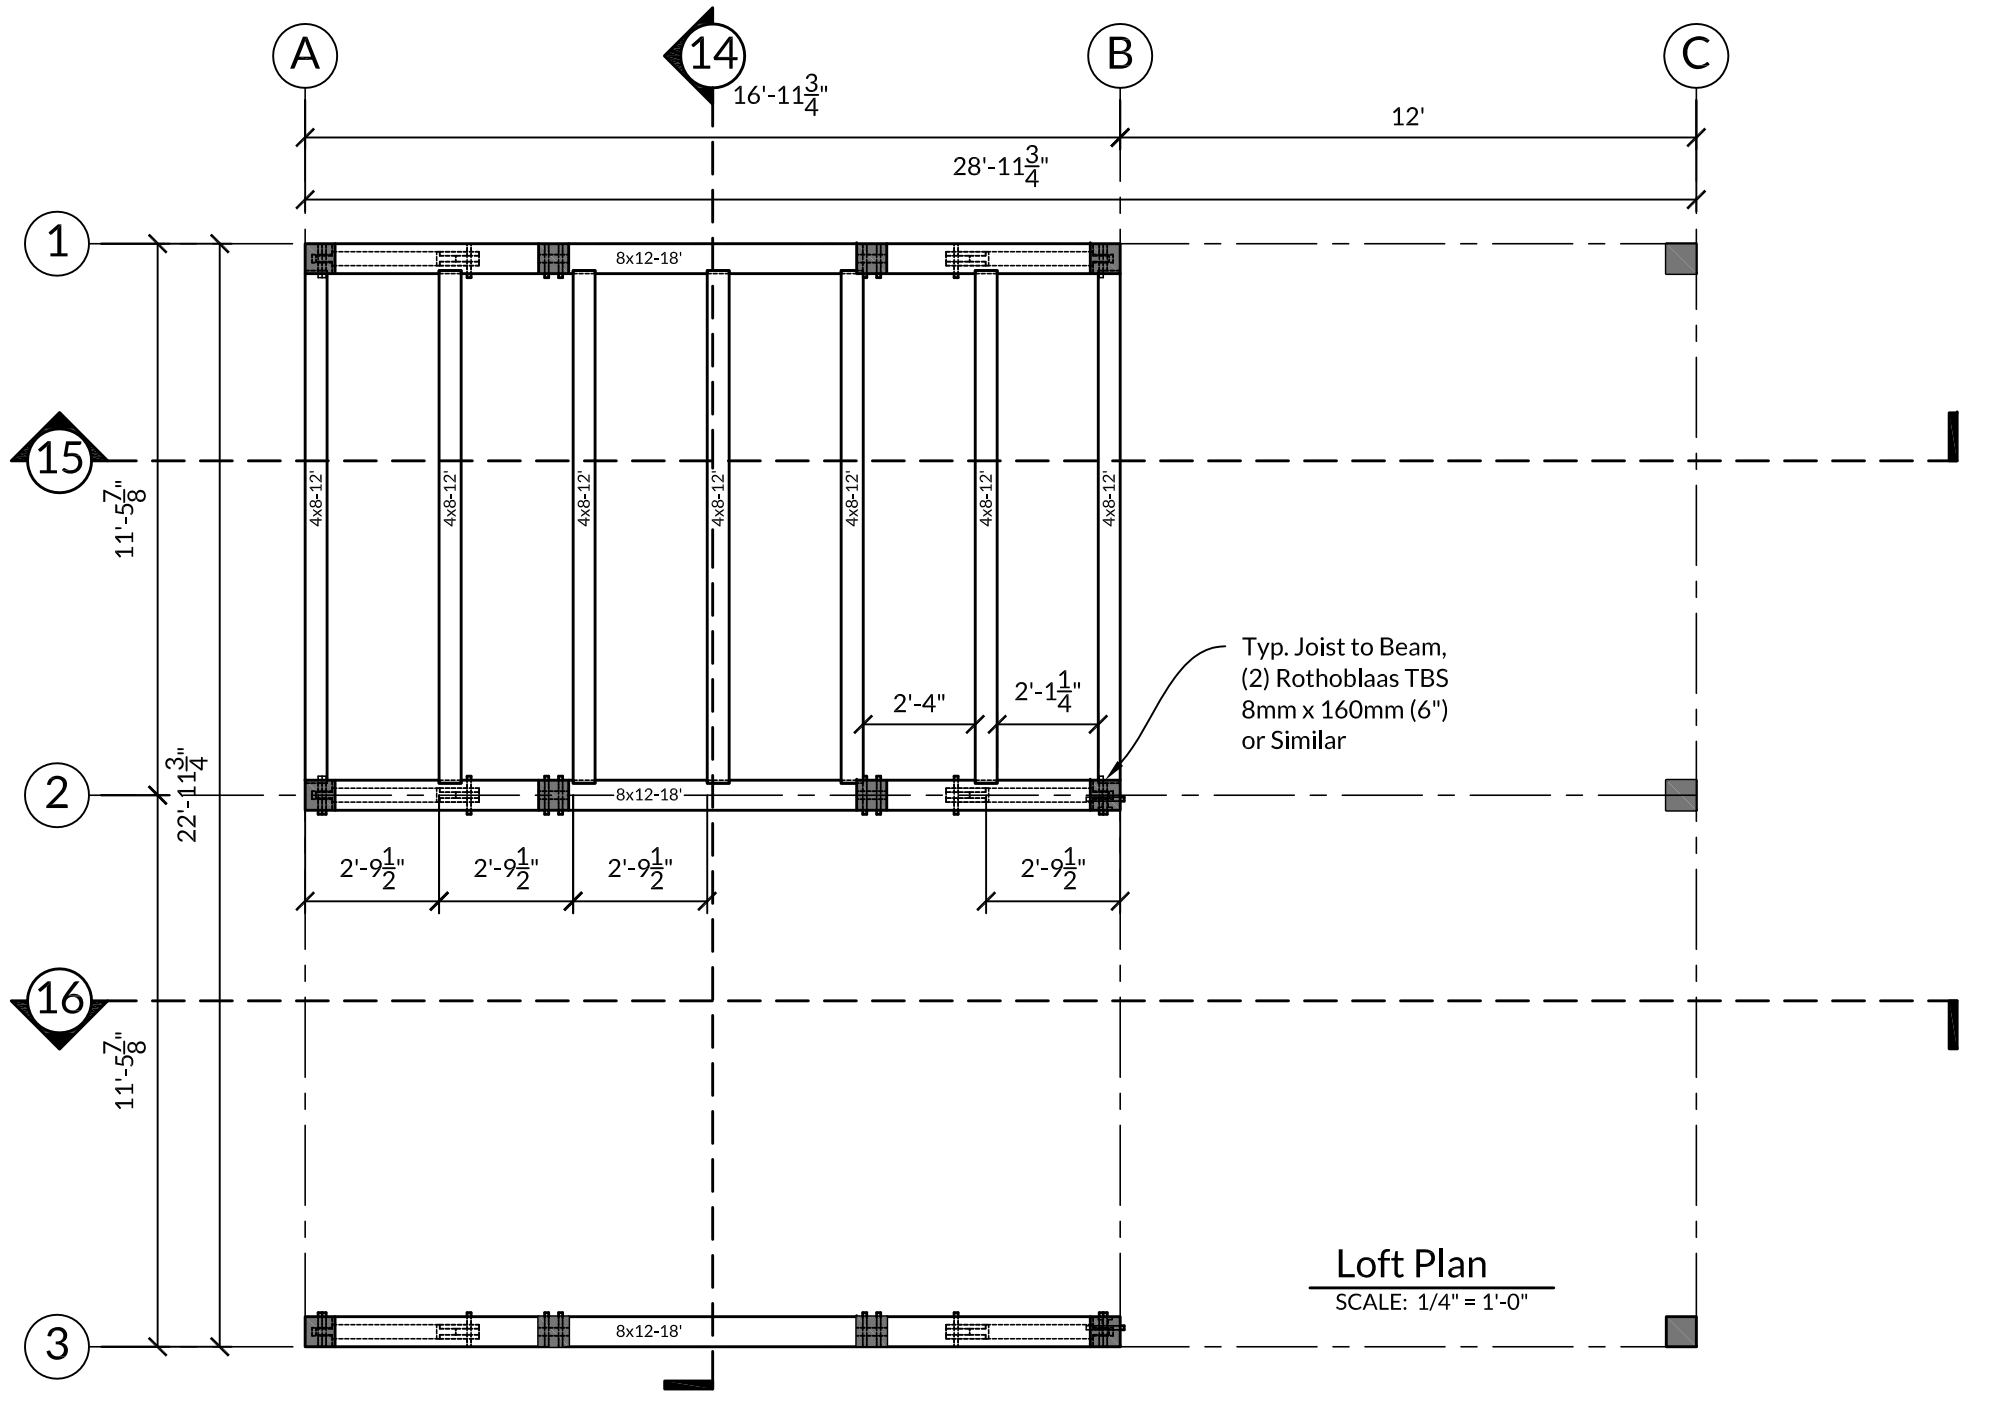

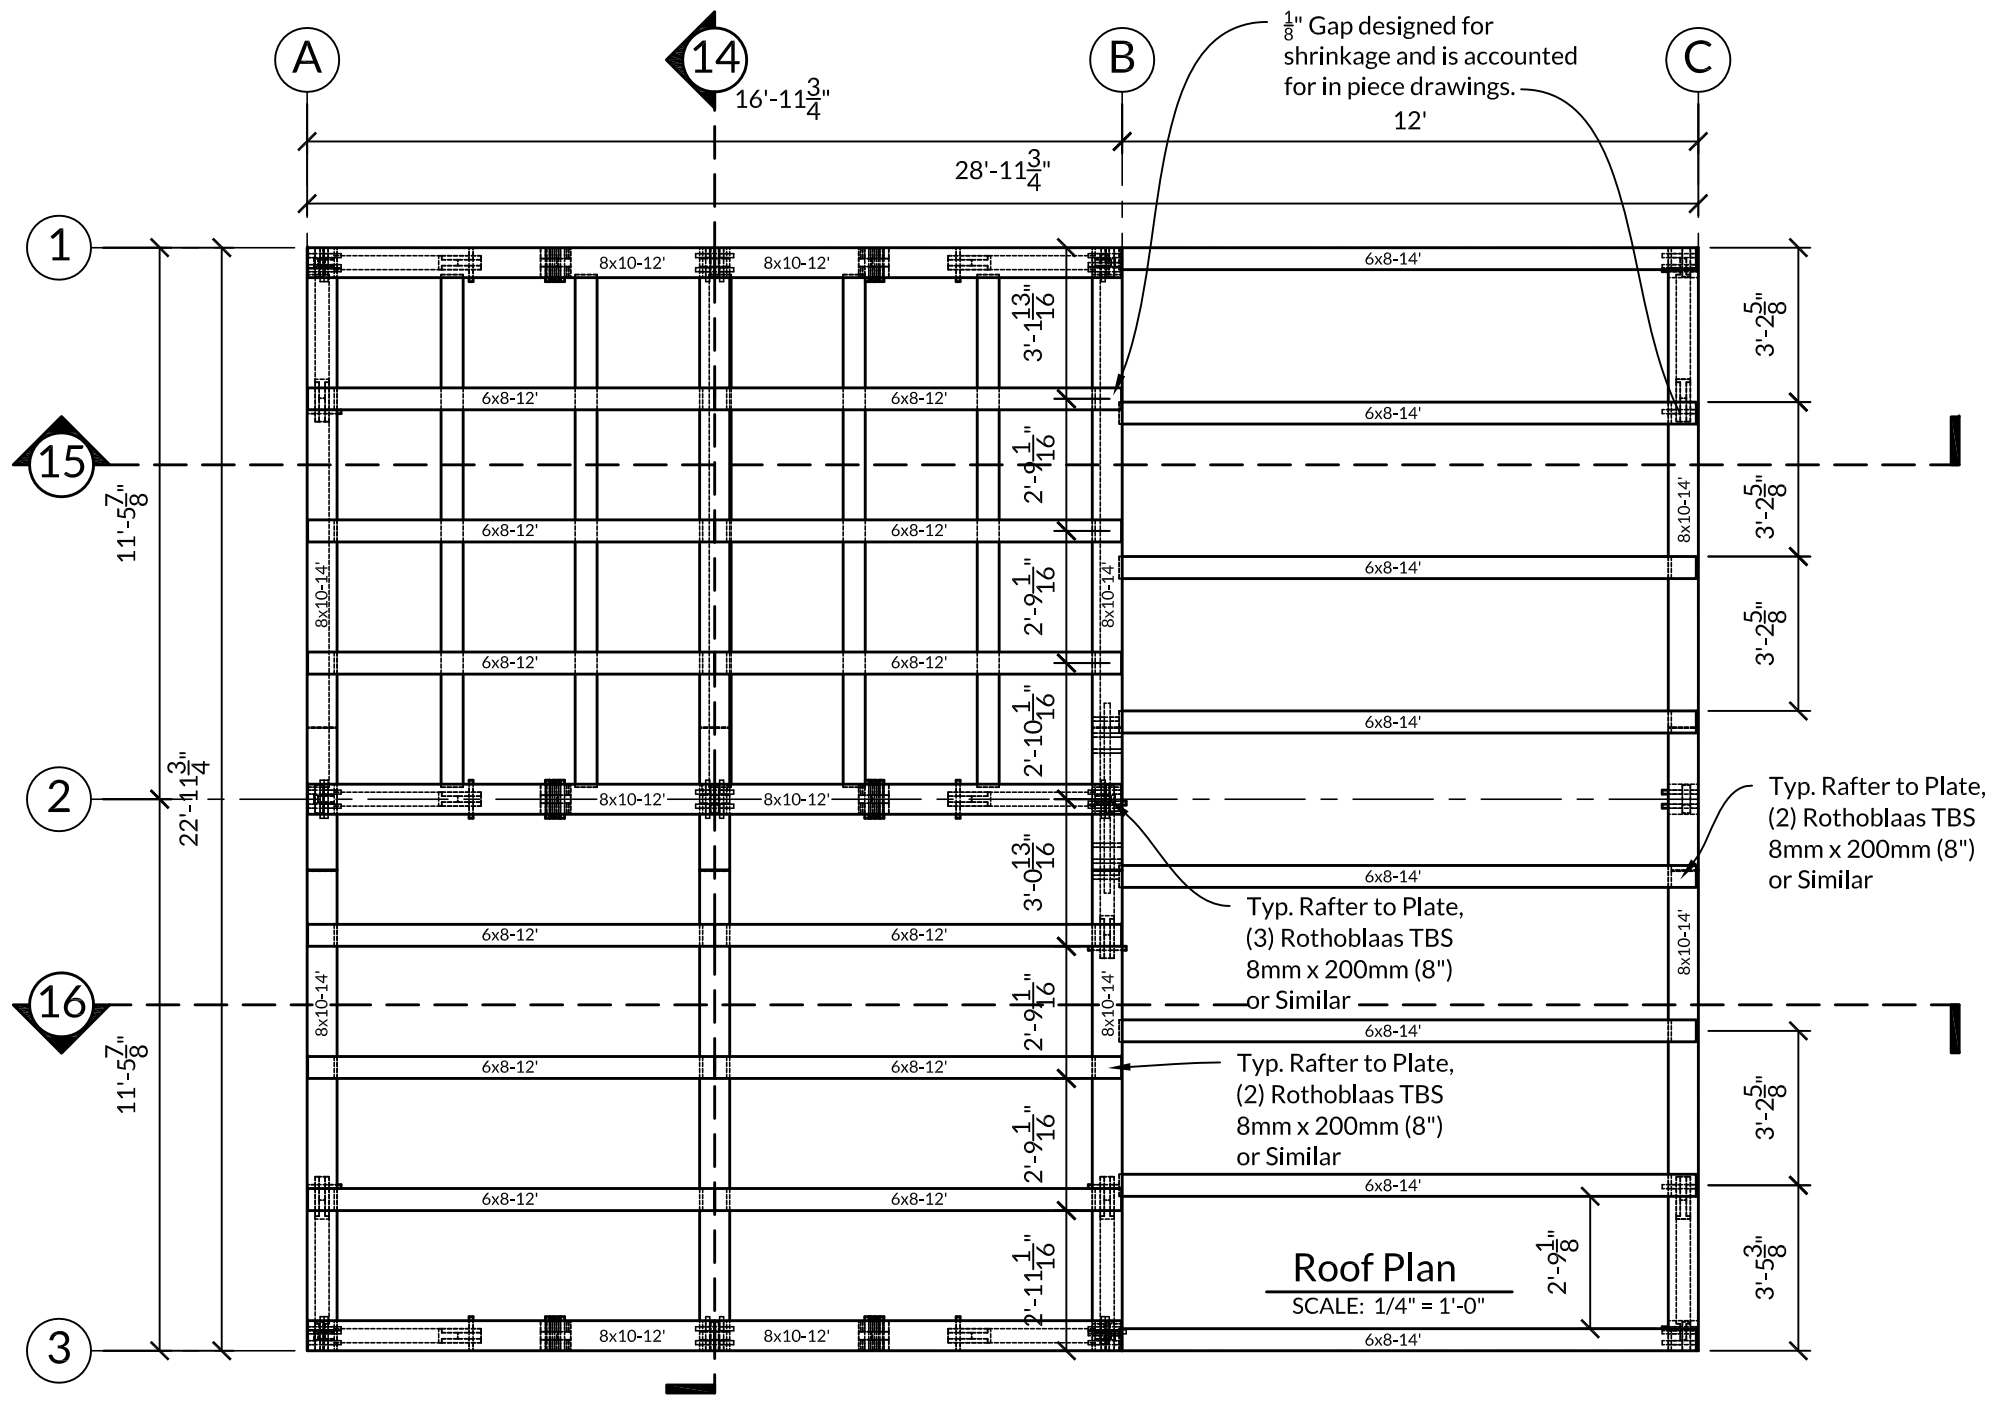


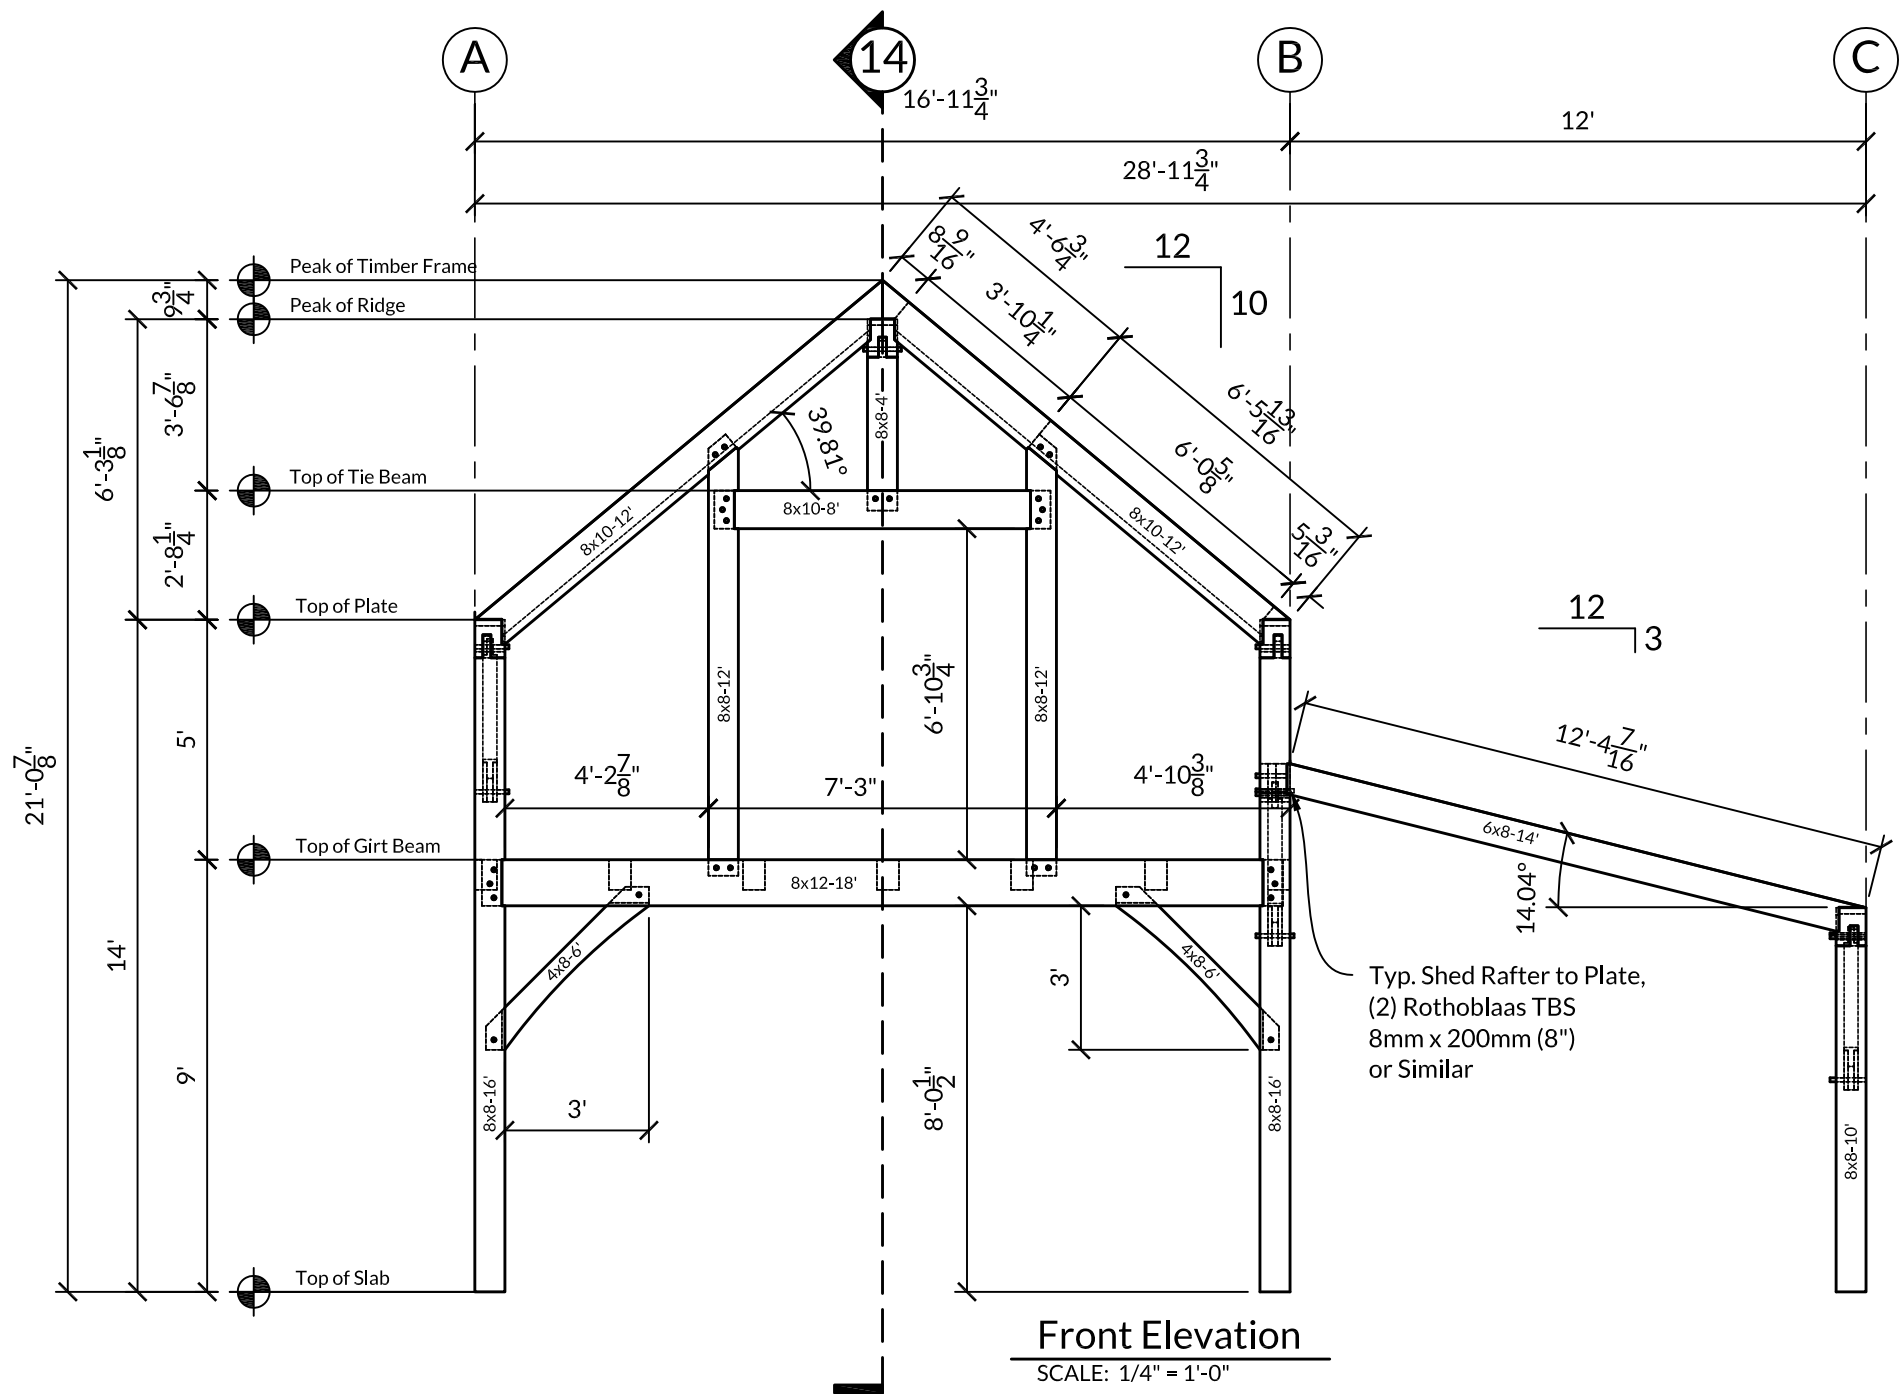


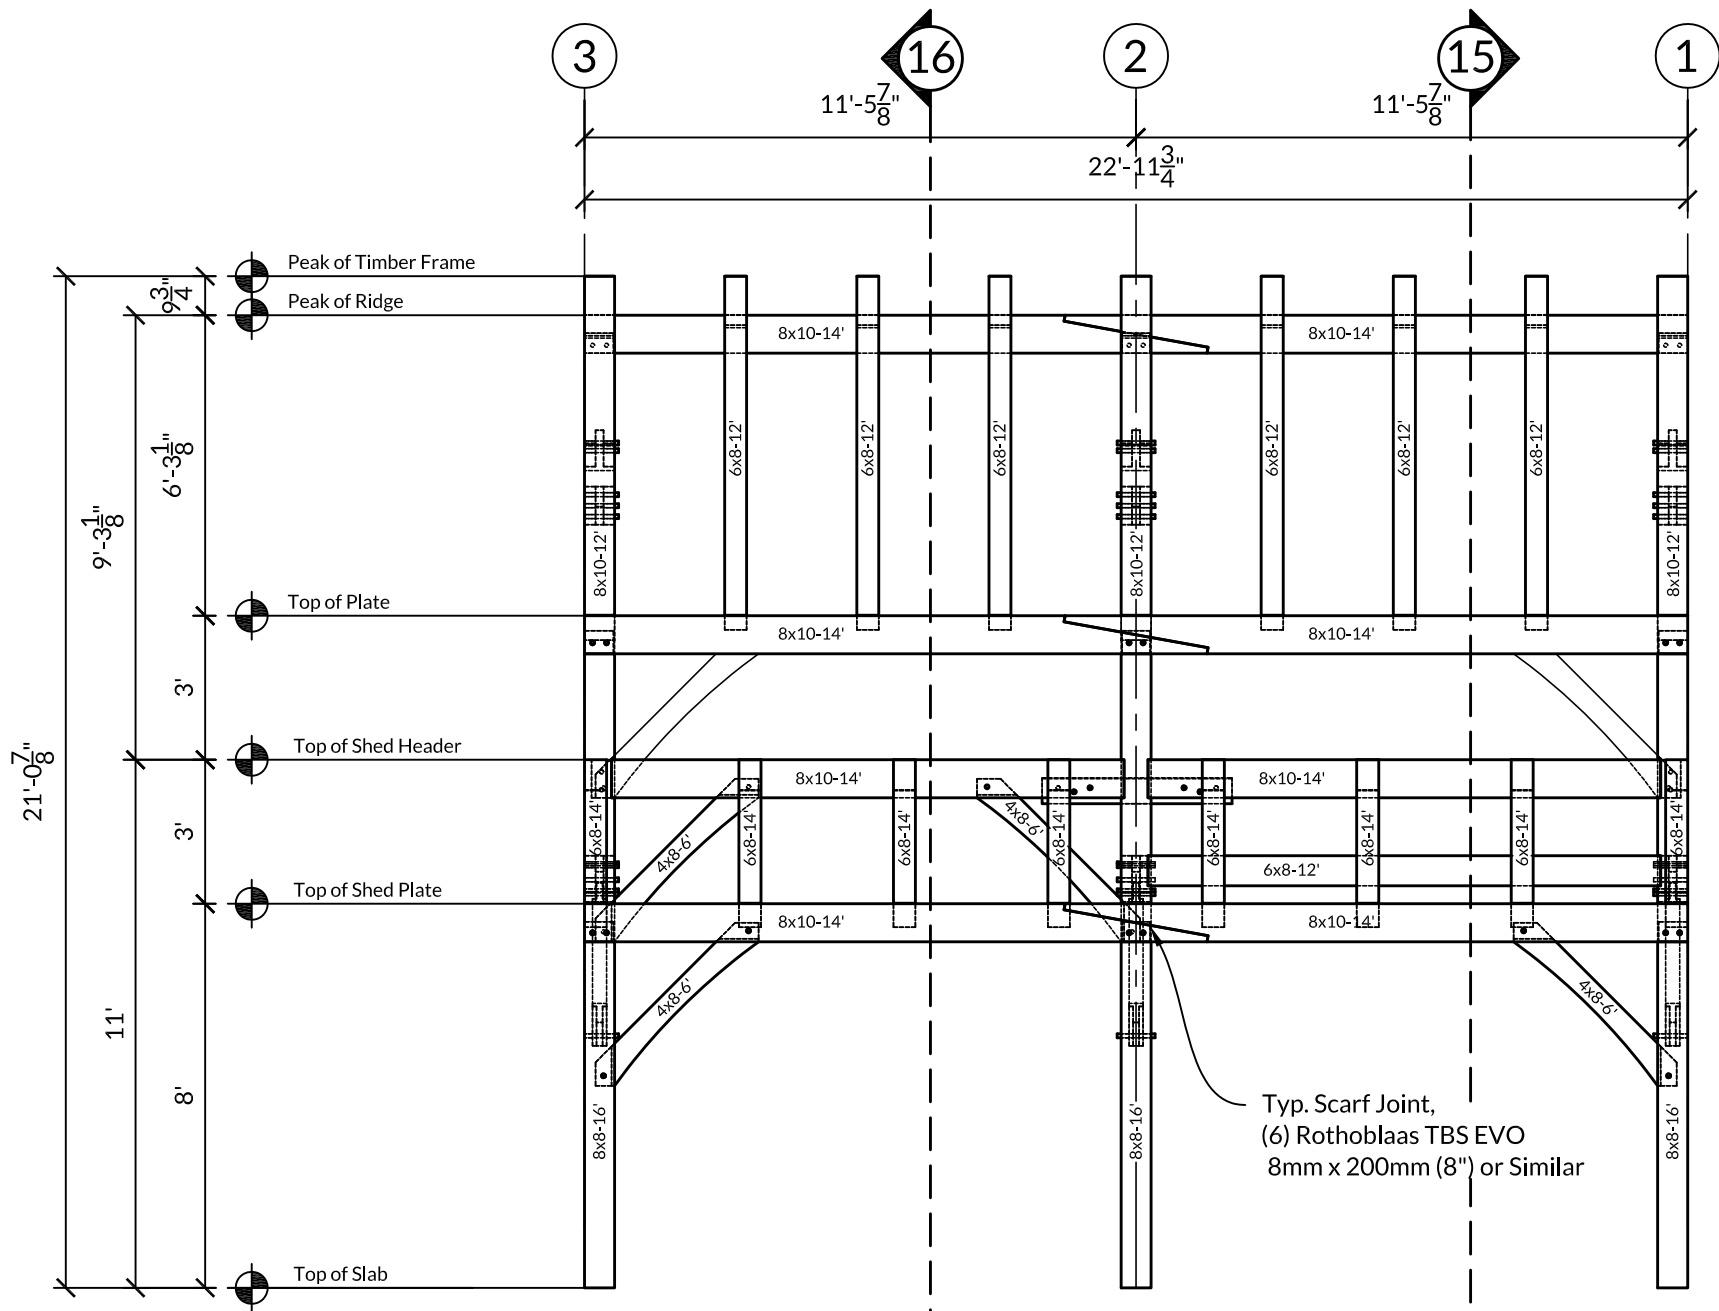



Right Elevation


SCALE: 1/4" = 1'-0"


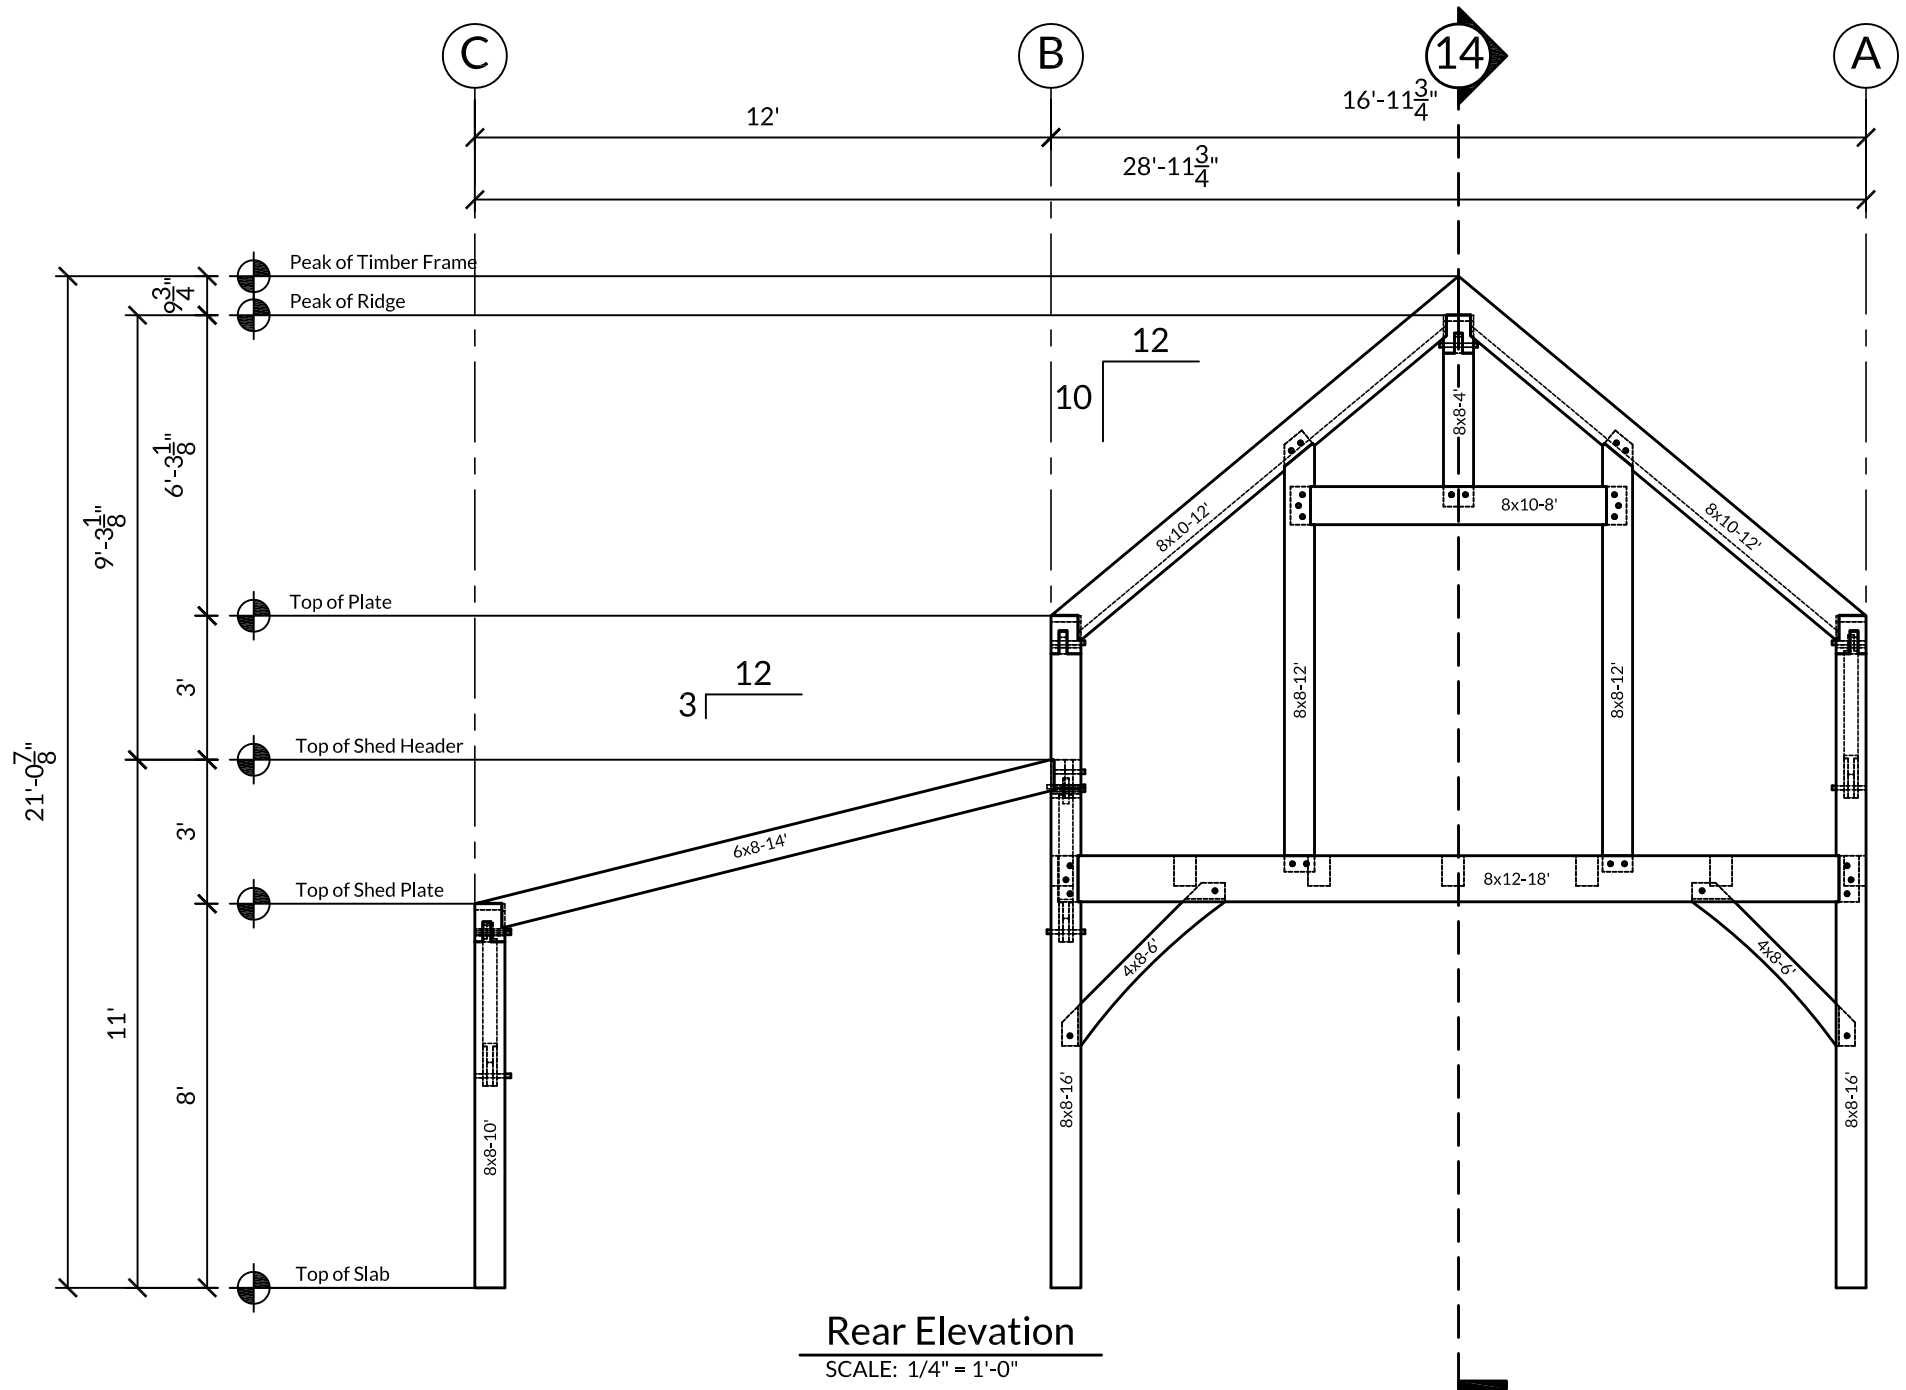


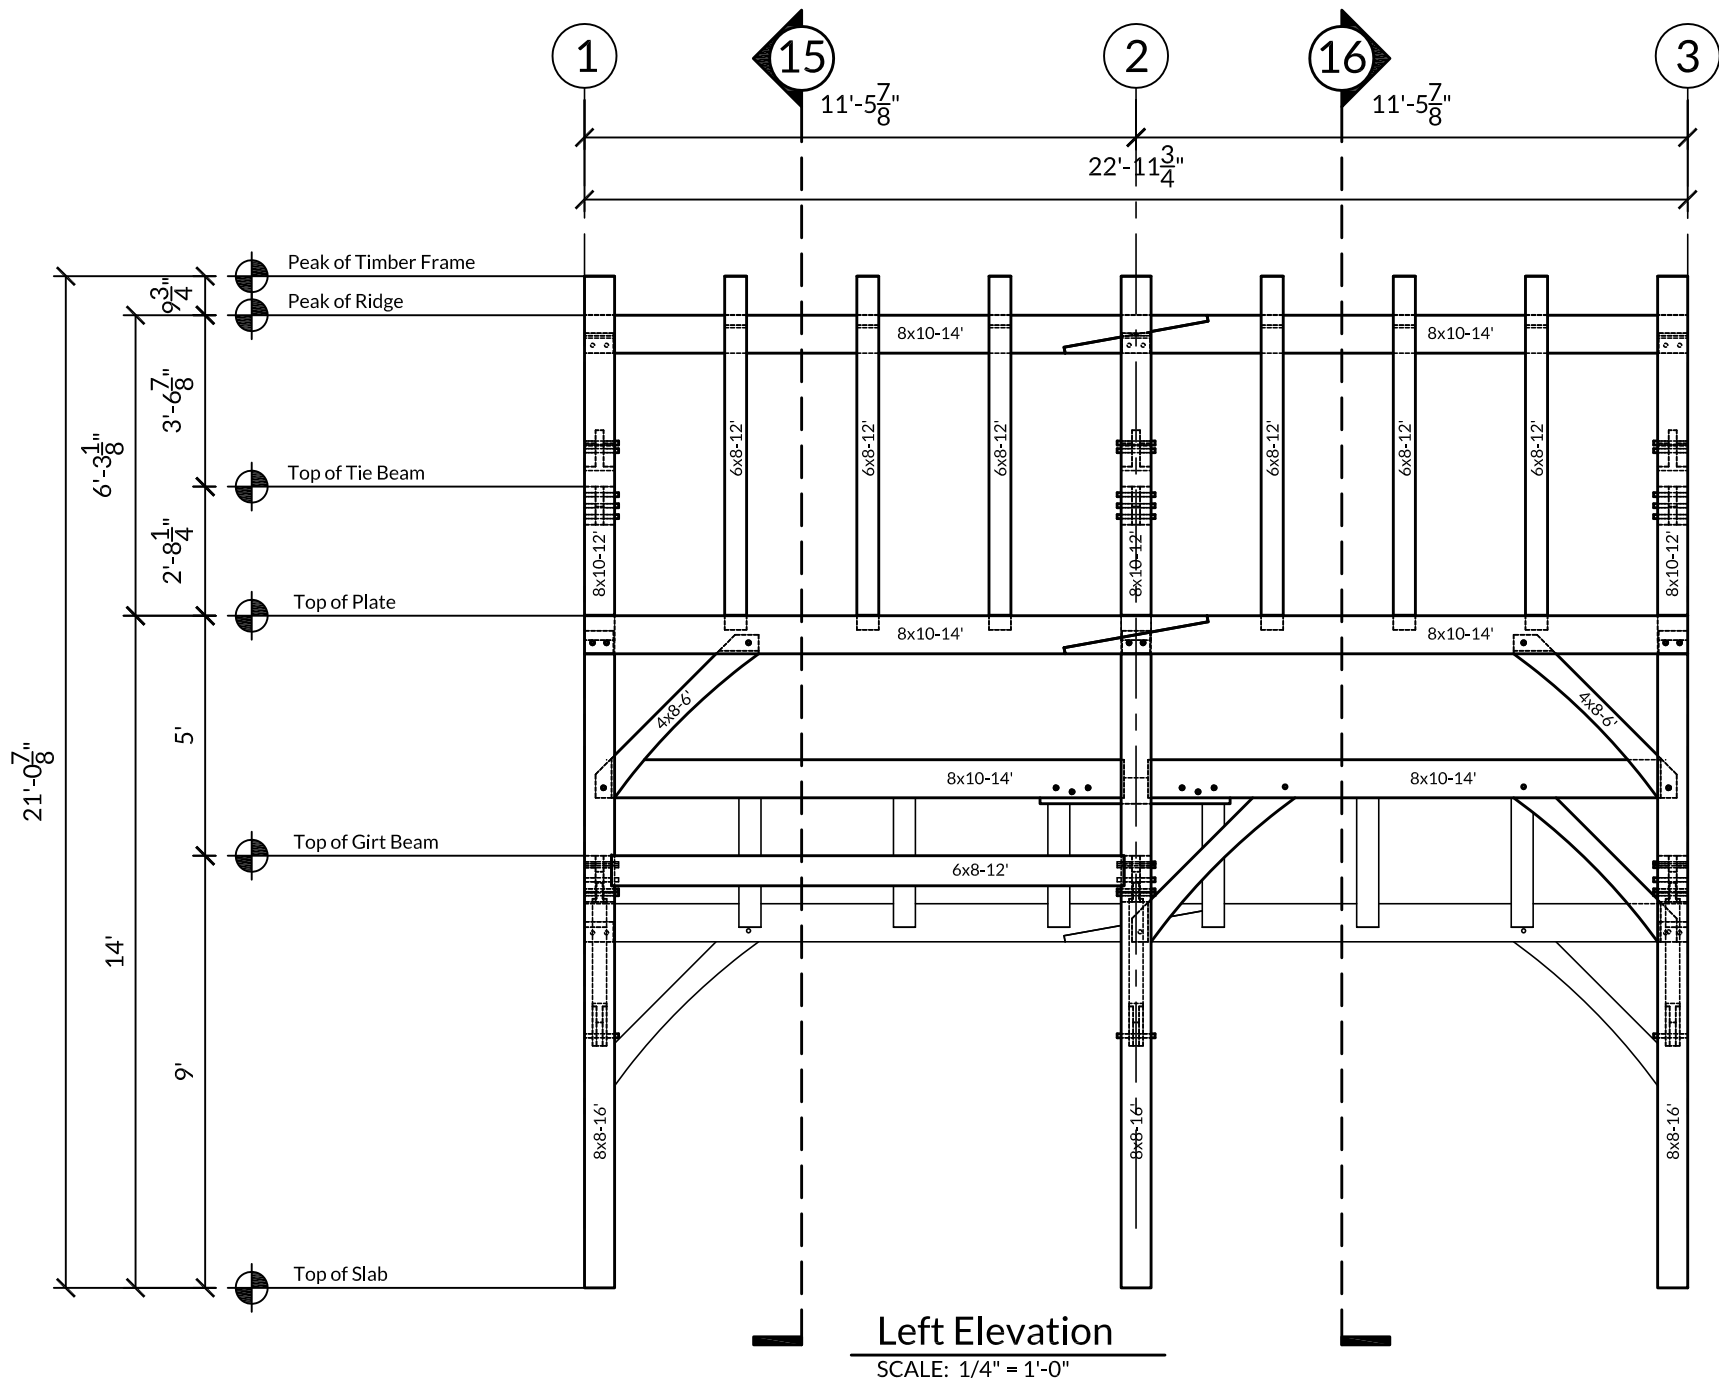


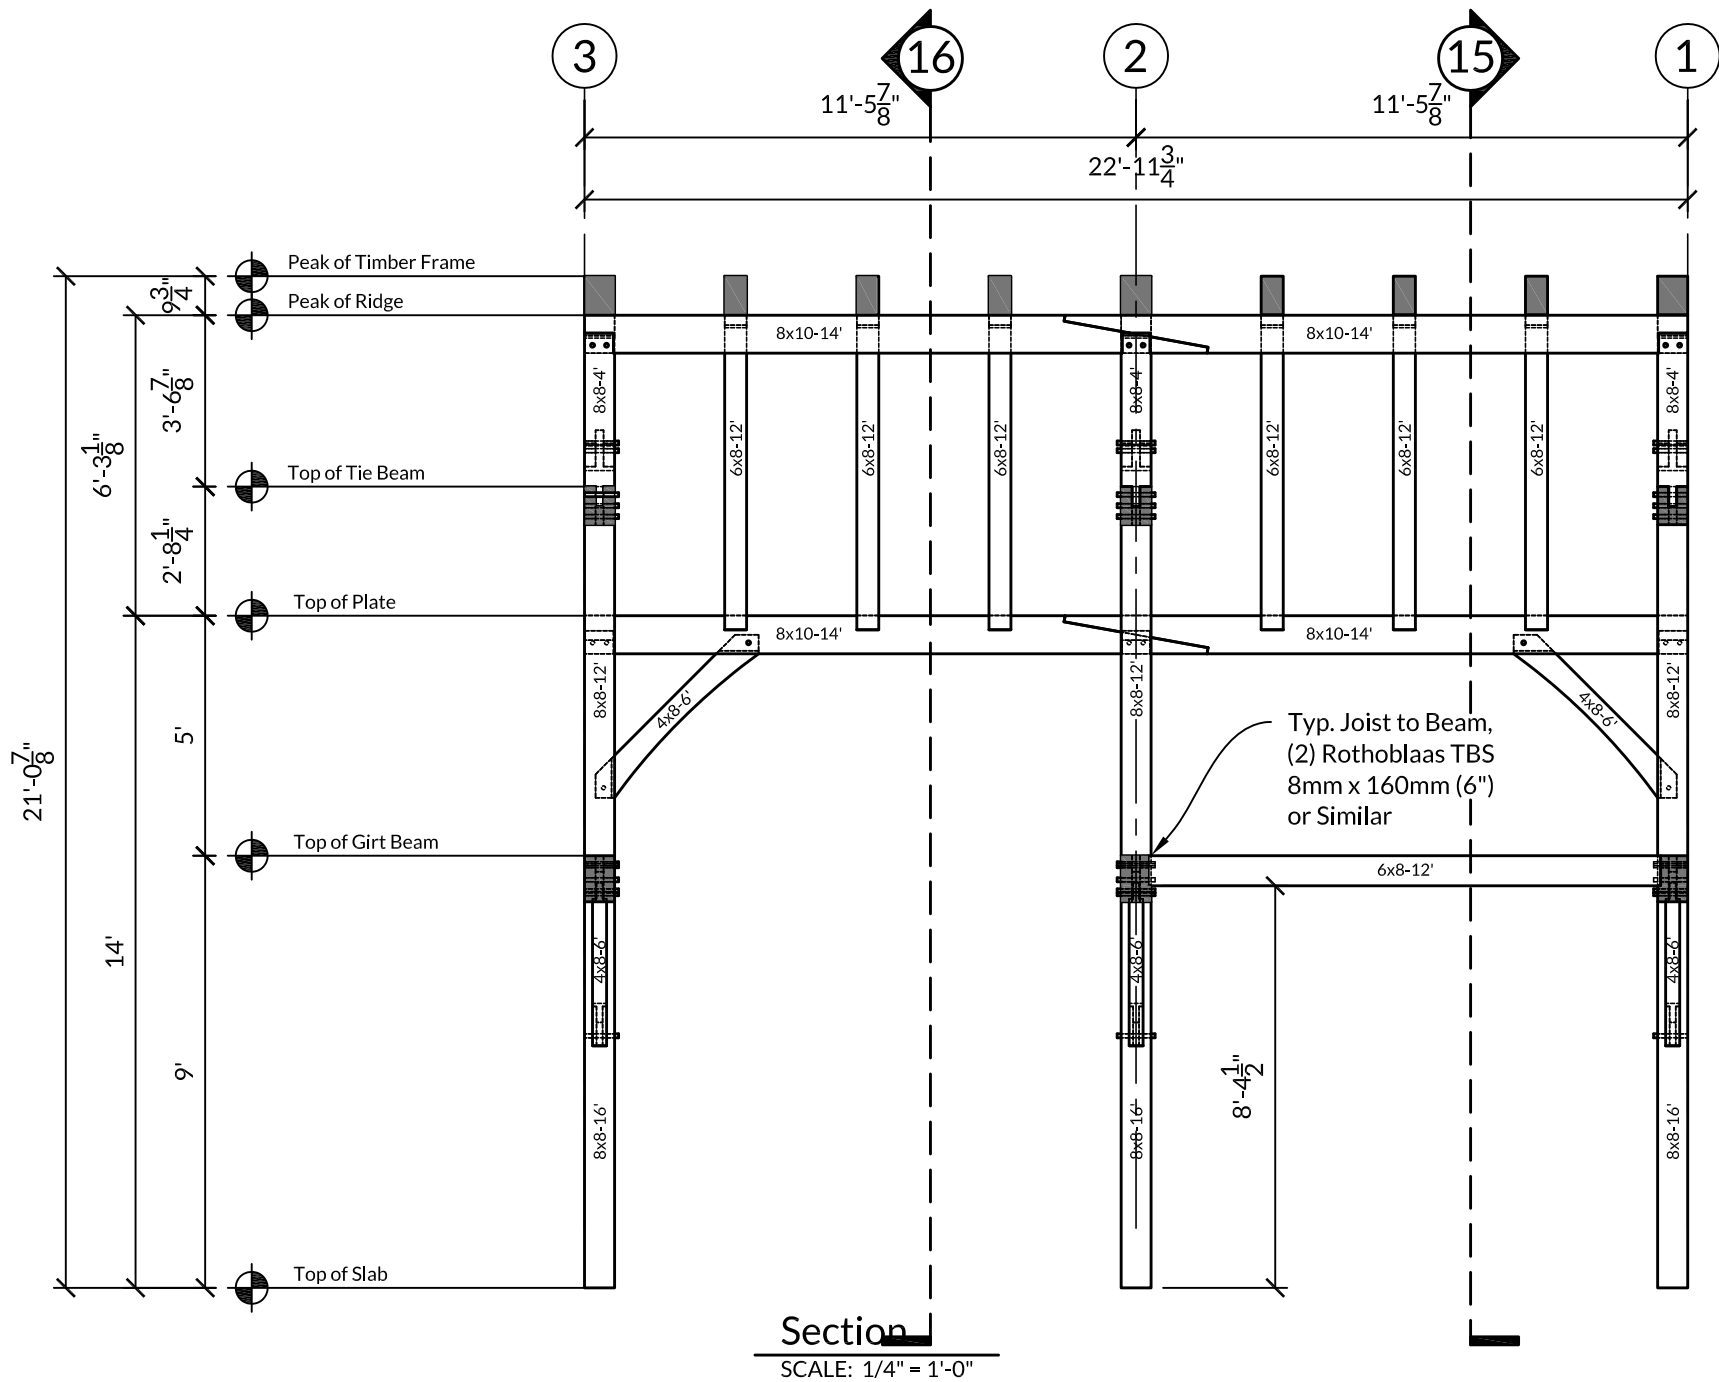


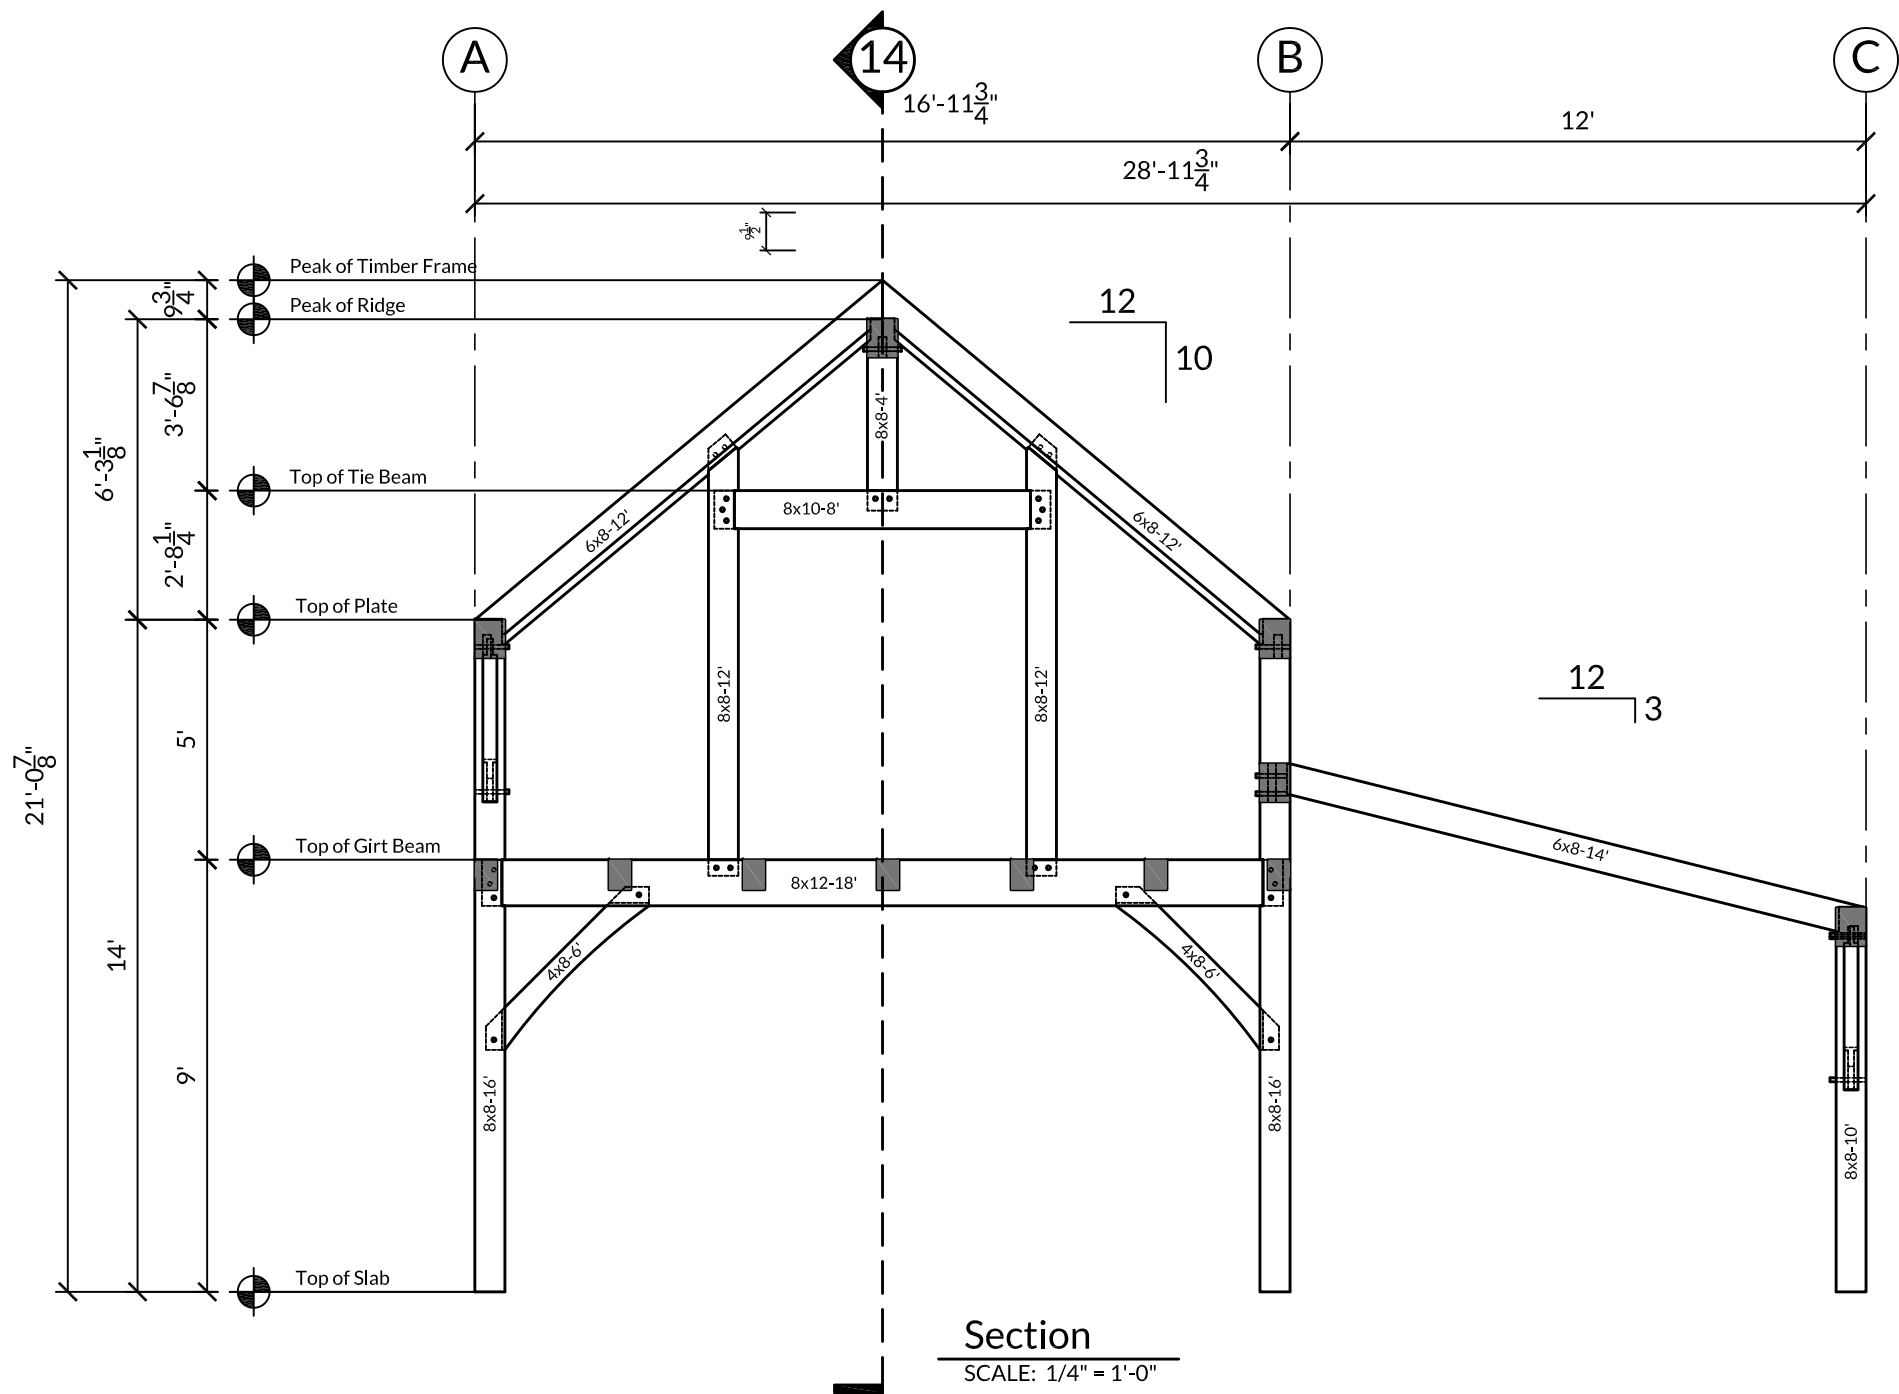

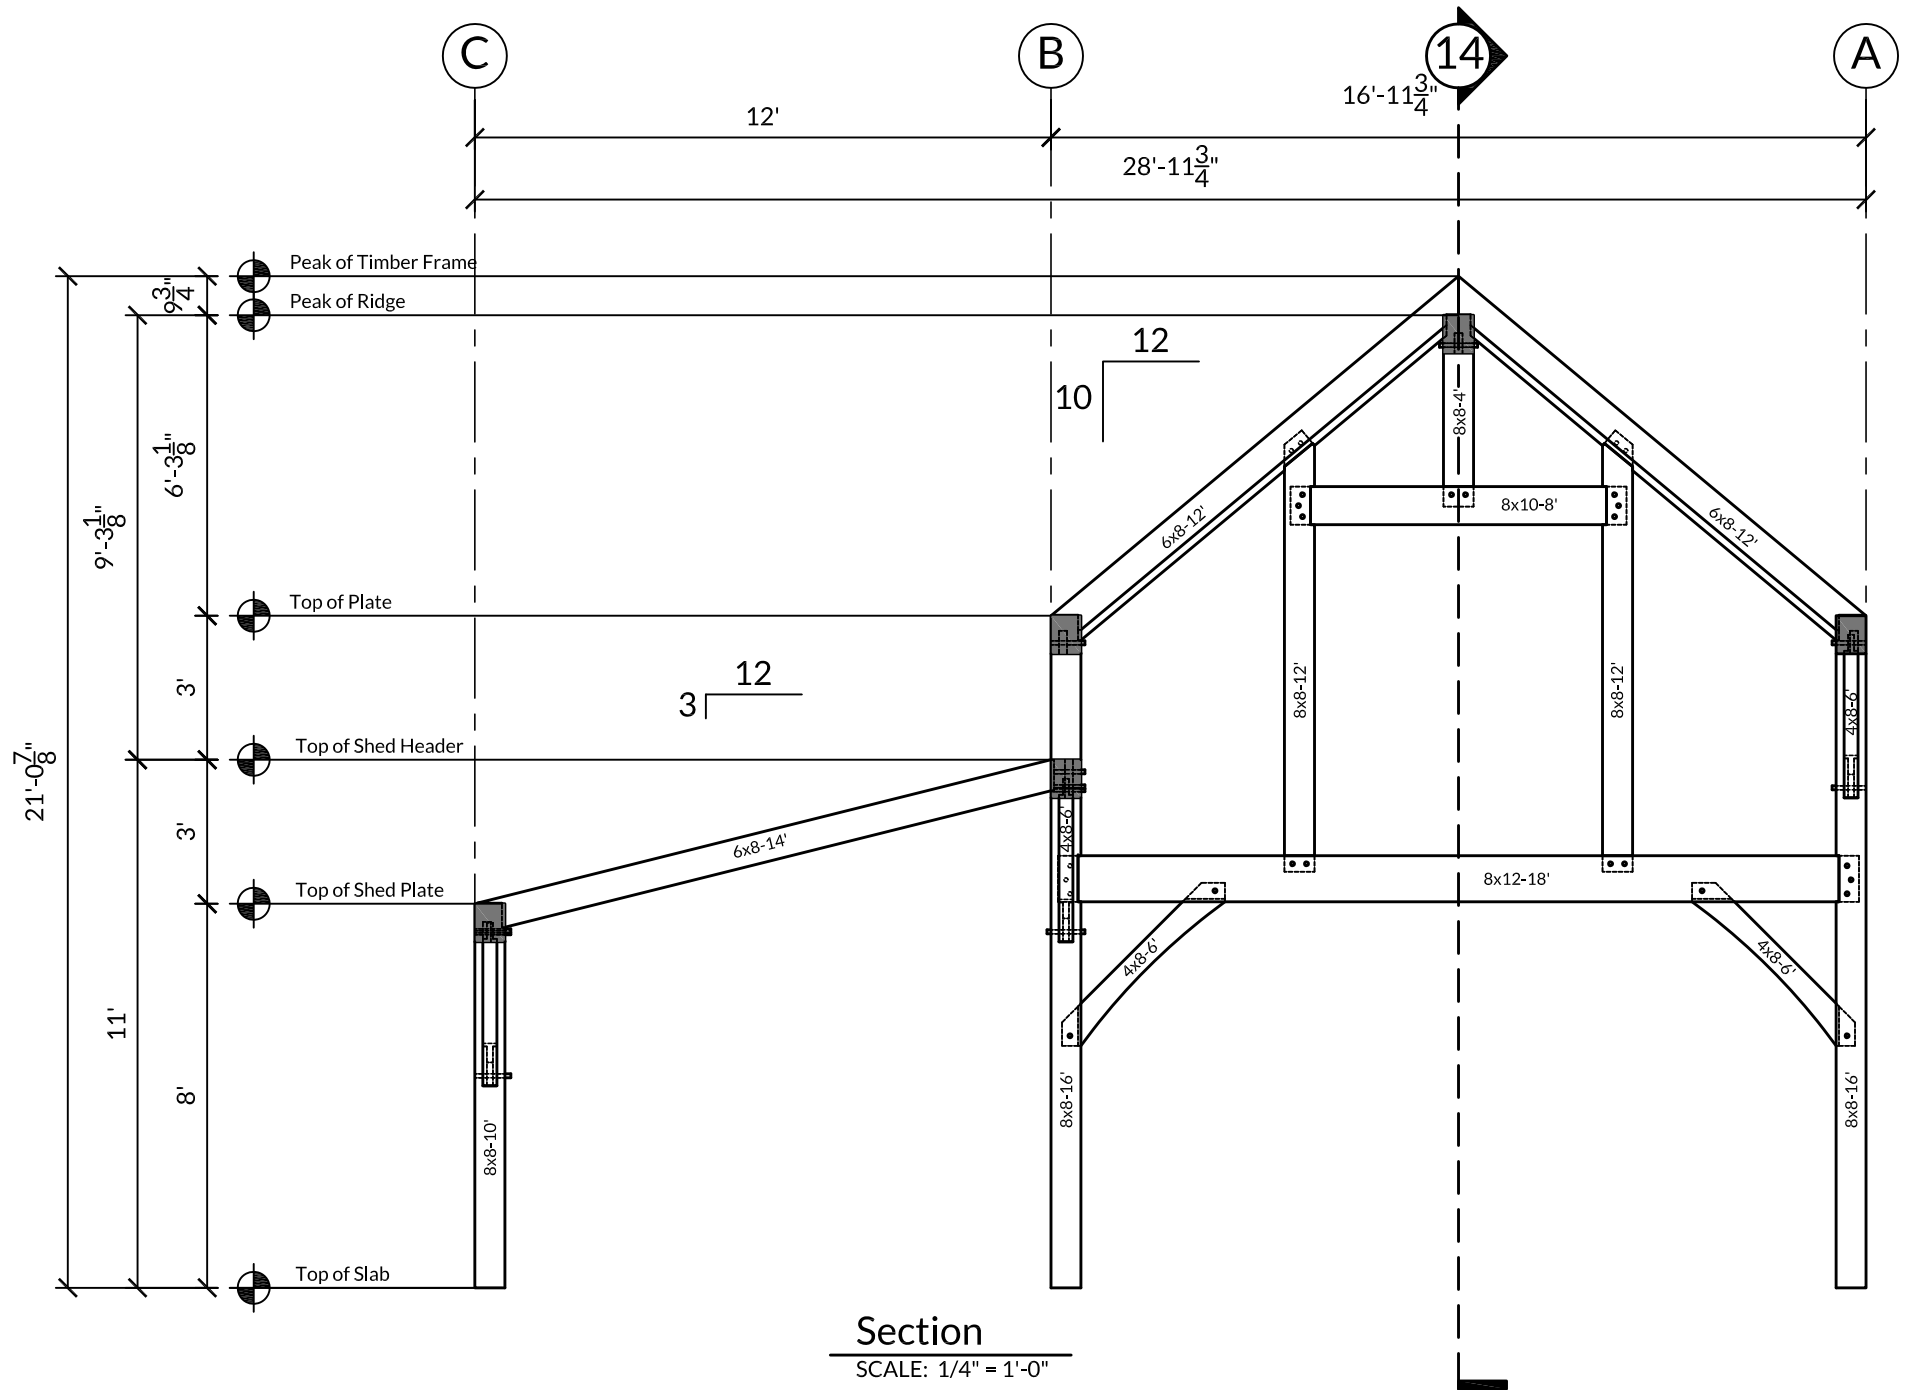


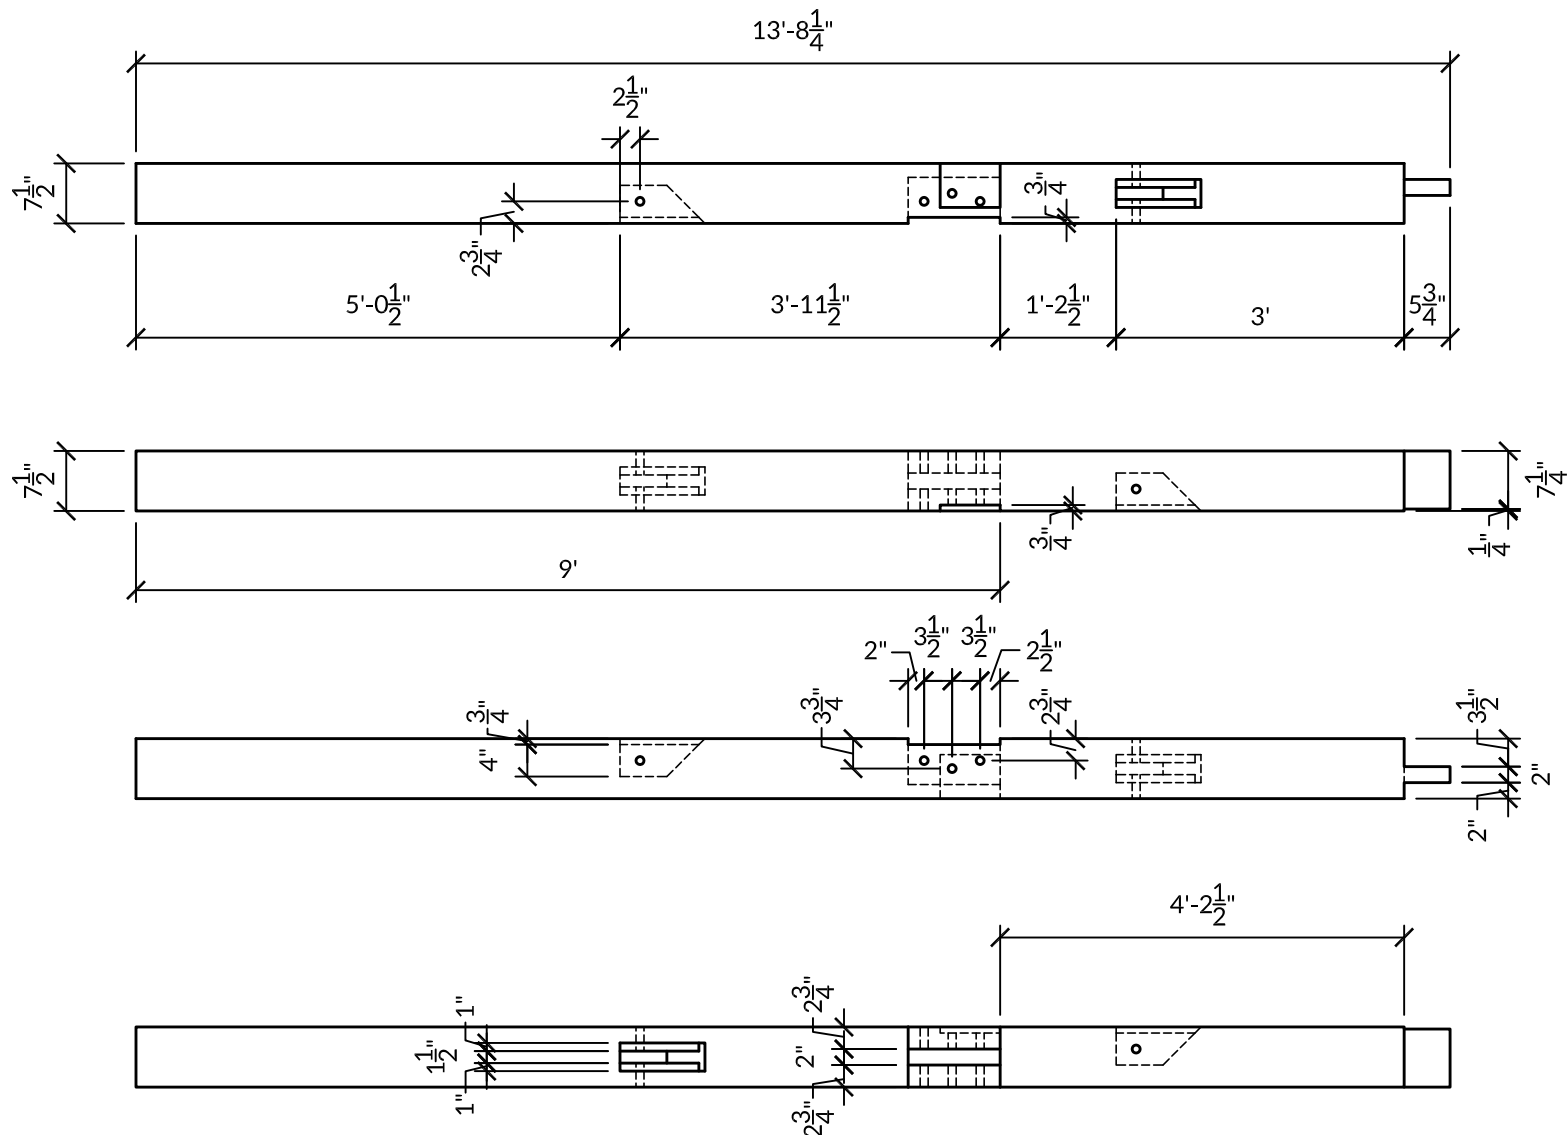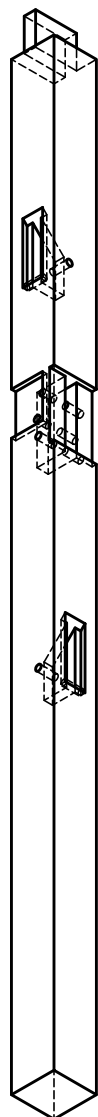


Grid Line 1A Post
Qty: 1

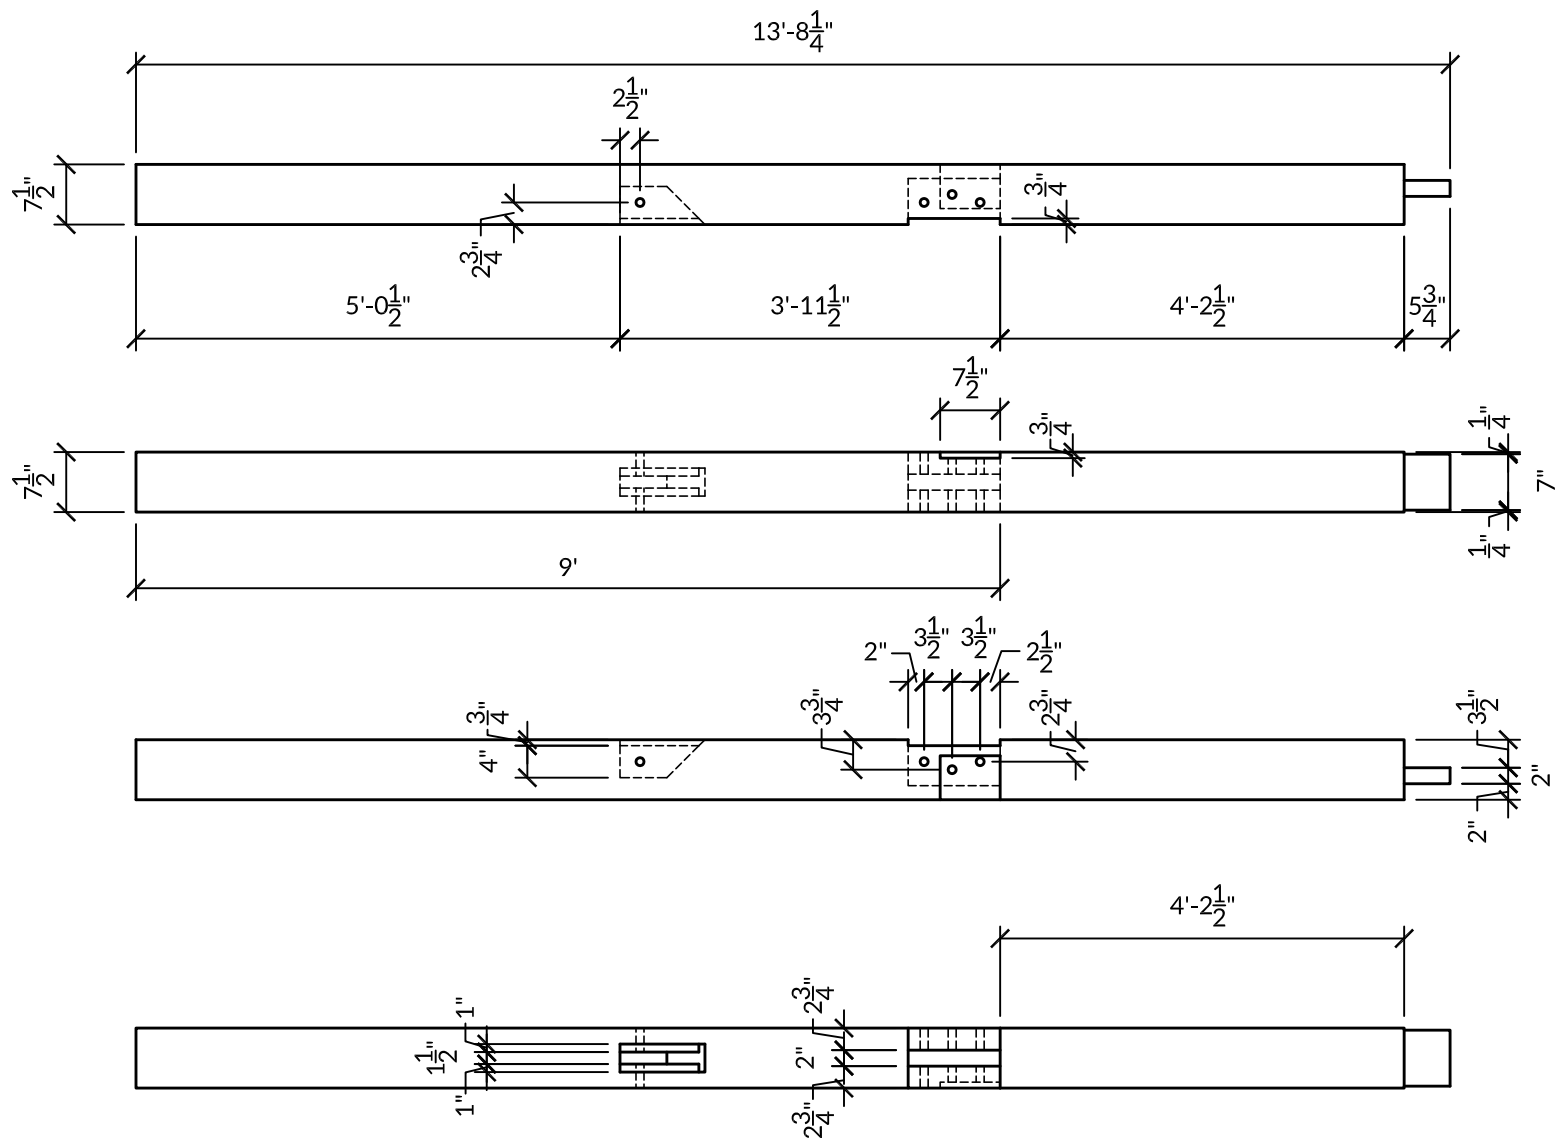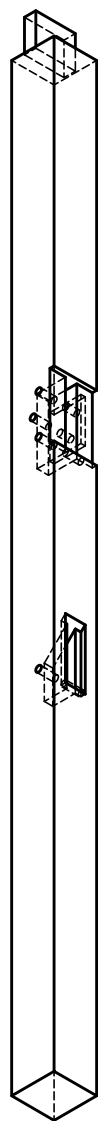



Grid Line 2A Post
Qty: 1

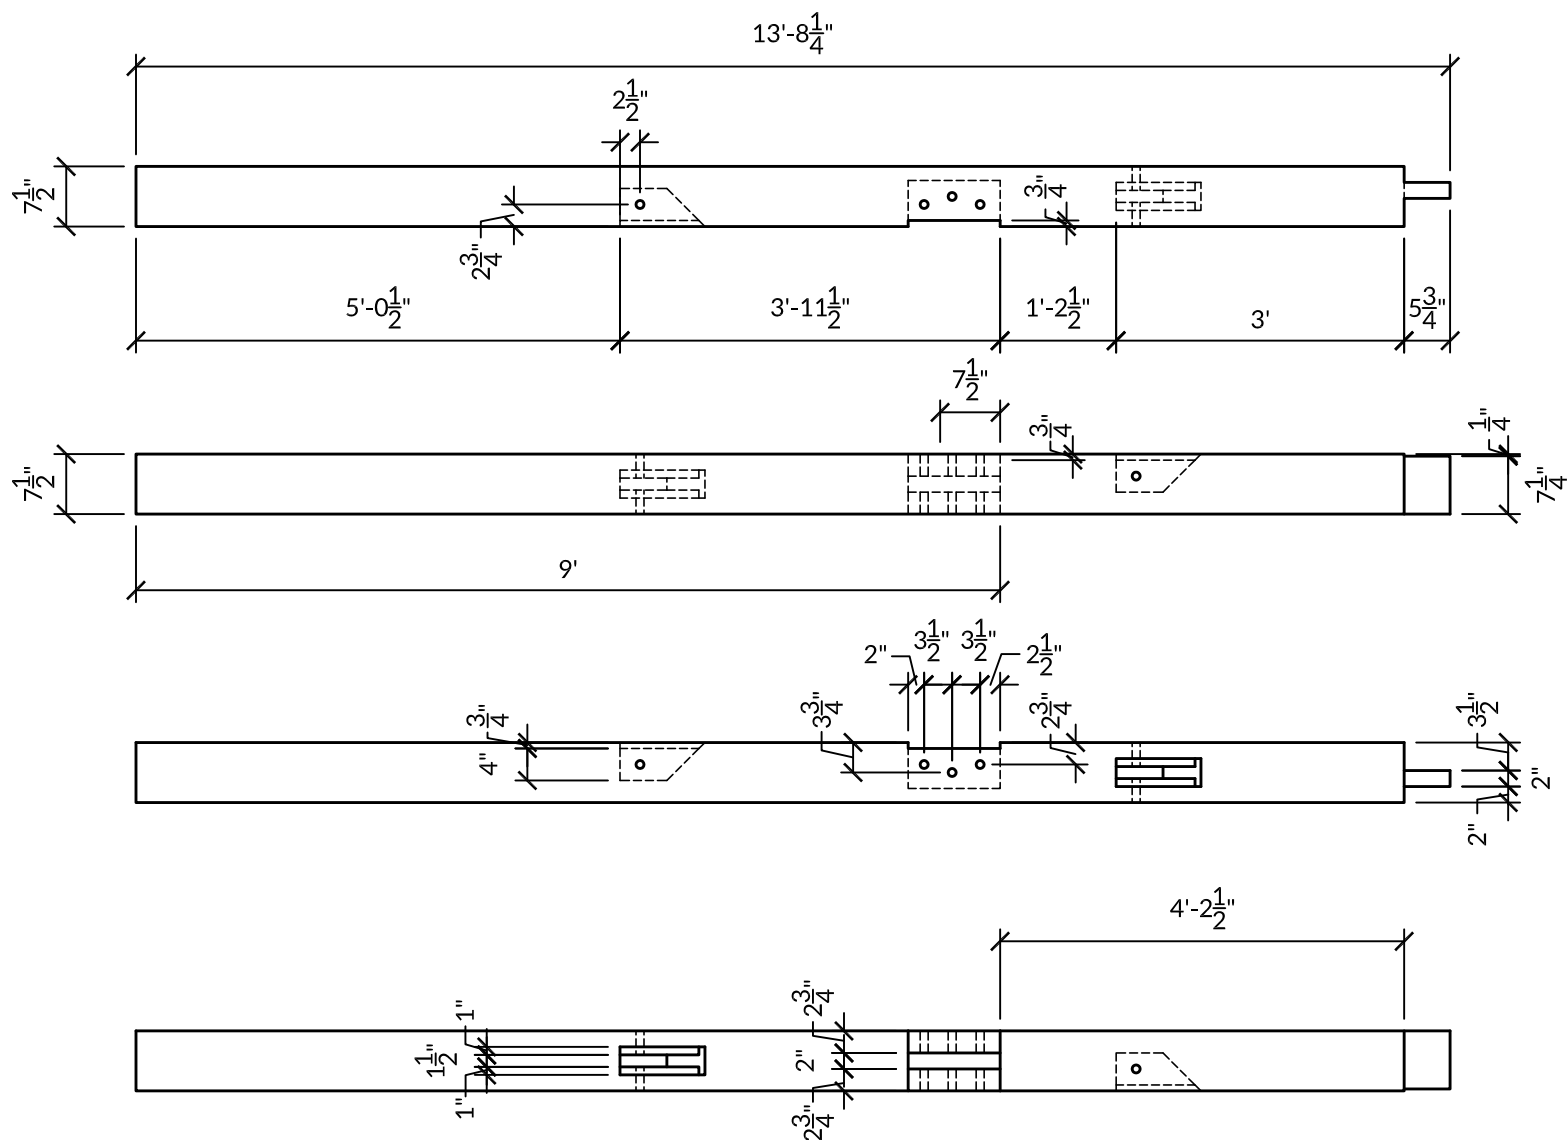



Grid Line 3A Post
Qty: 1

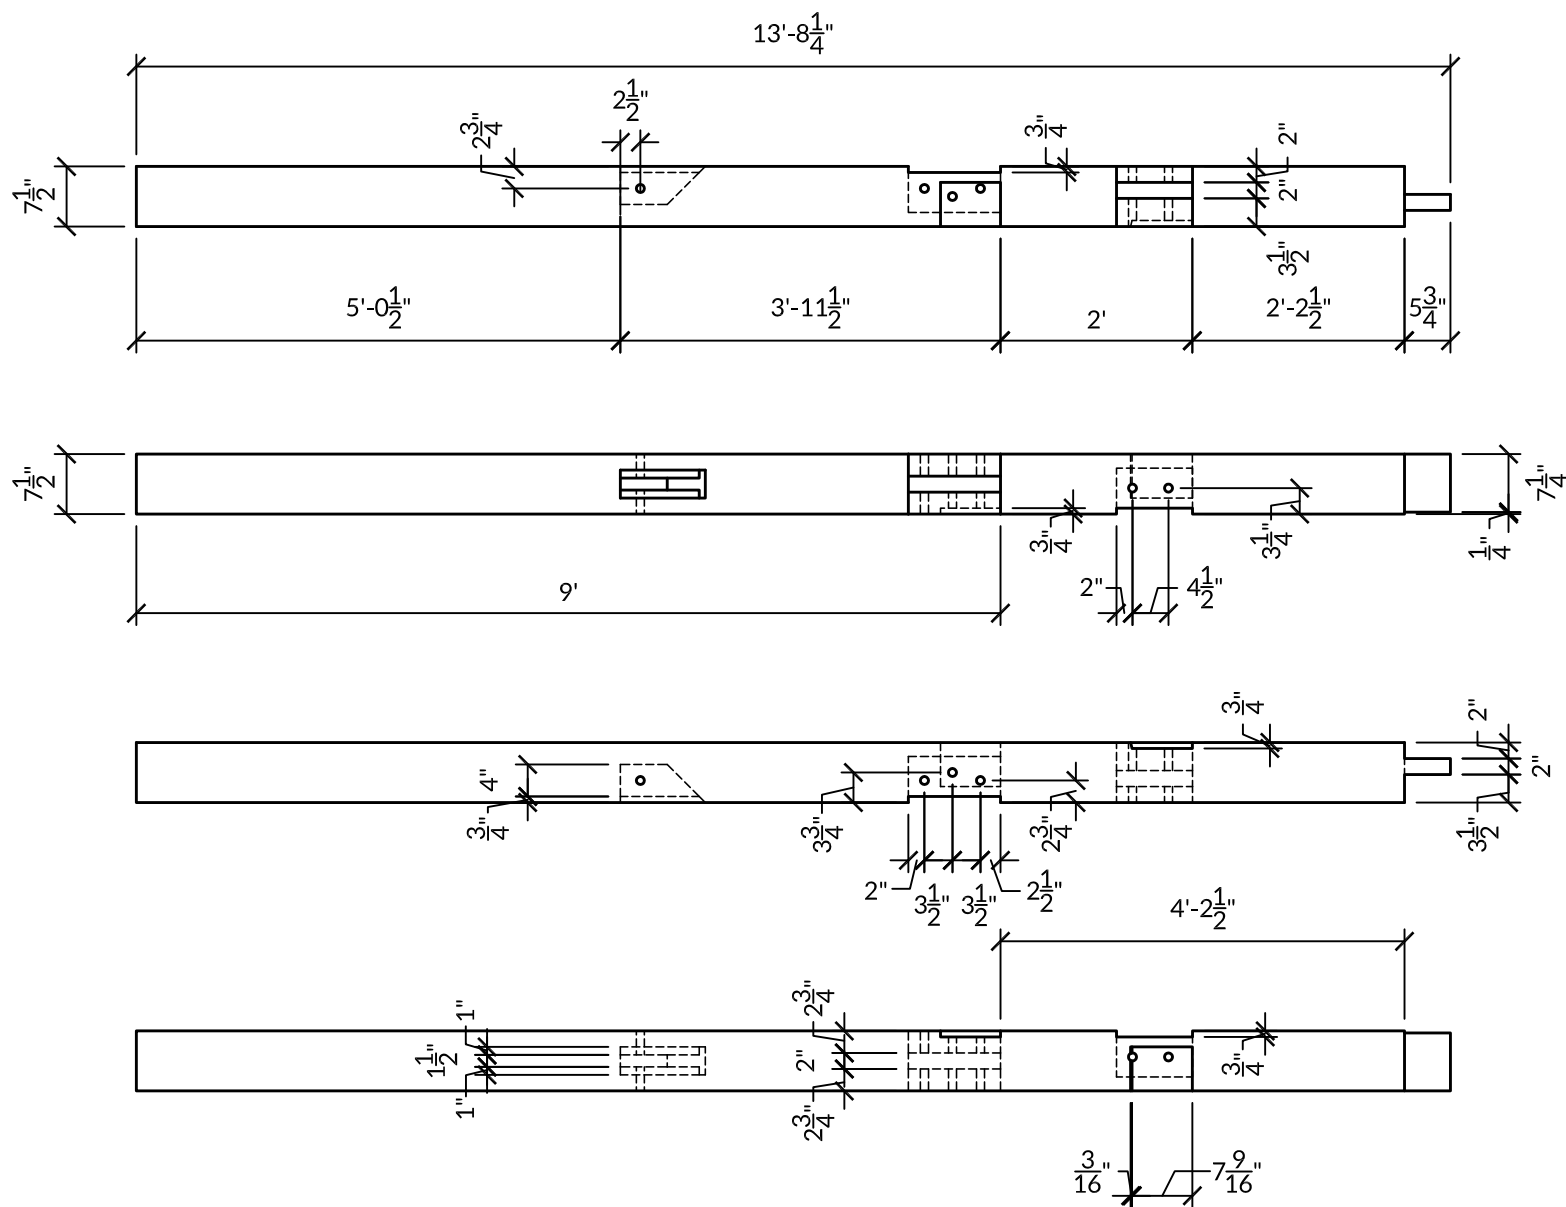



Grid Line 1B Post
Qty: 1

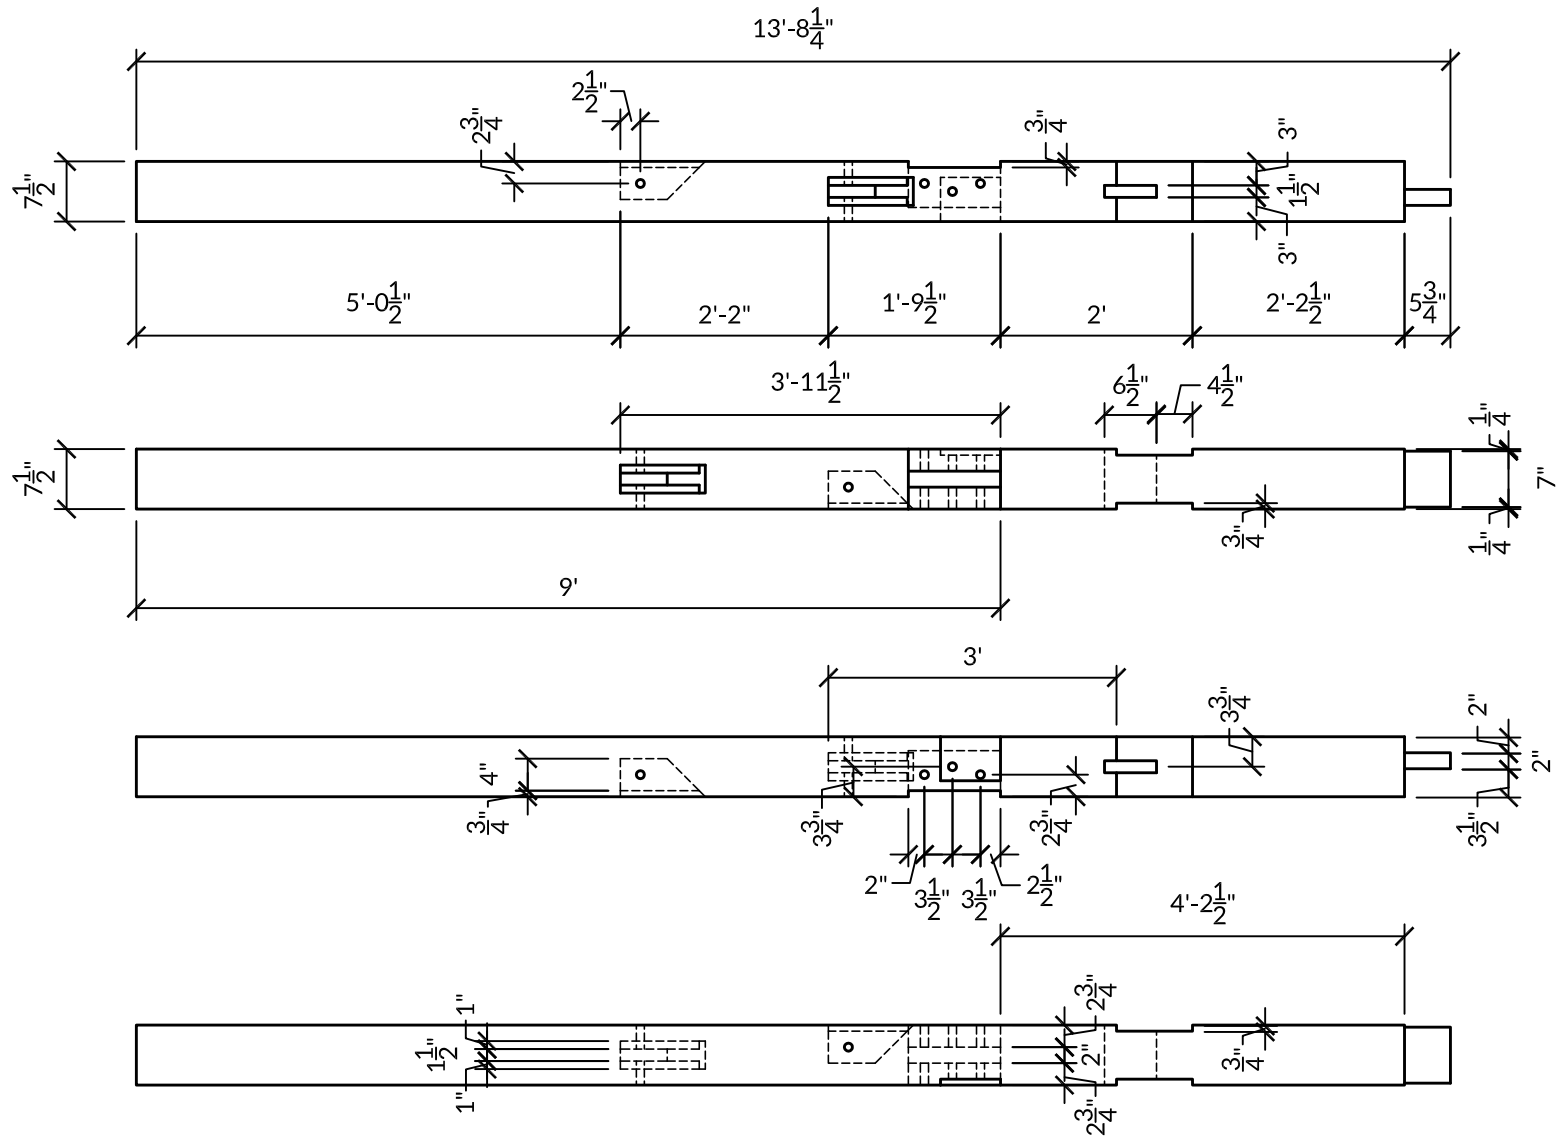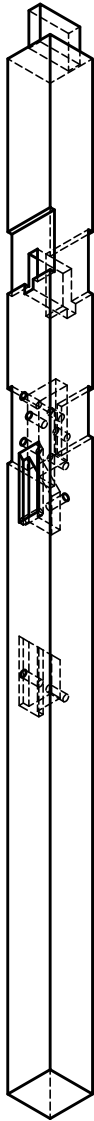



Grid Line 2B Post
Qty: 1

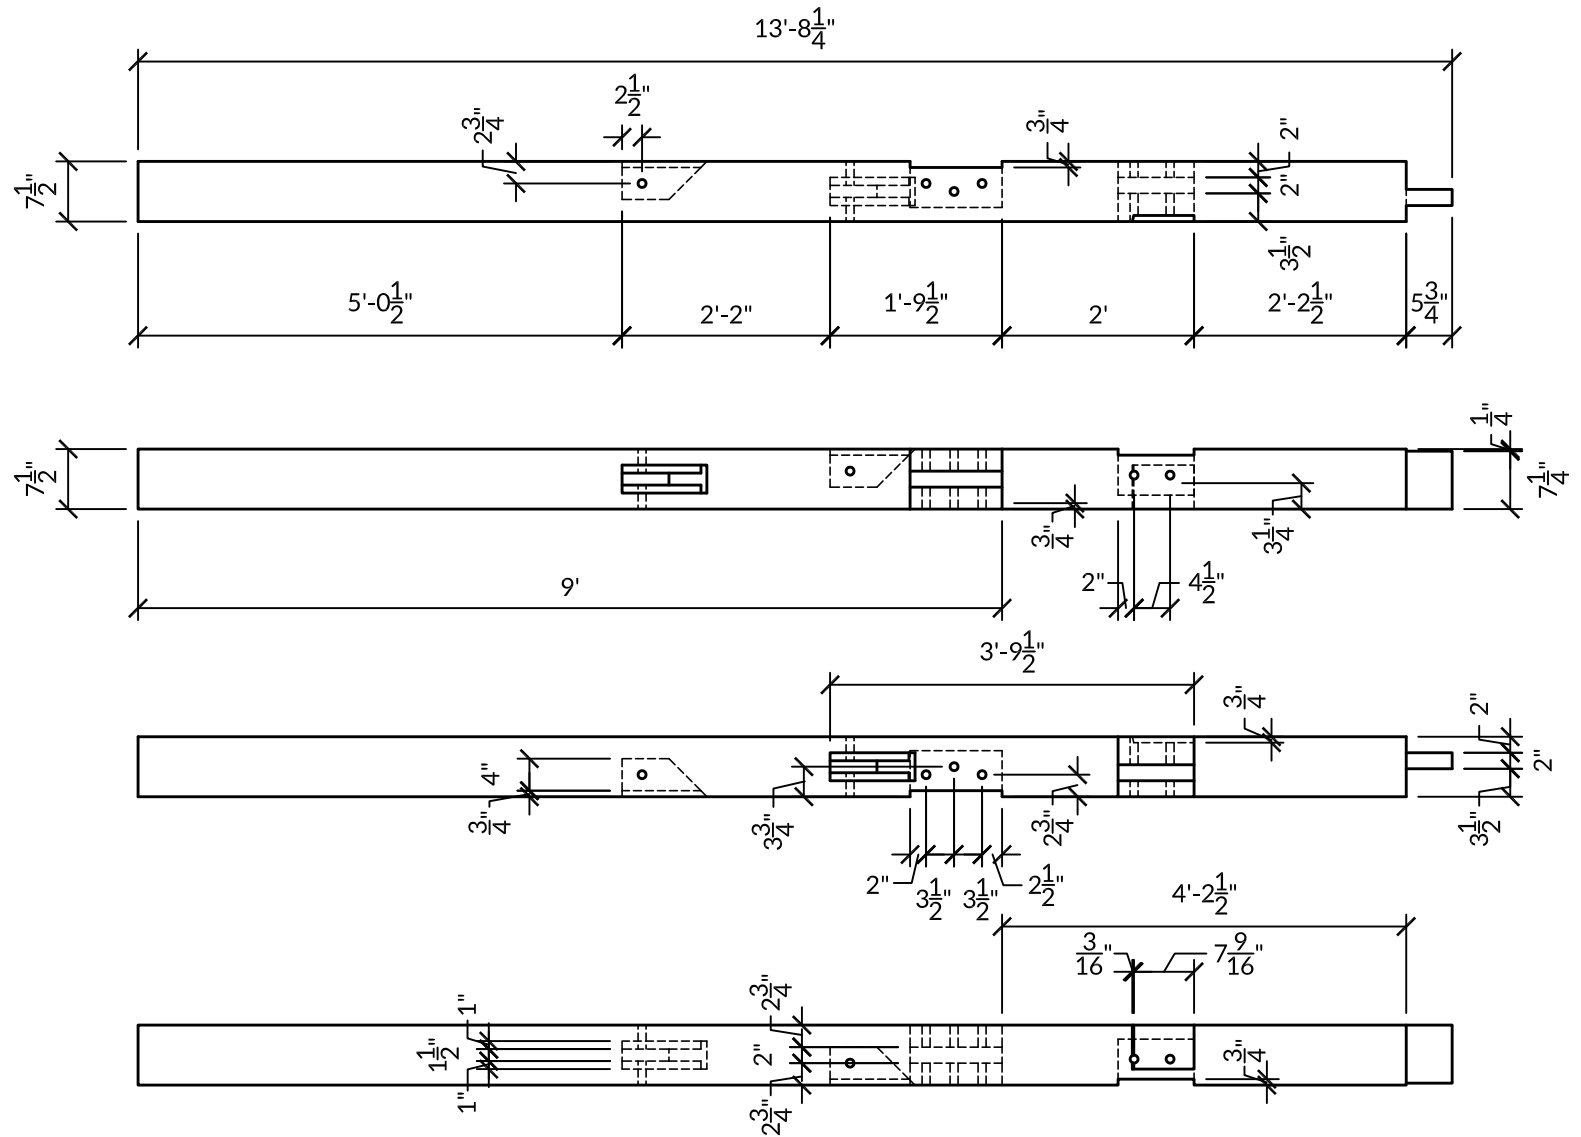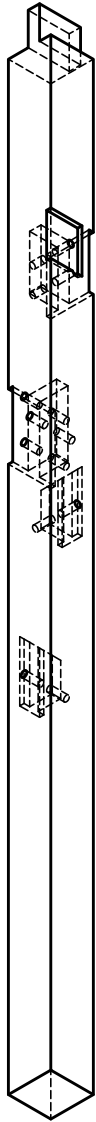



Grid Line 3B Post
Qty: 1

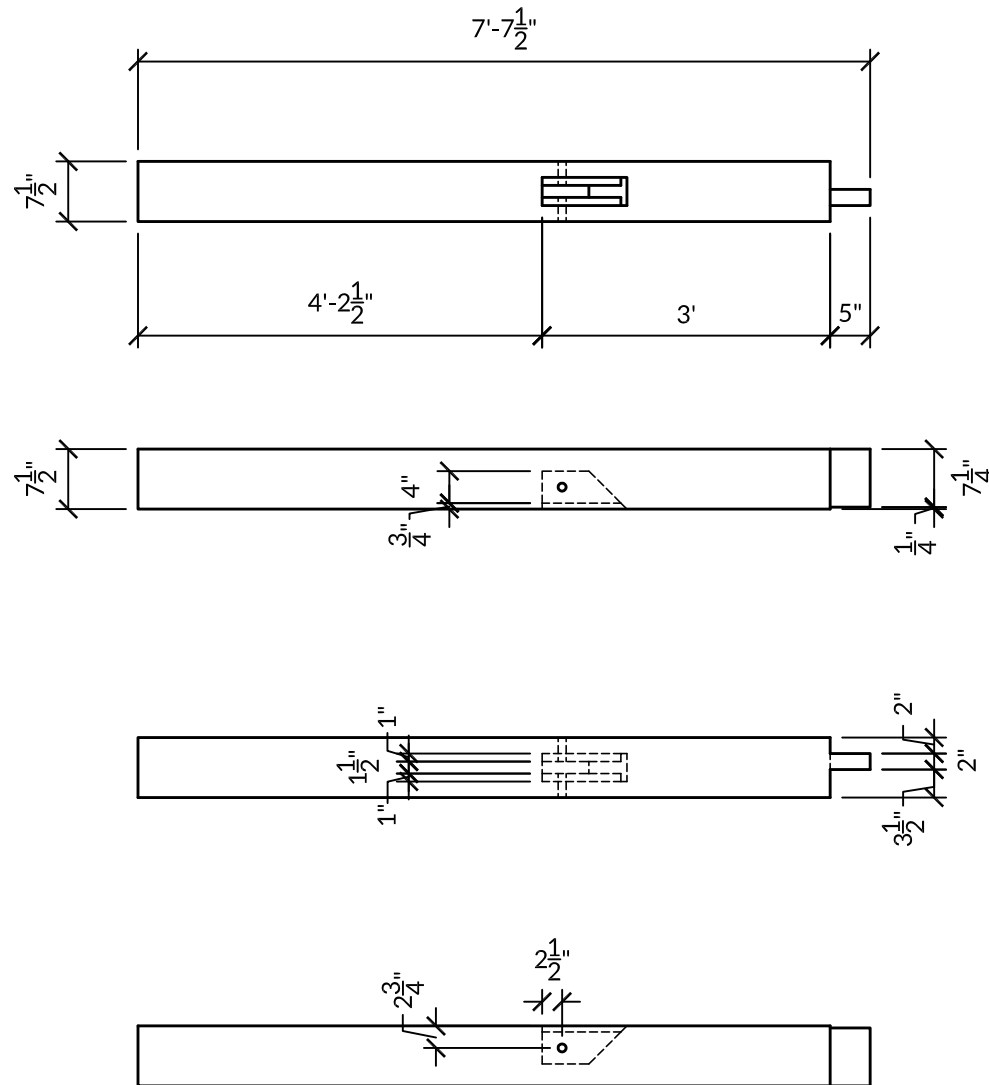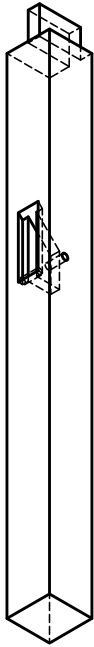



Grid Line 3A Post
Qty: 1

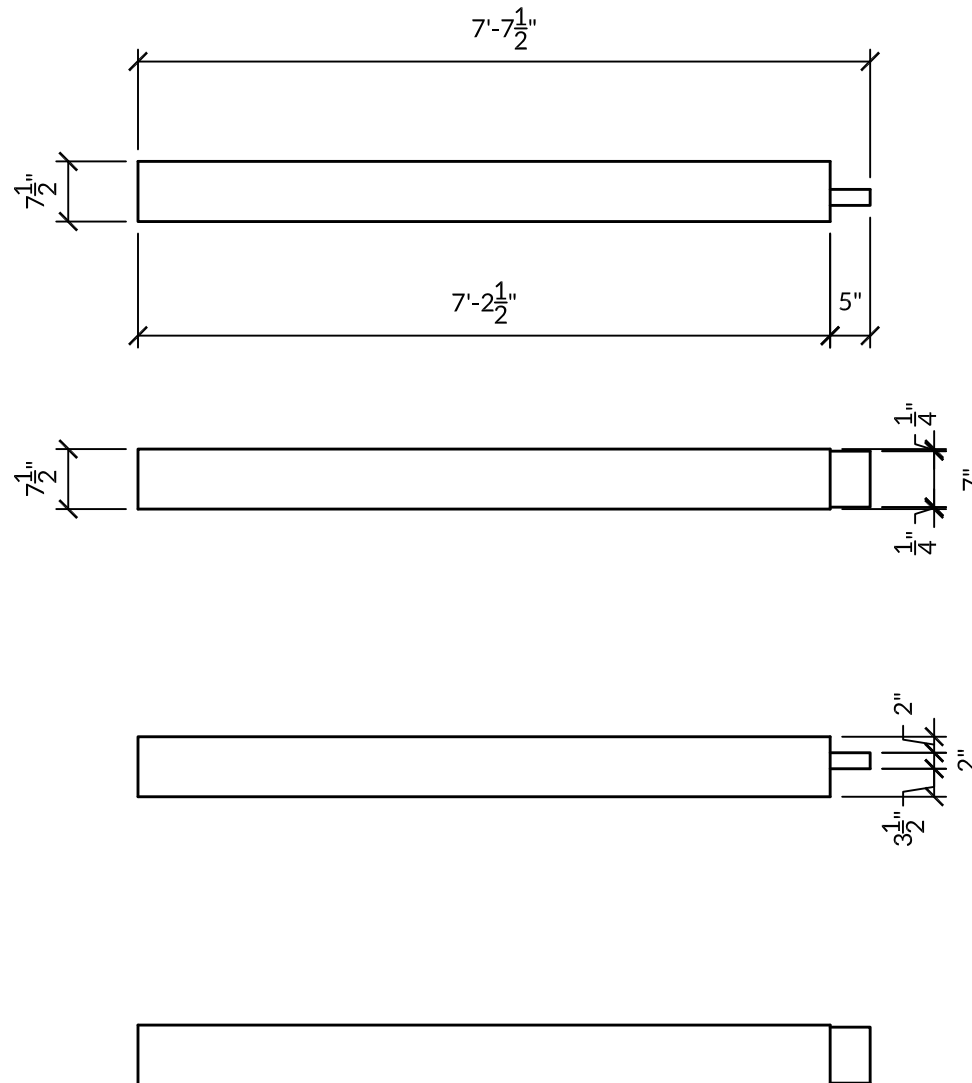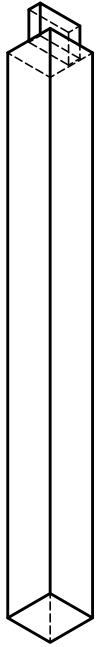



Grid Line 3B Post
Qty: 1

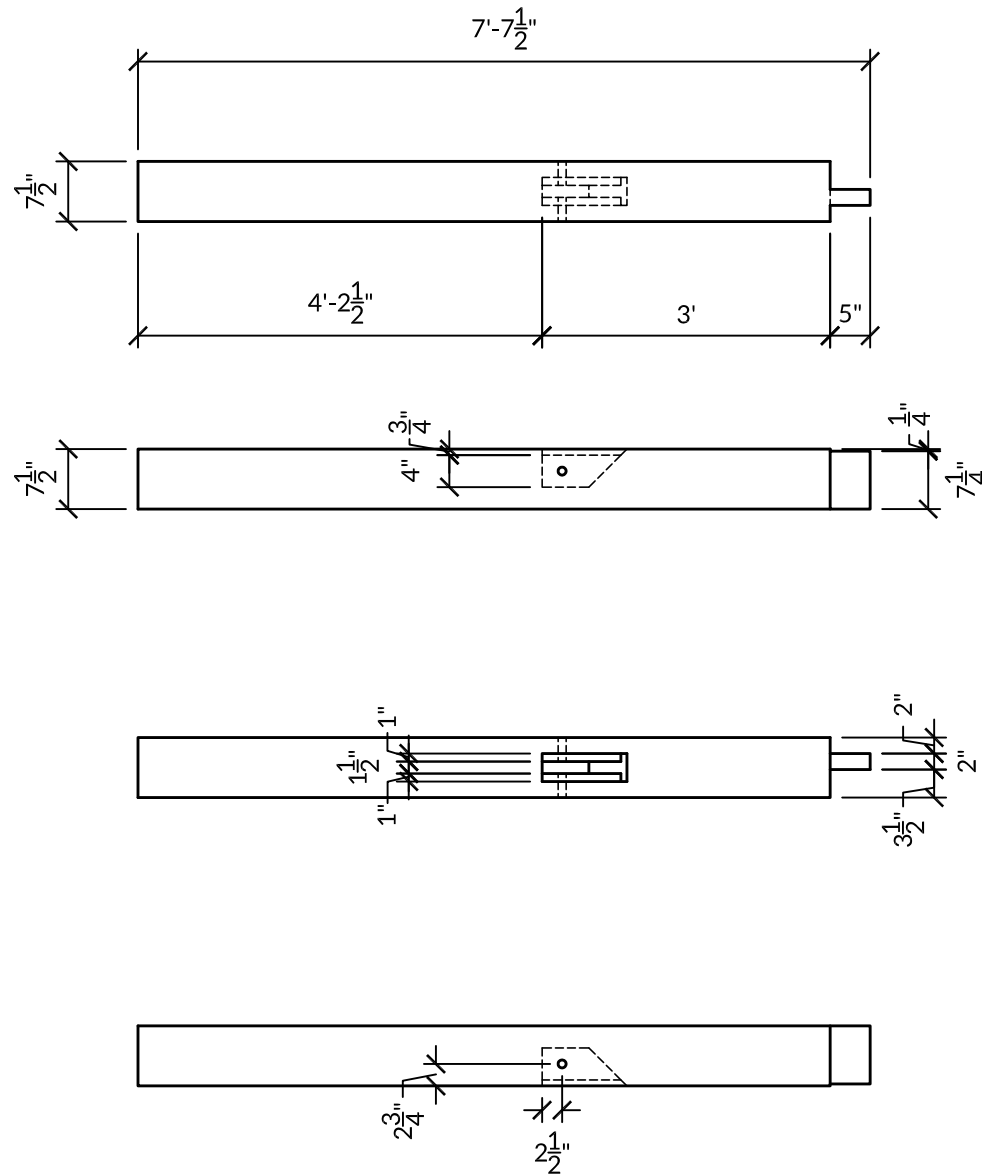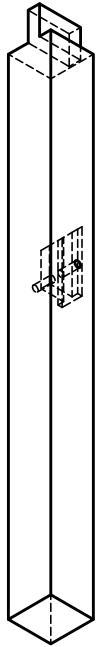



Grid Line 3C Post
Qty: 1

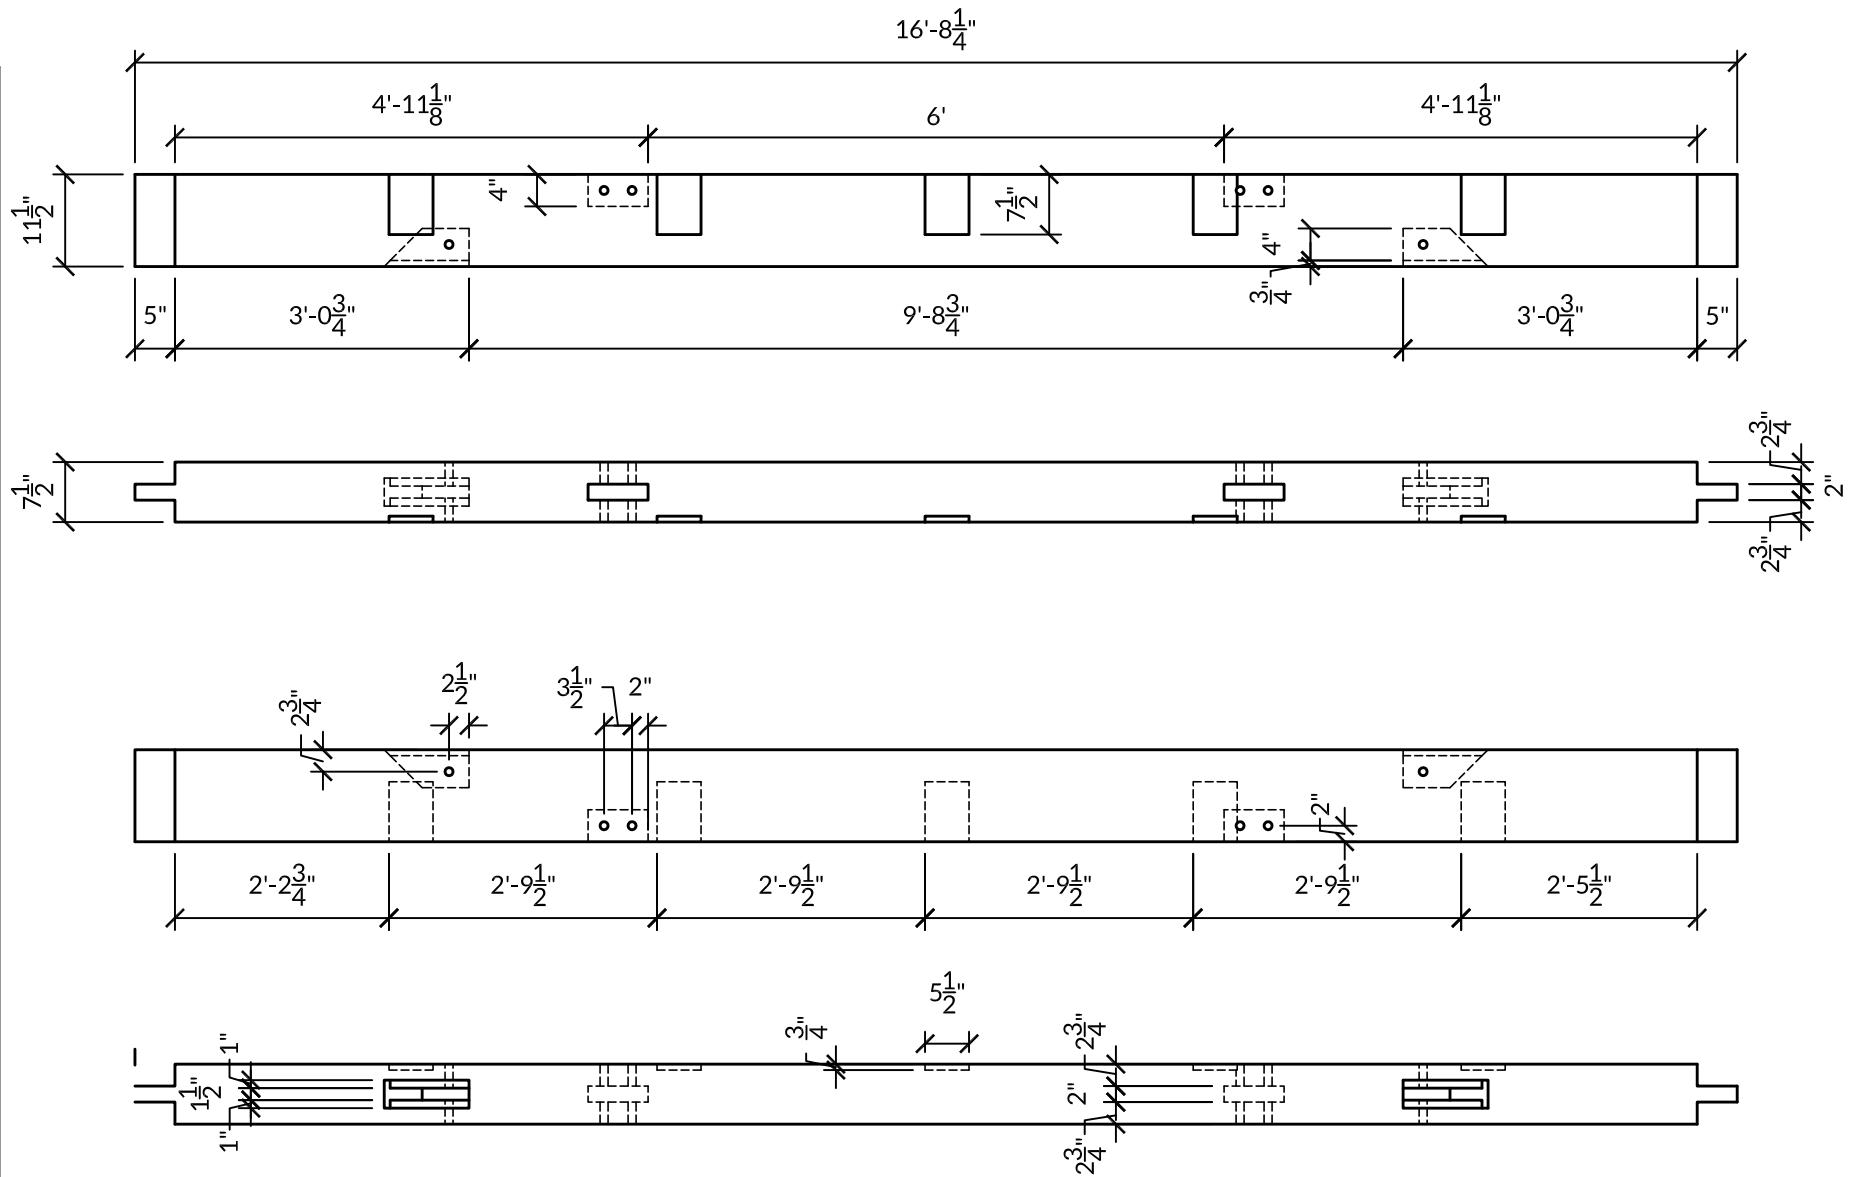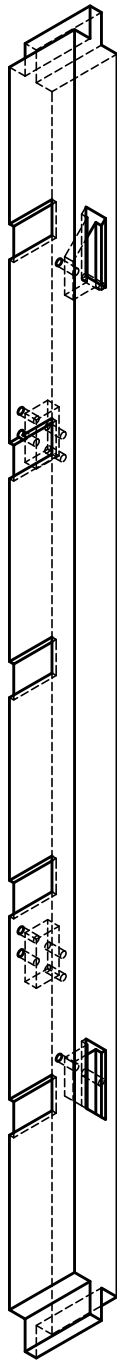



Grid Line 1 Girt Beam
Qty: 1

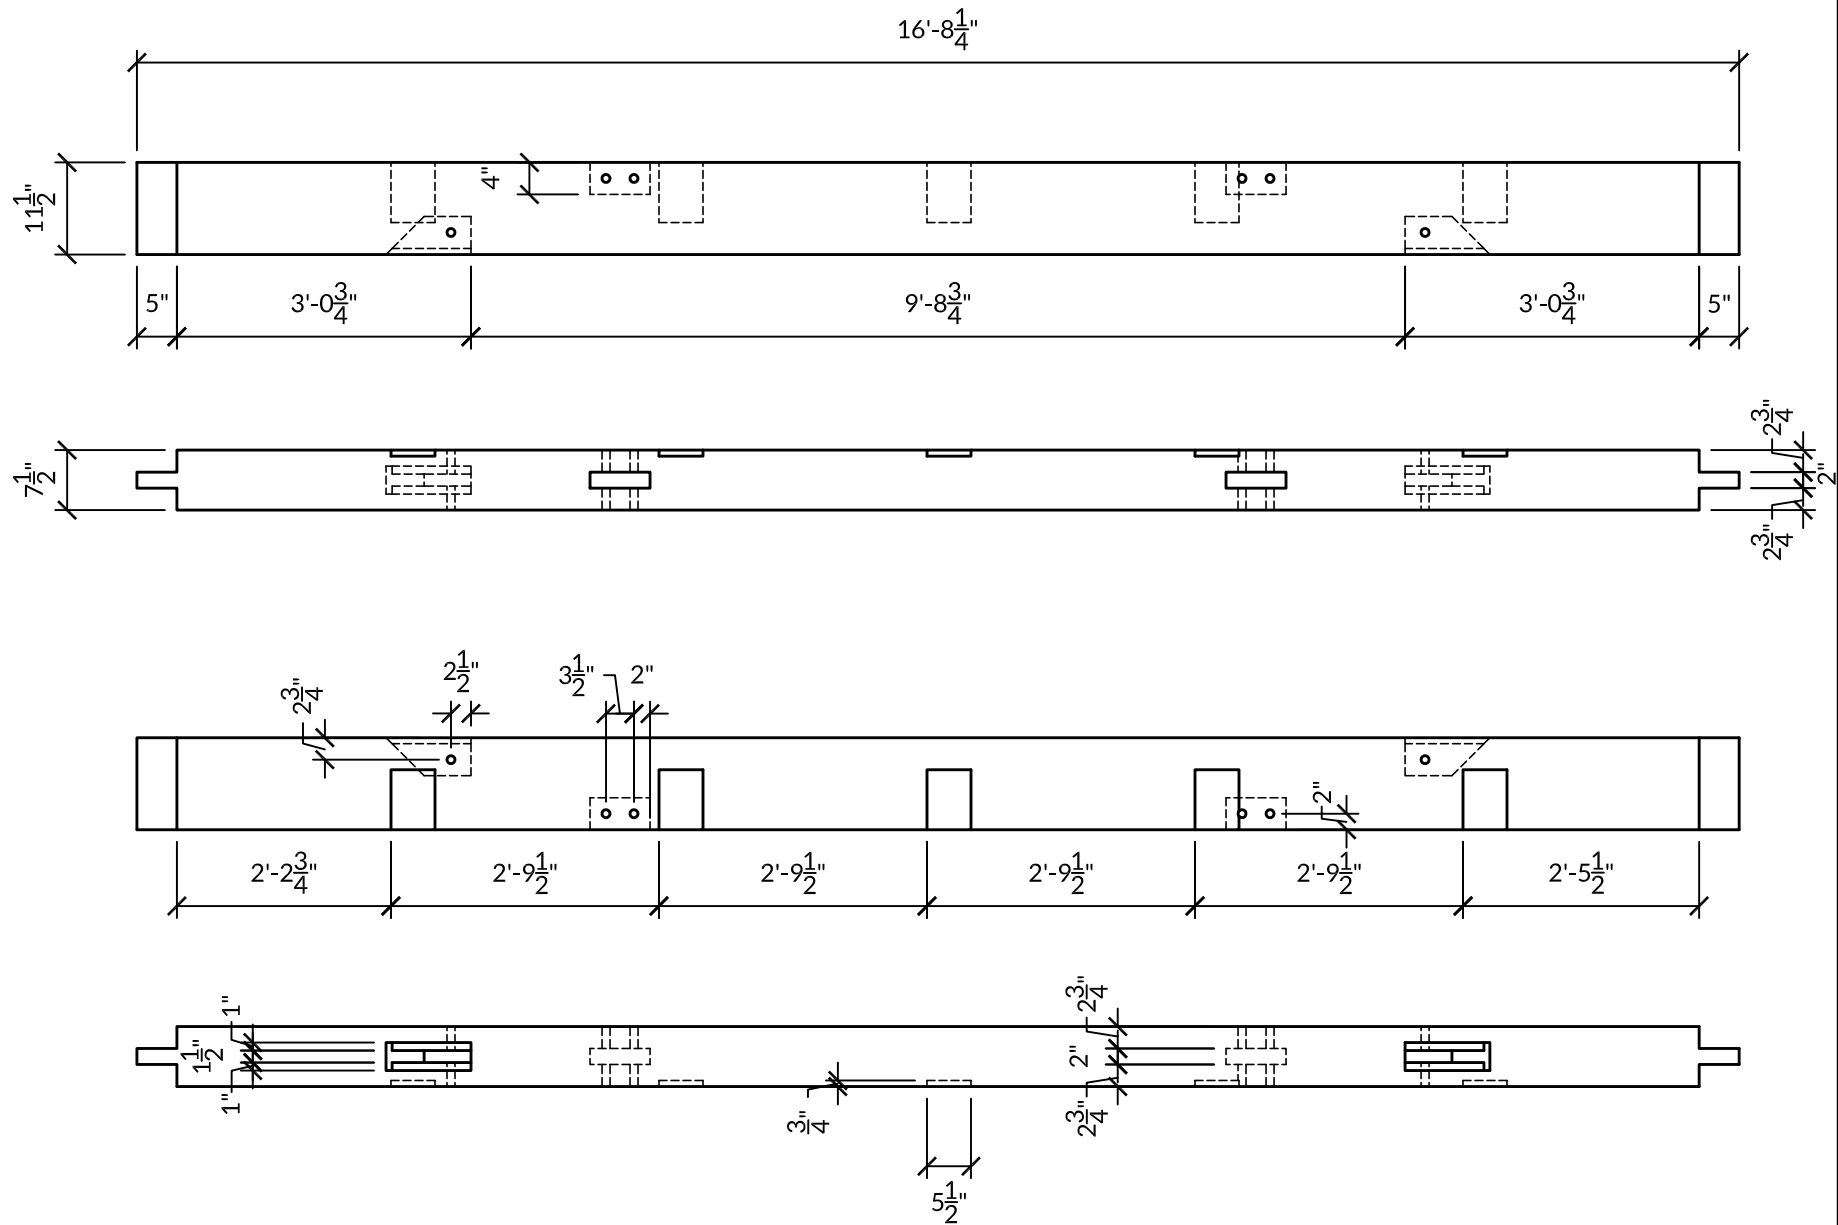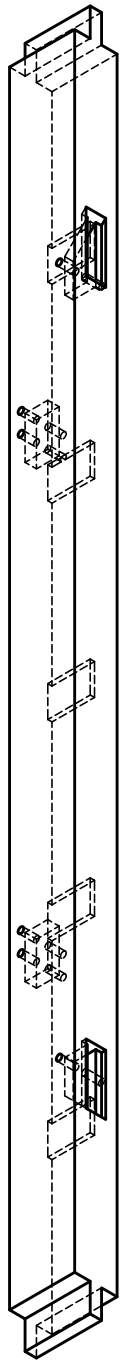






Grid Line 2 Girt Beam
Qty: 1

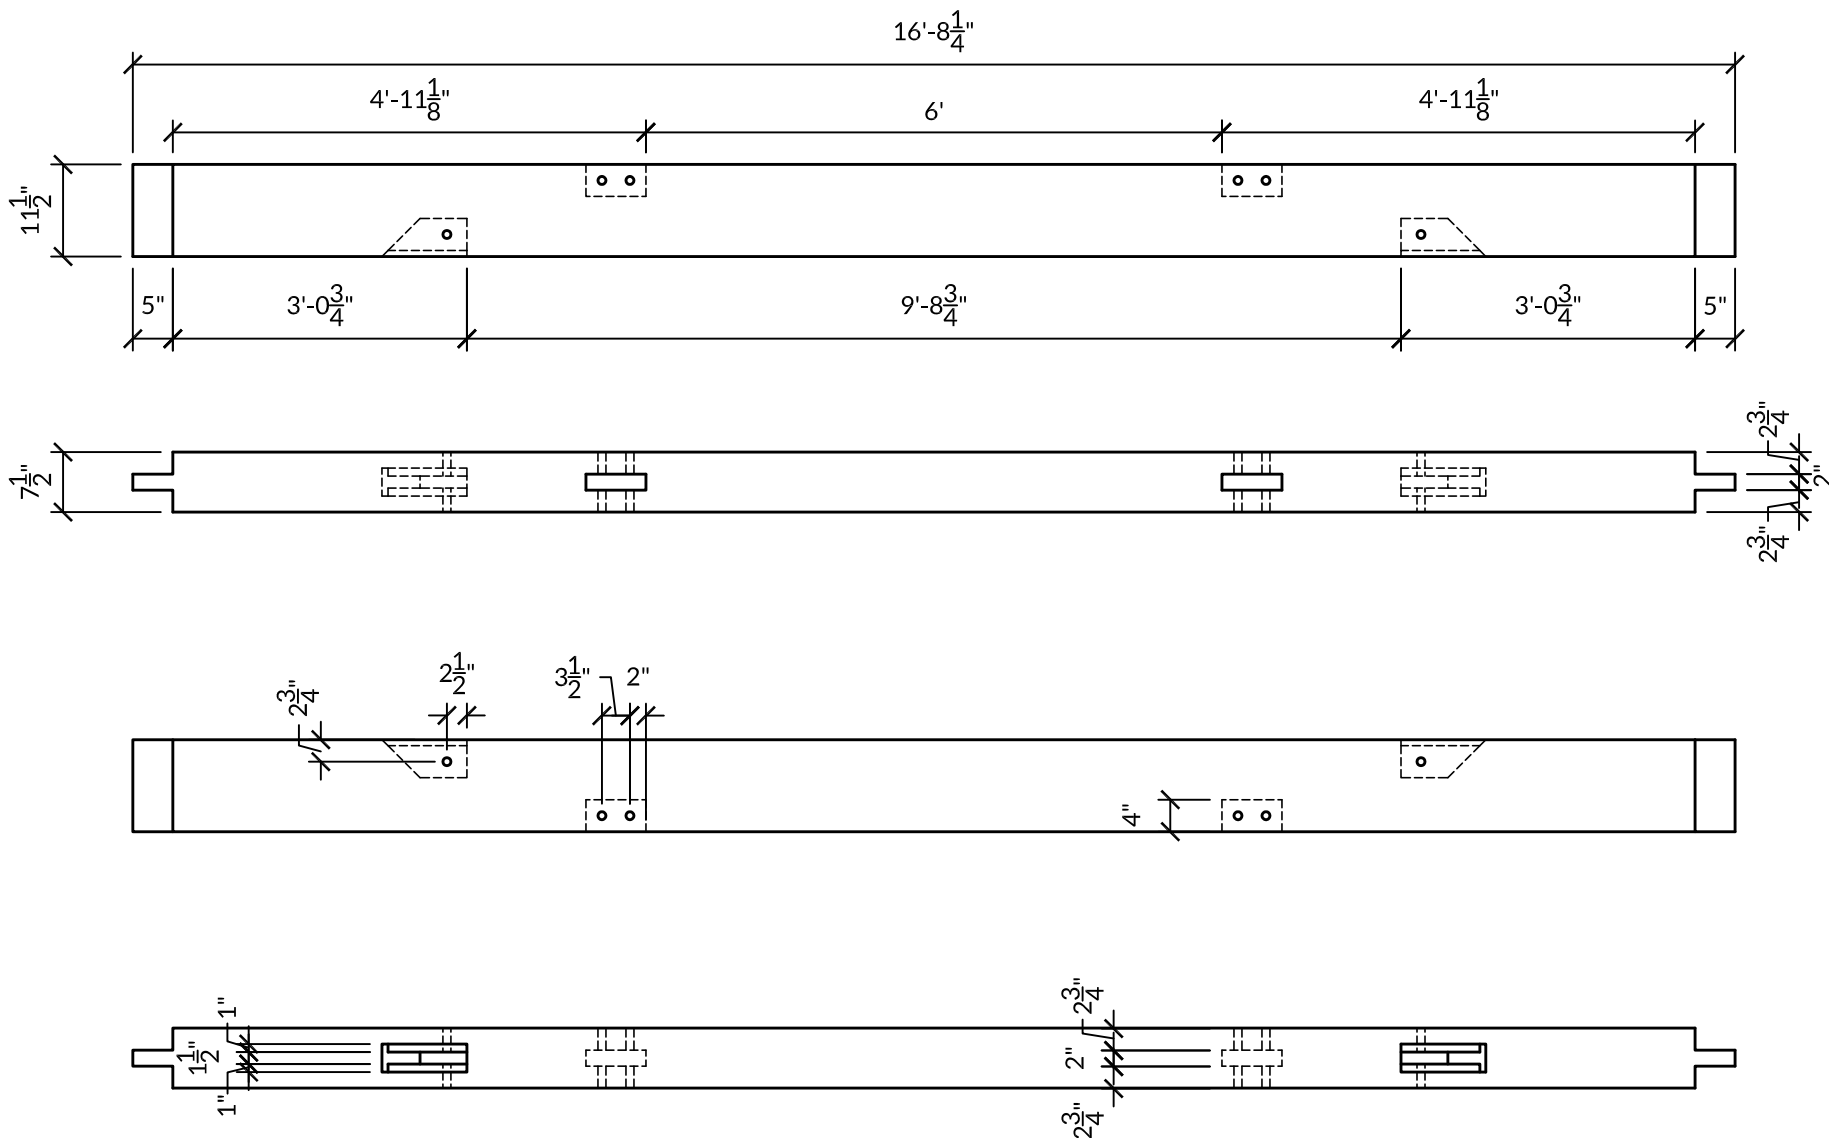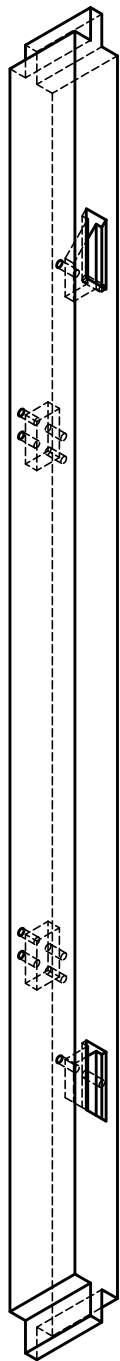



Grid Line 3 Girt Beam
Qty: 1

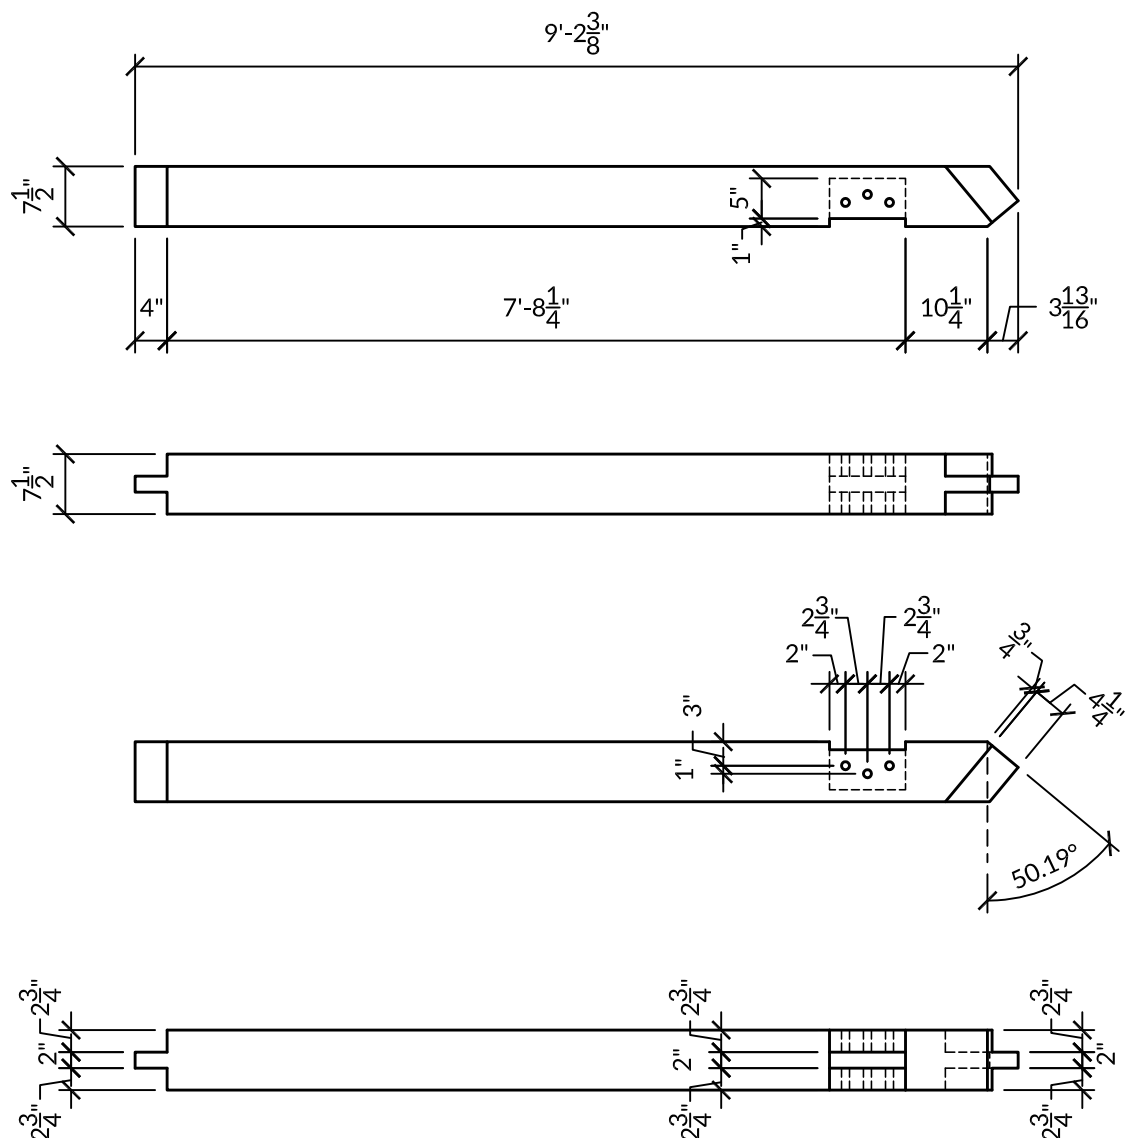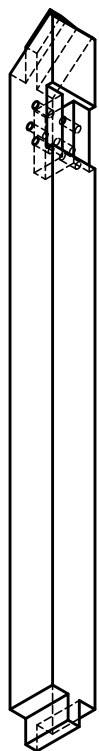



Queen Post
Qty: 6 - (3) Mirrored

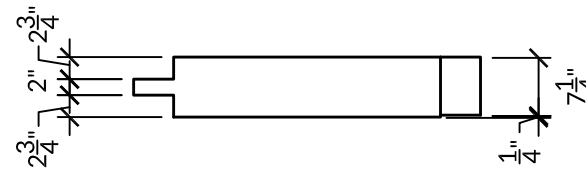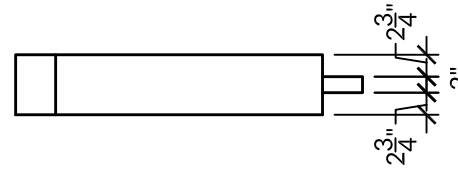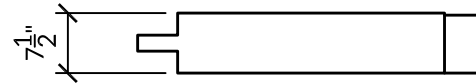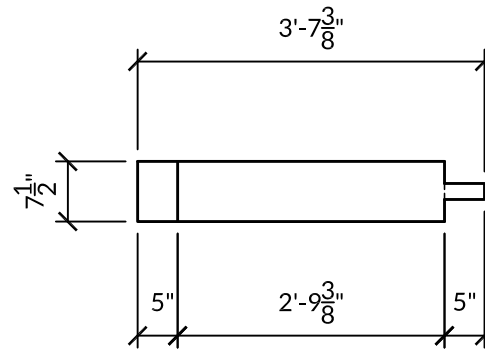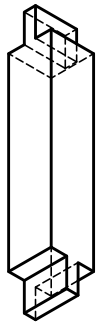


King Post
Qty: 3

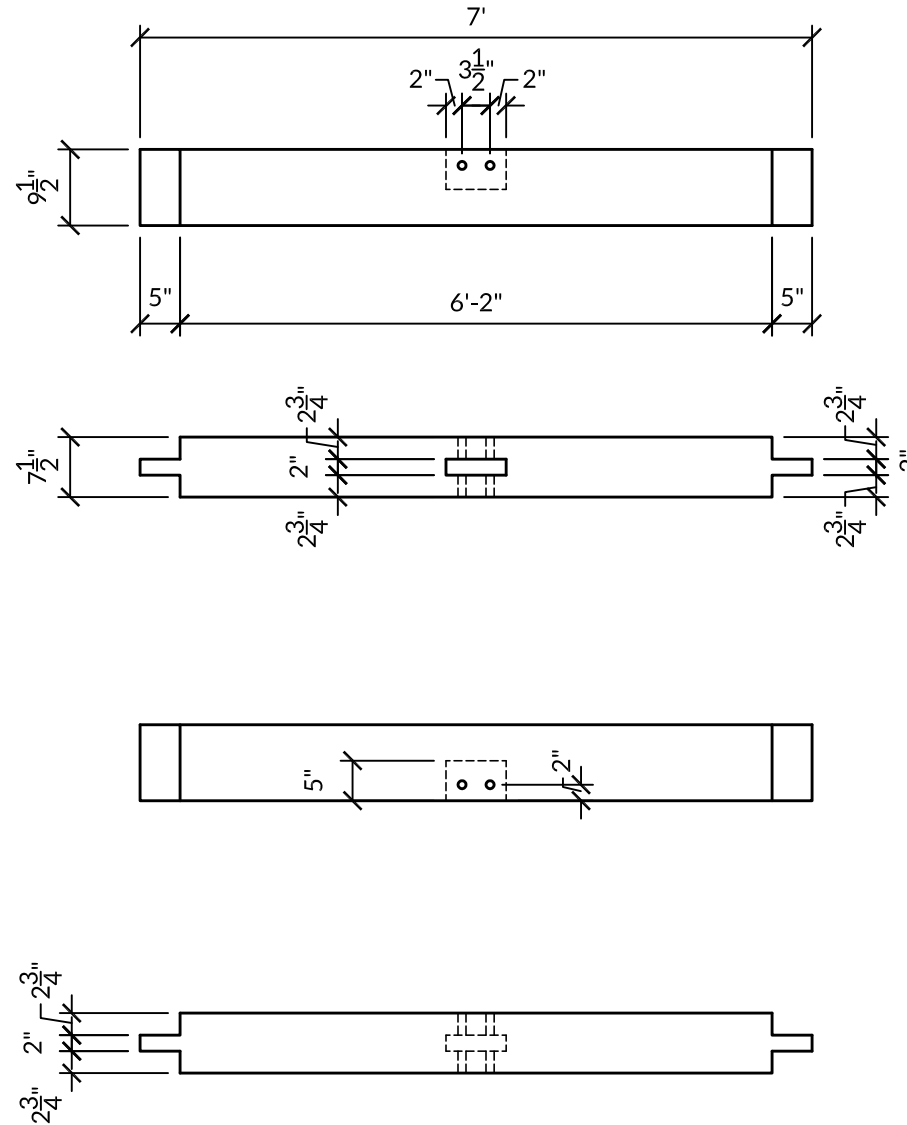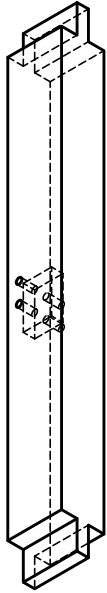

Tie Beam
Qty: 3

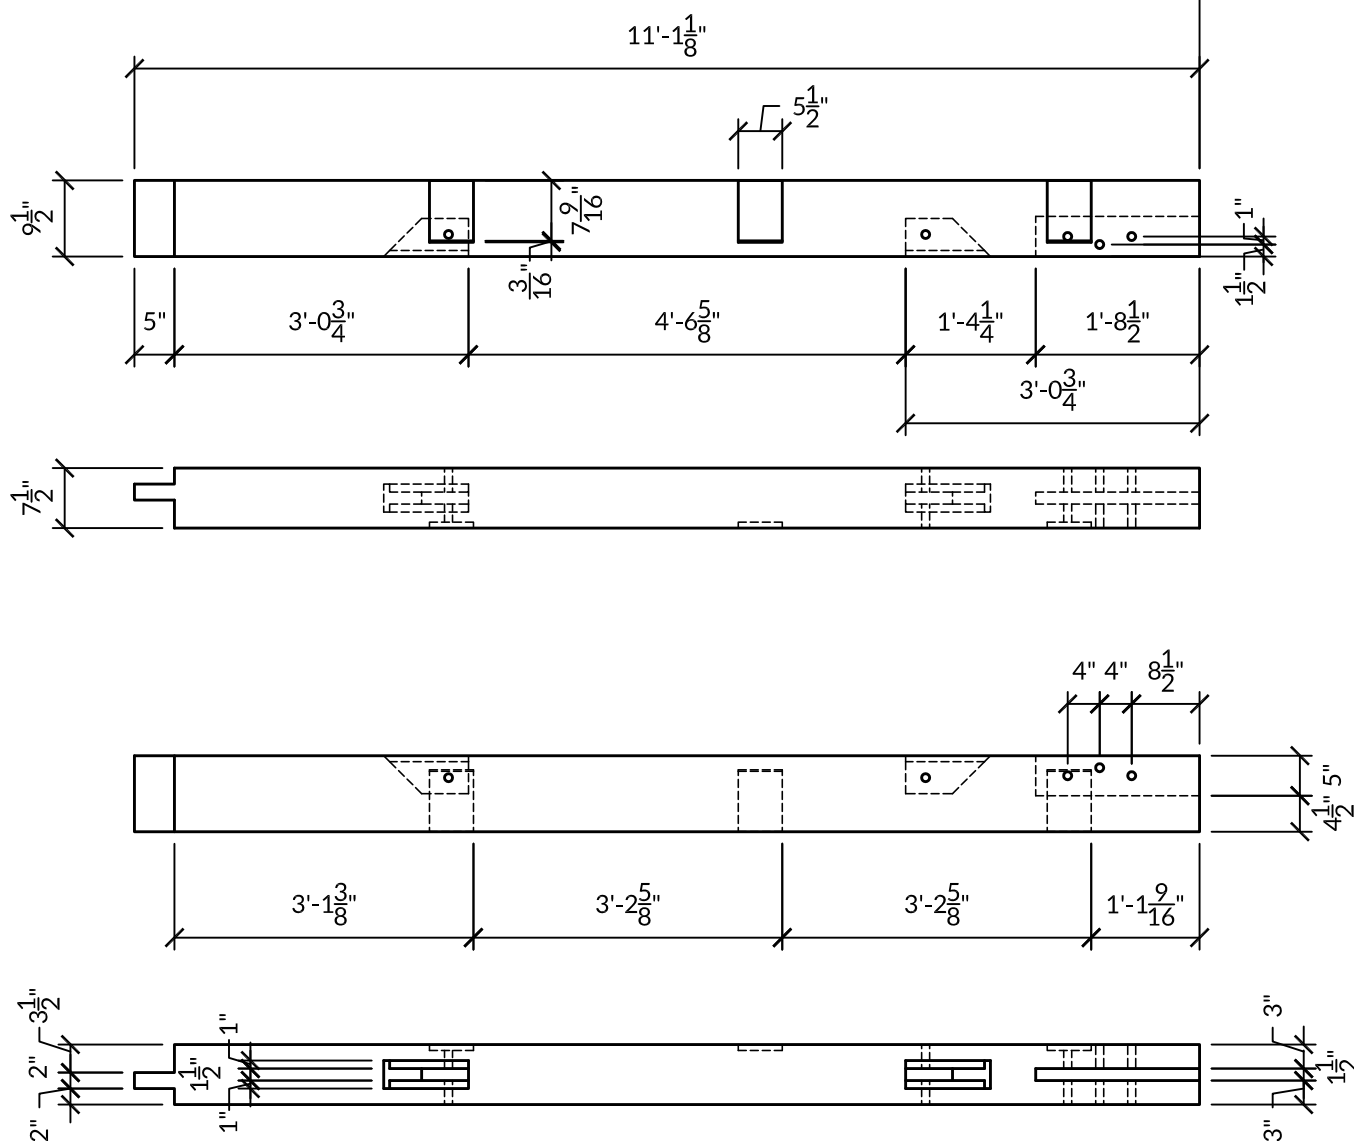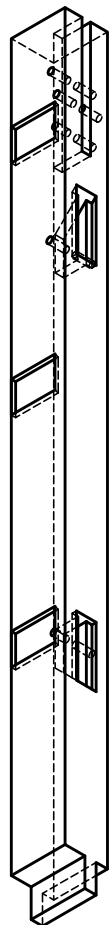

Shed Header 1-2
Qty: 1

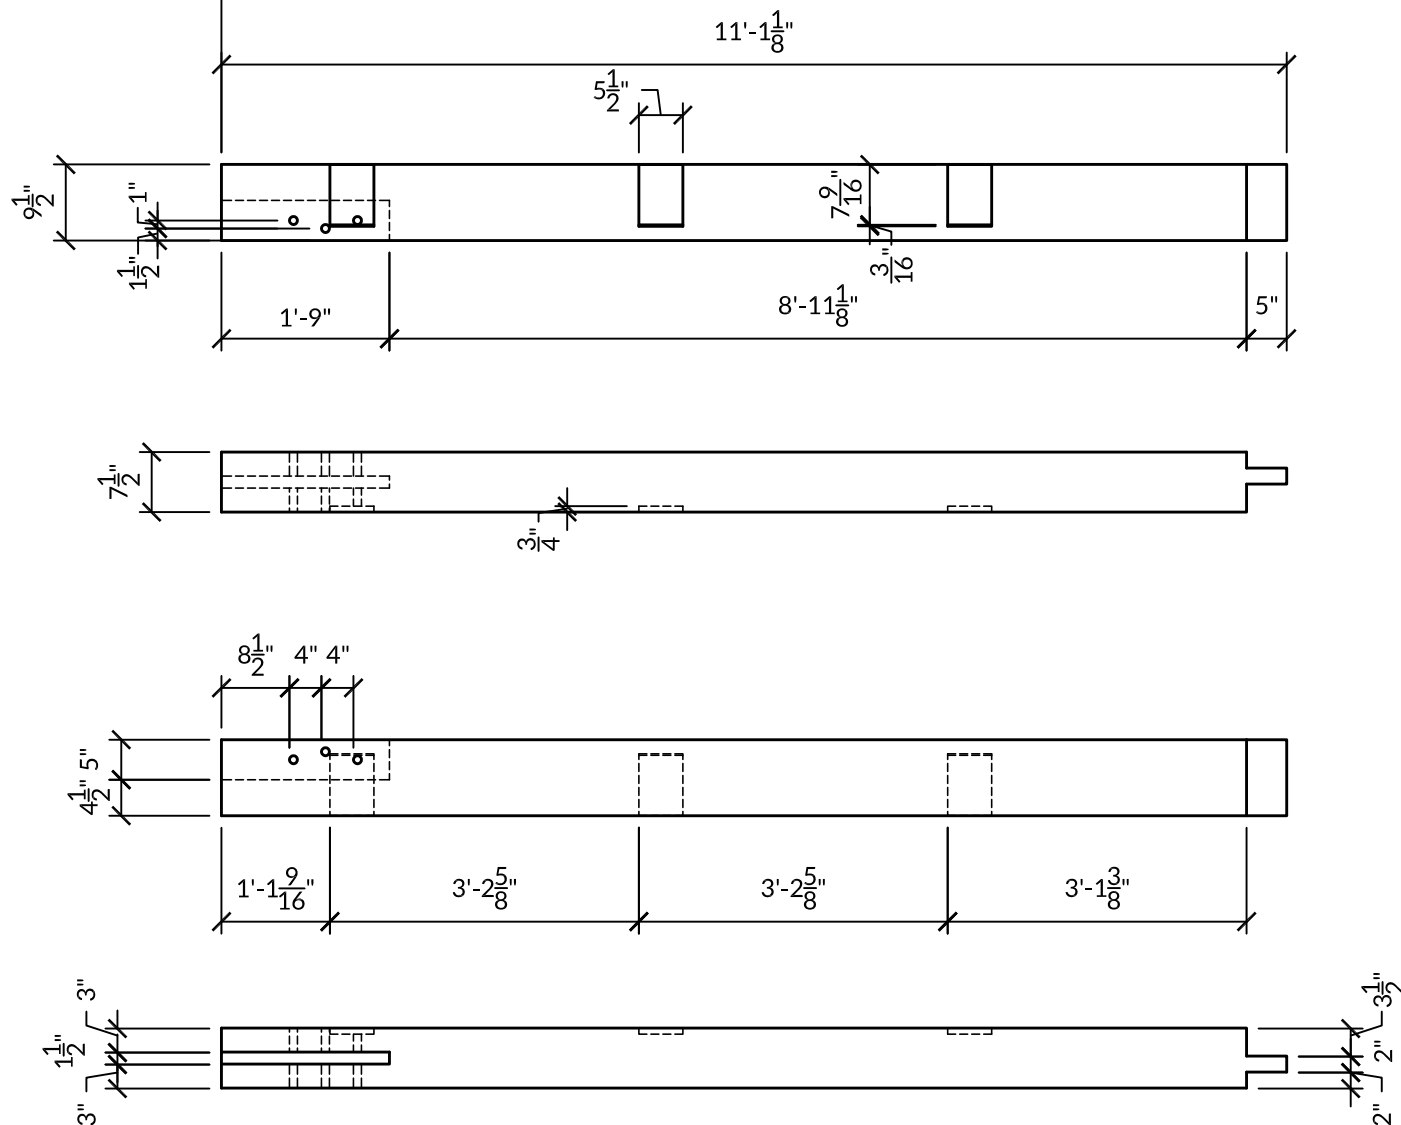

Qty: 1

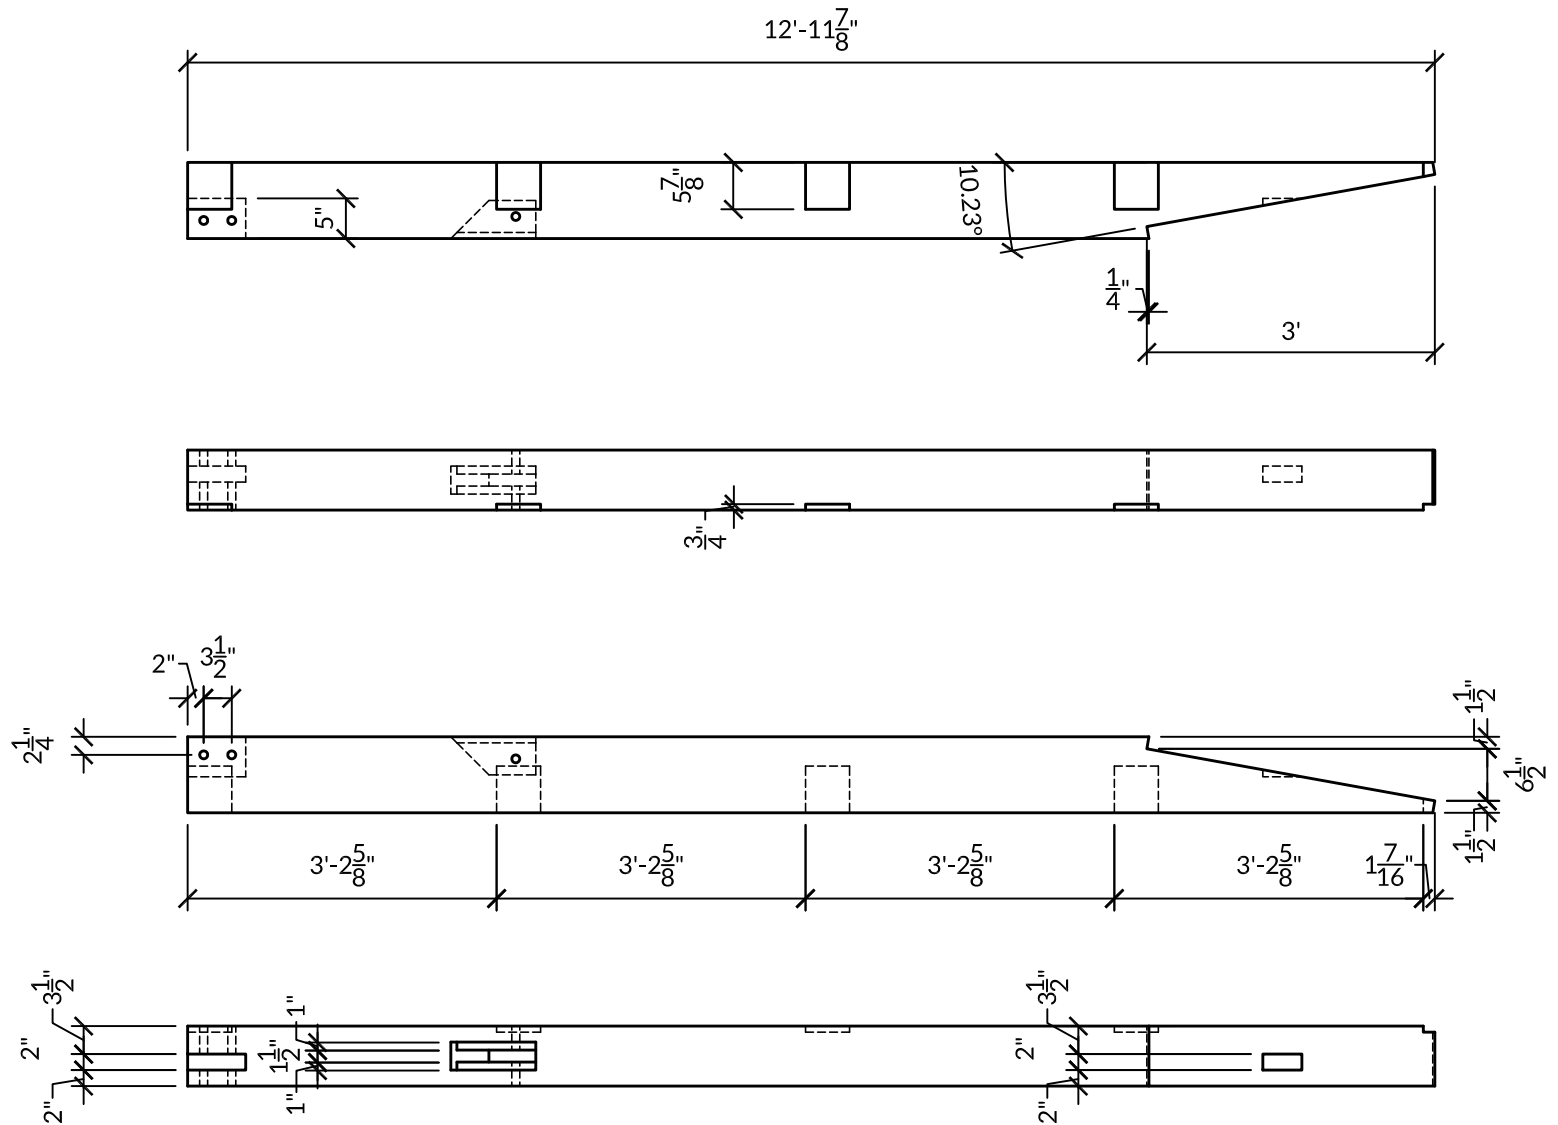
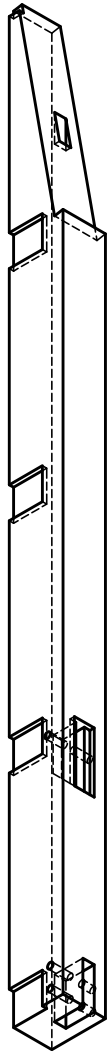


Plate A/1-2
Qty: 1

Knee Brace B
Qty: 8



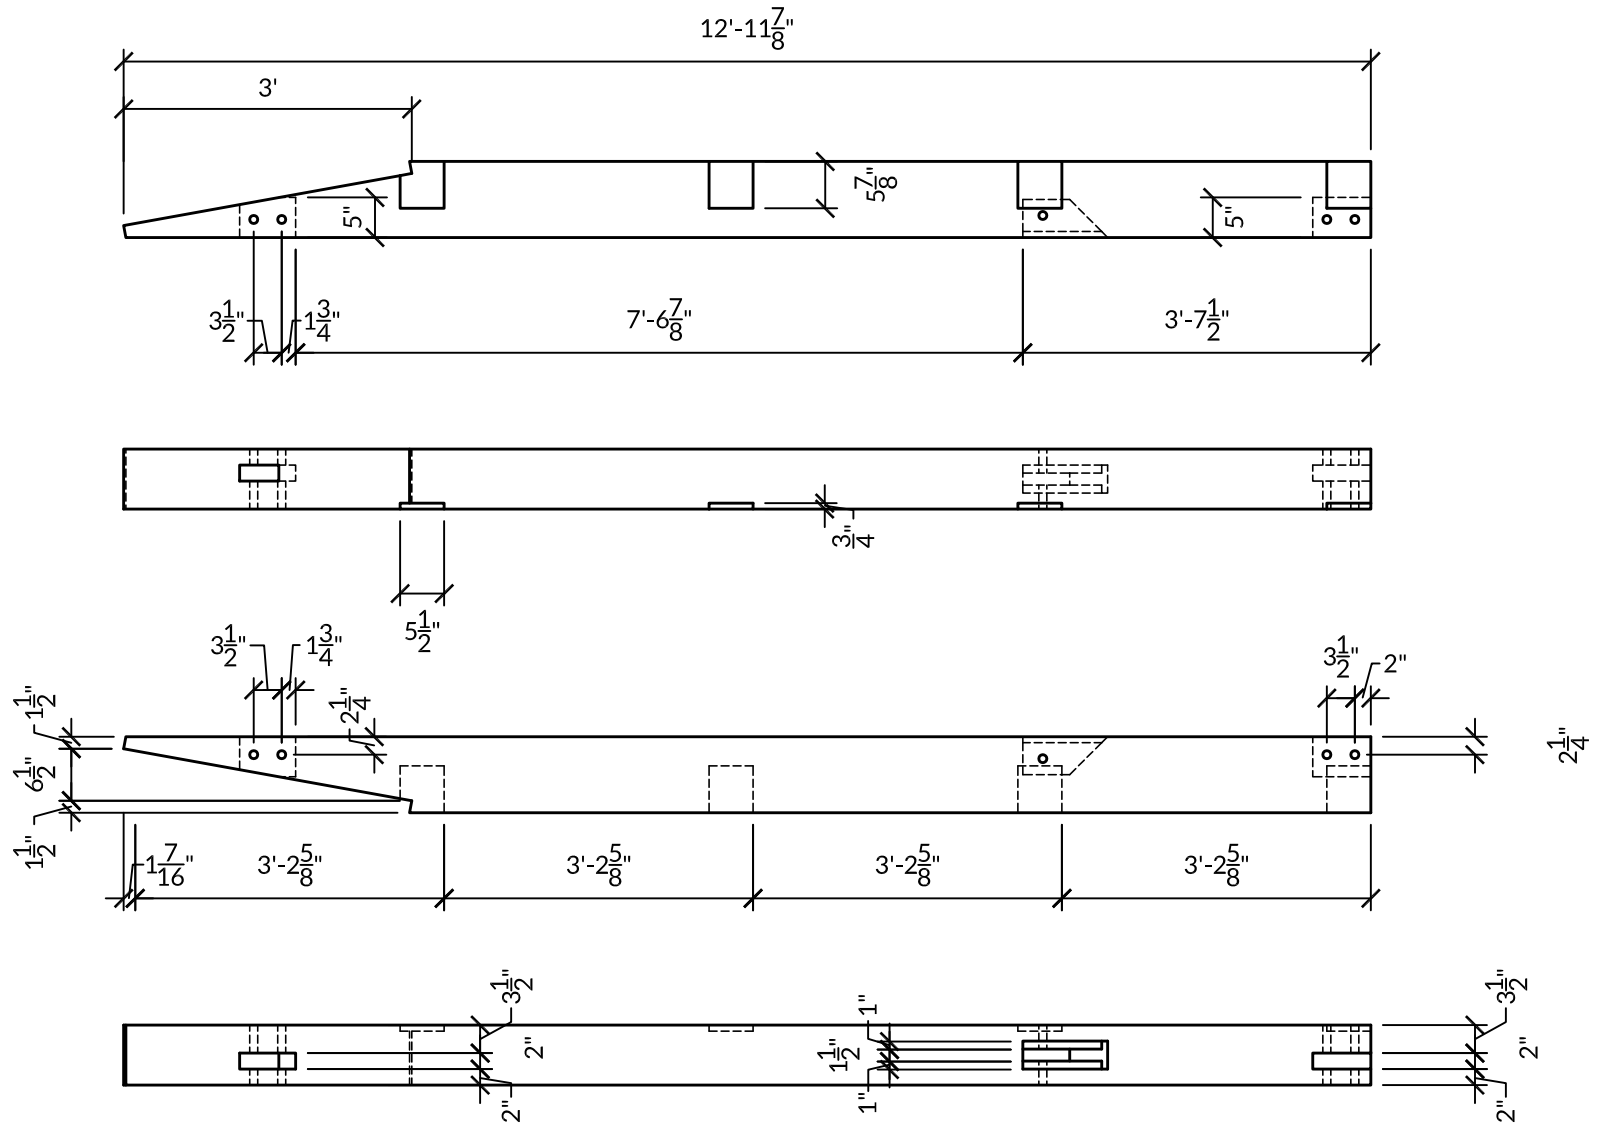


Plate A/2-3
Qty: 1

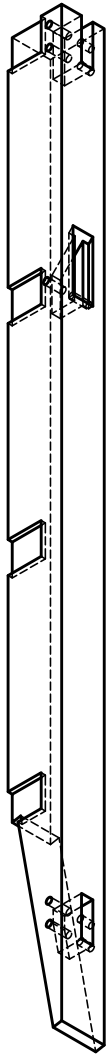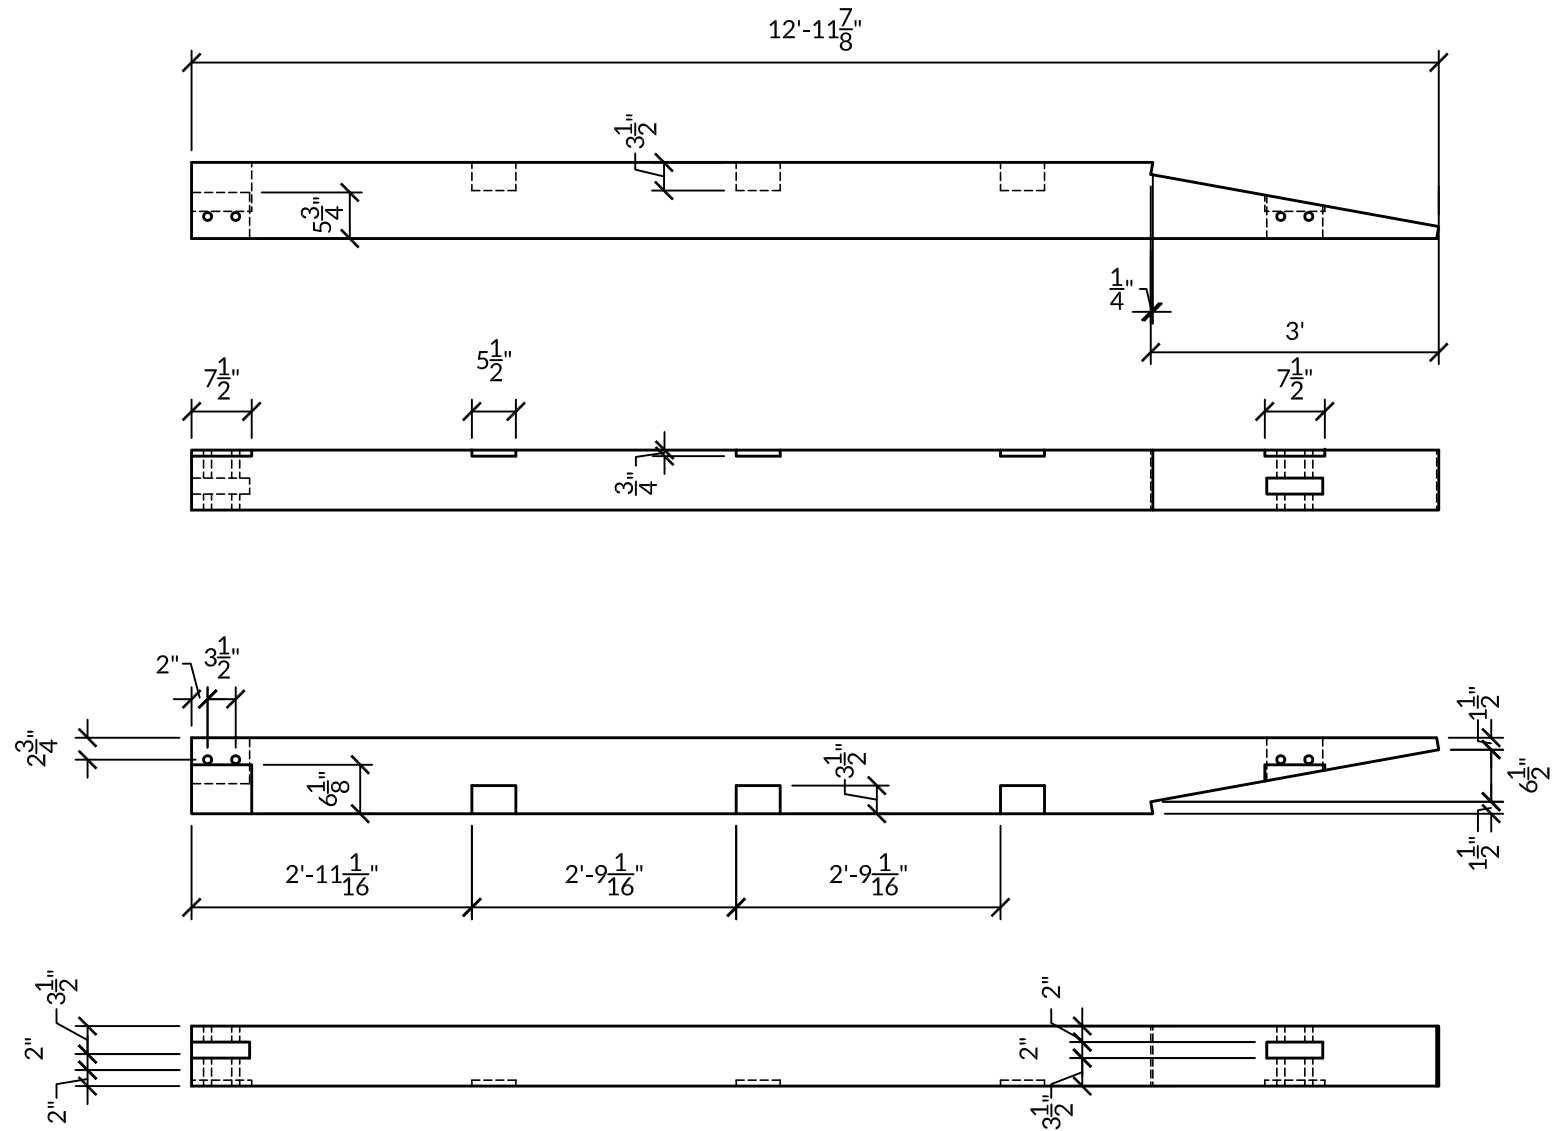

Qty: 1

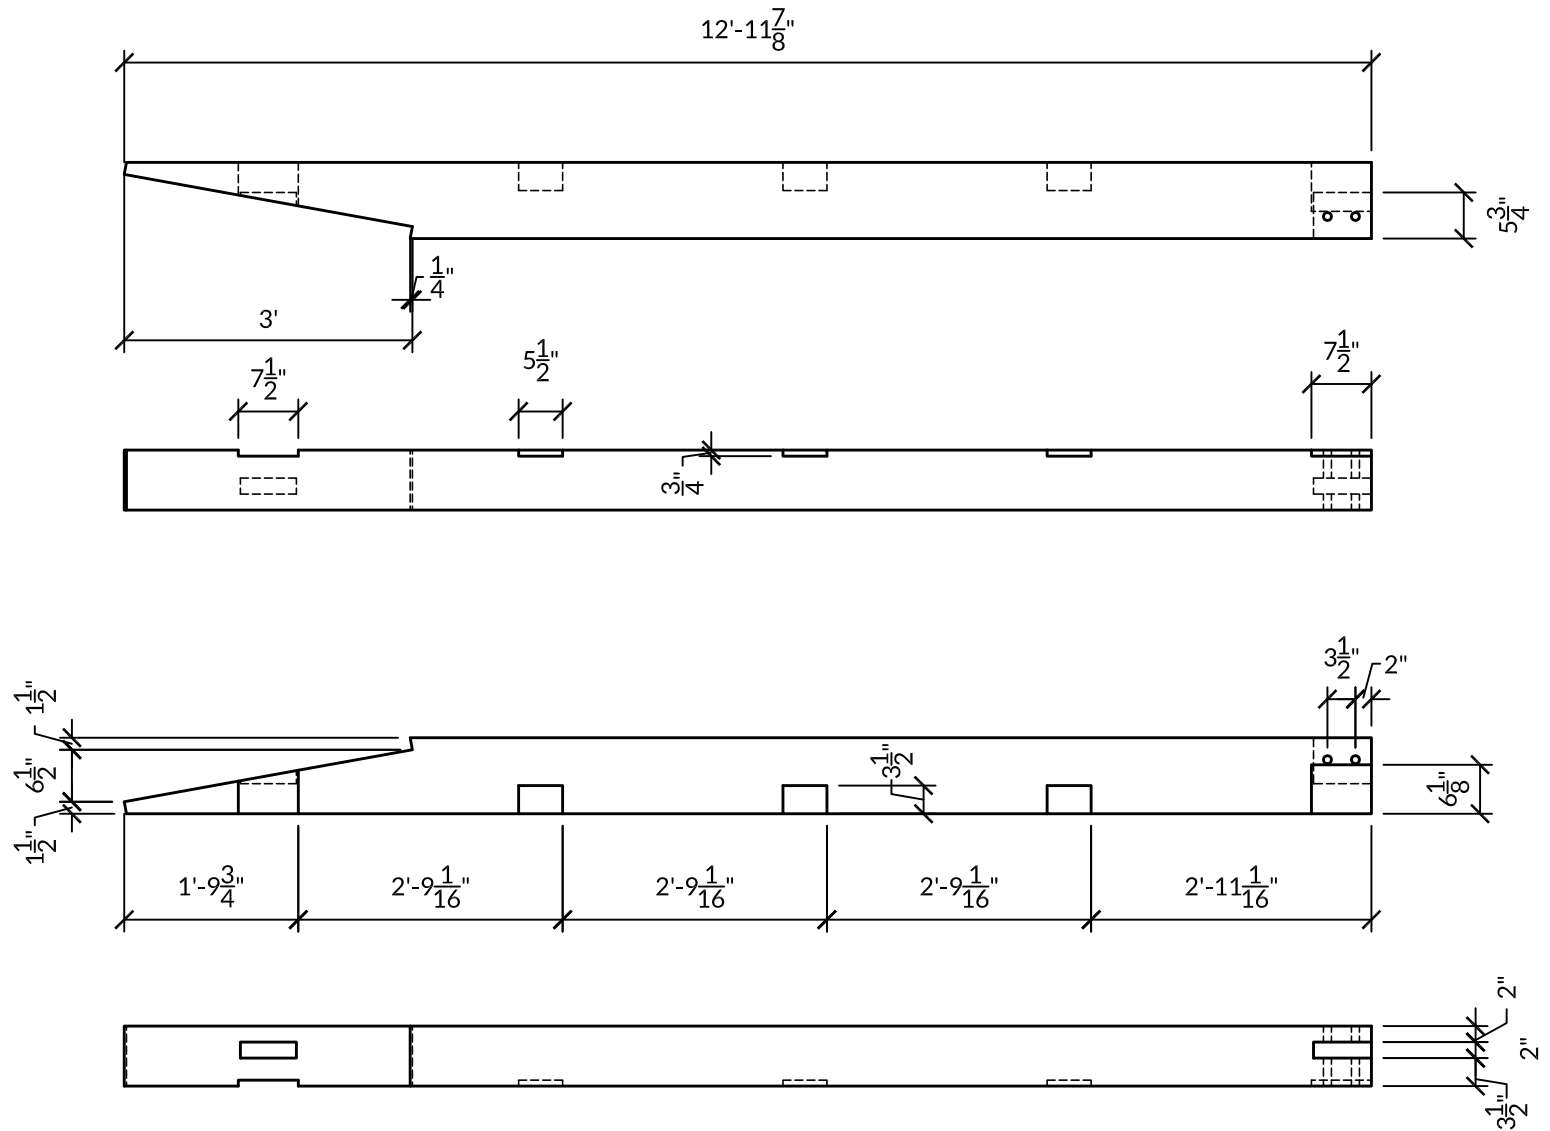
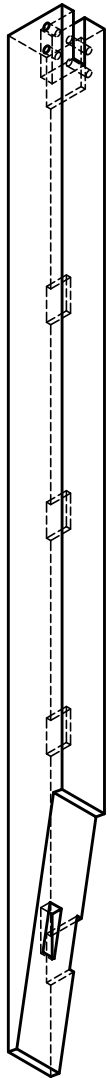


Plate B/2-3

Qty: 1

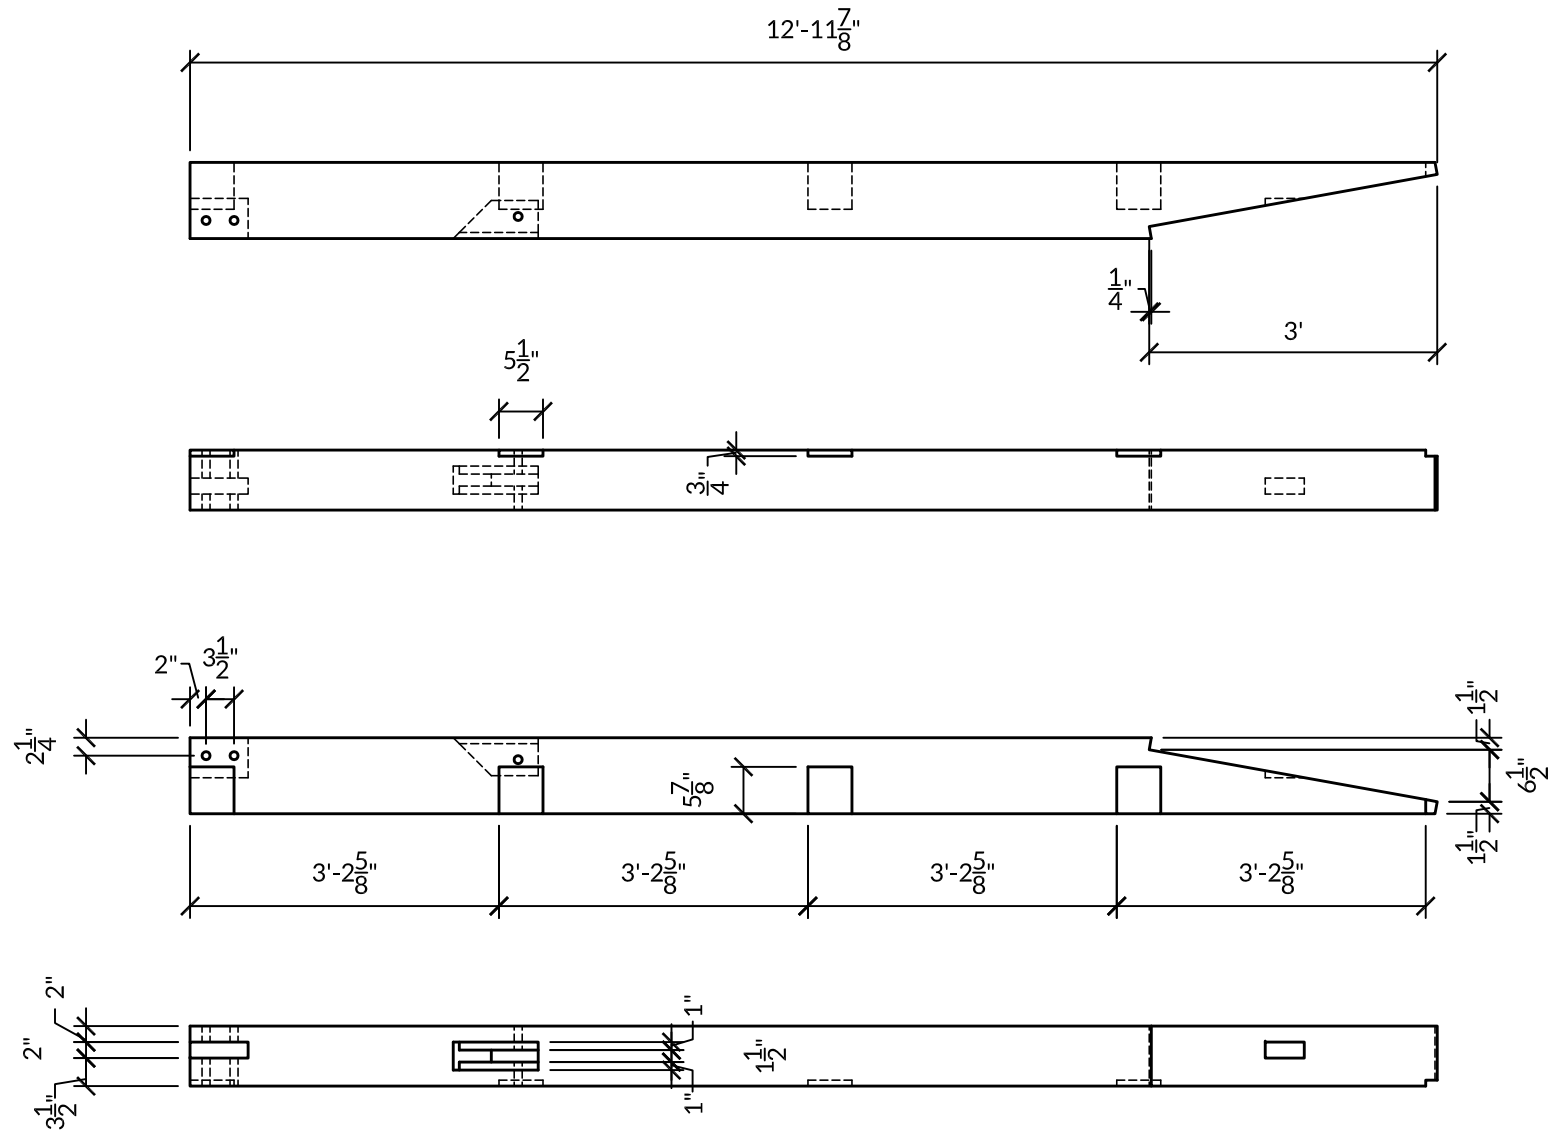
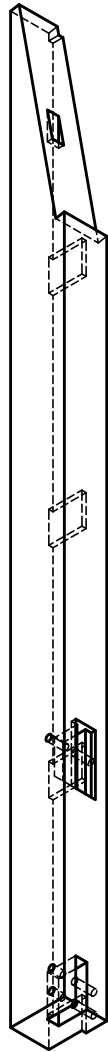


Plate C/1-2

Qty: 1




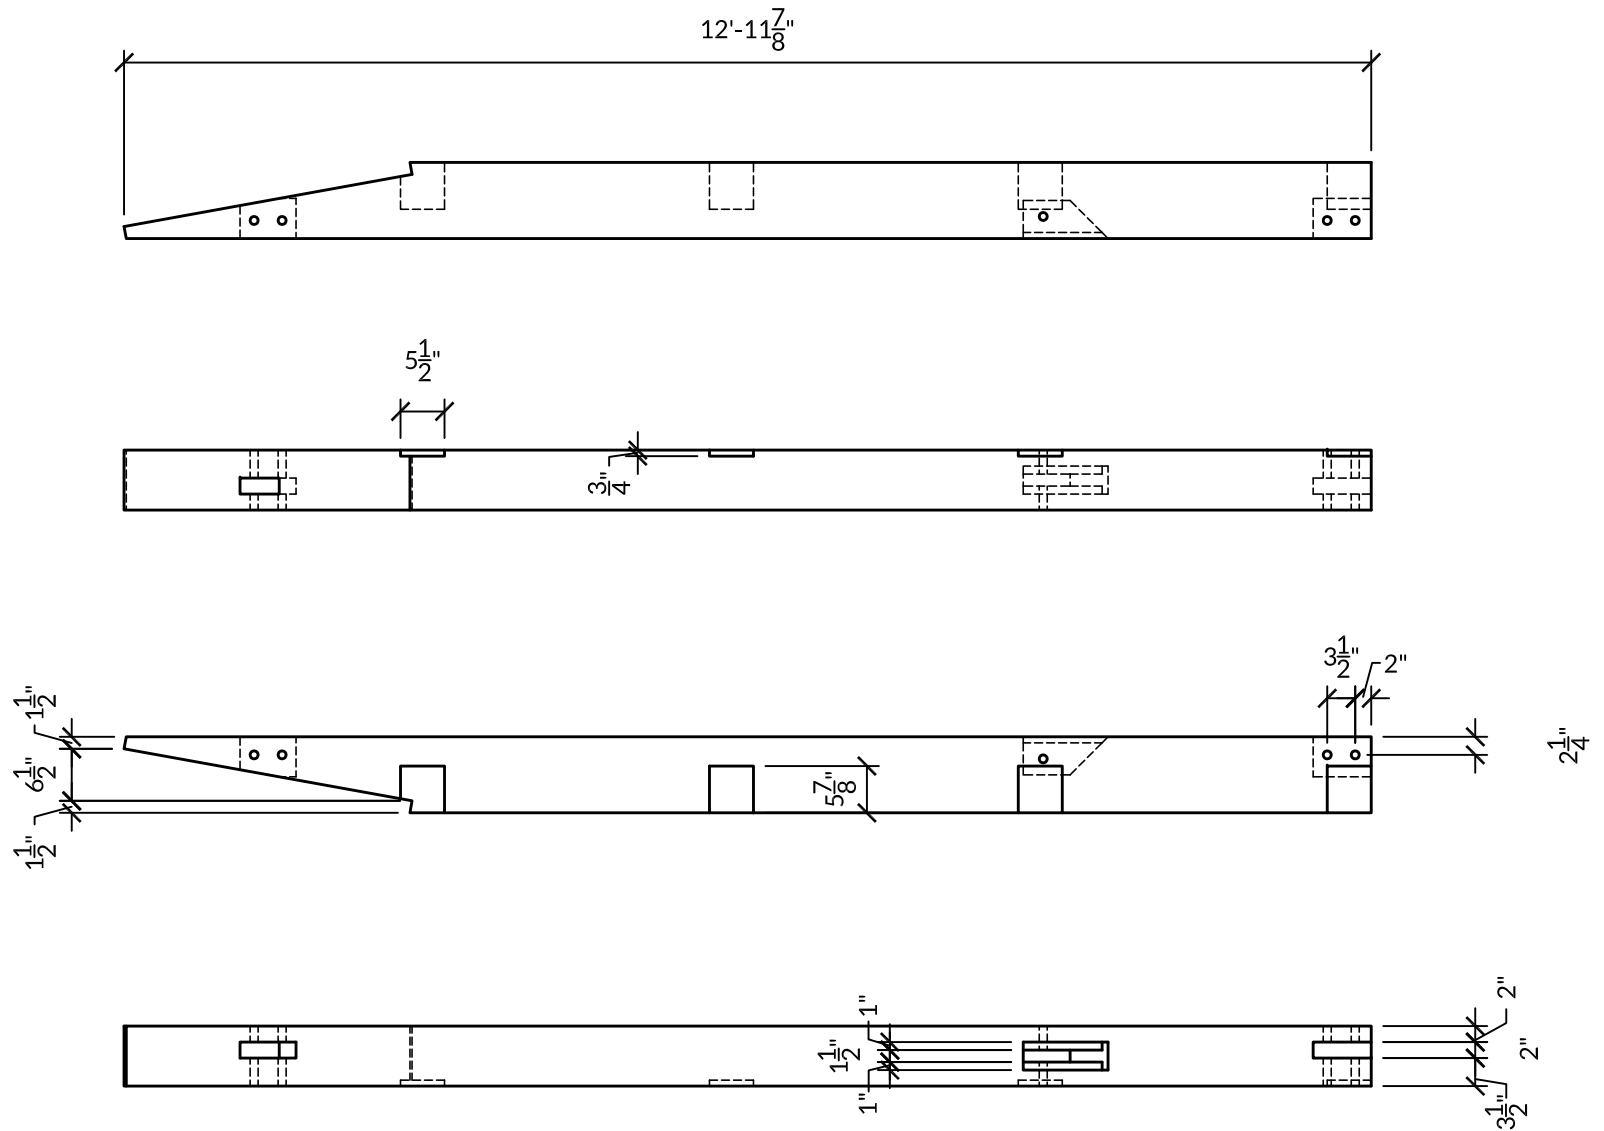



Plate C/2-3

Qty: 1


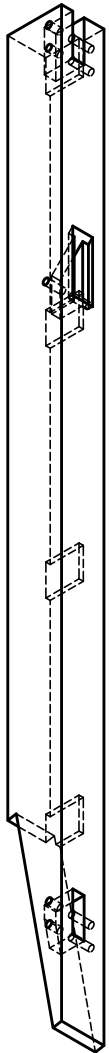
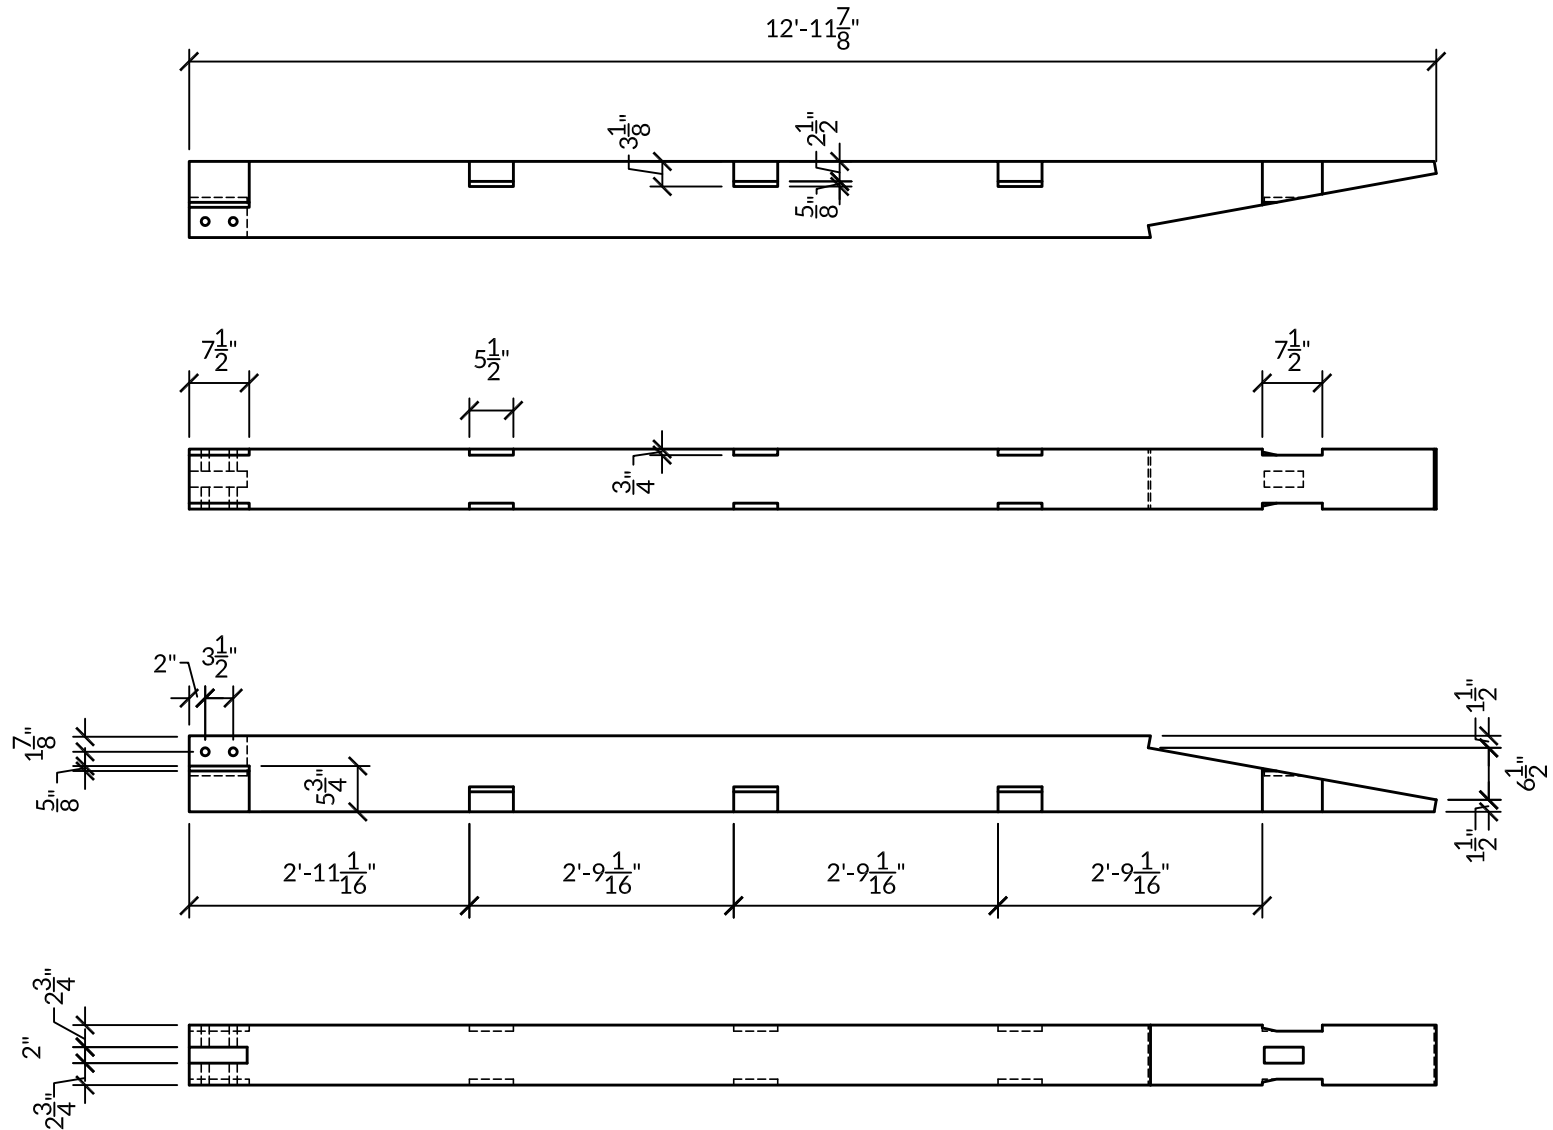
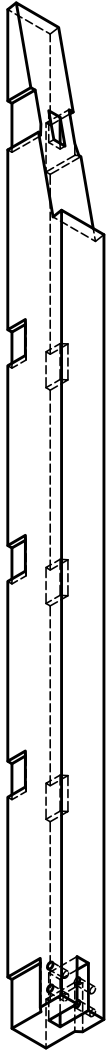


Ridge 1-2






Qty: 1

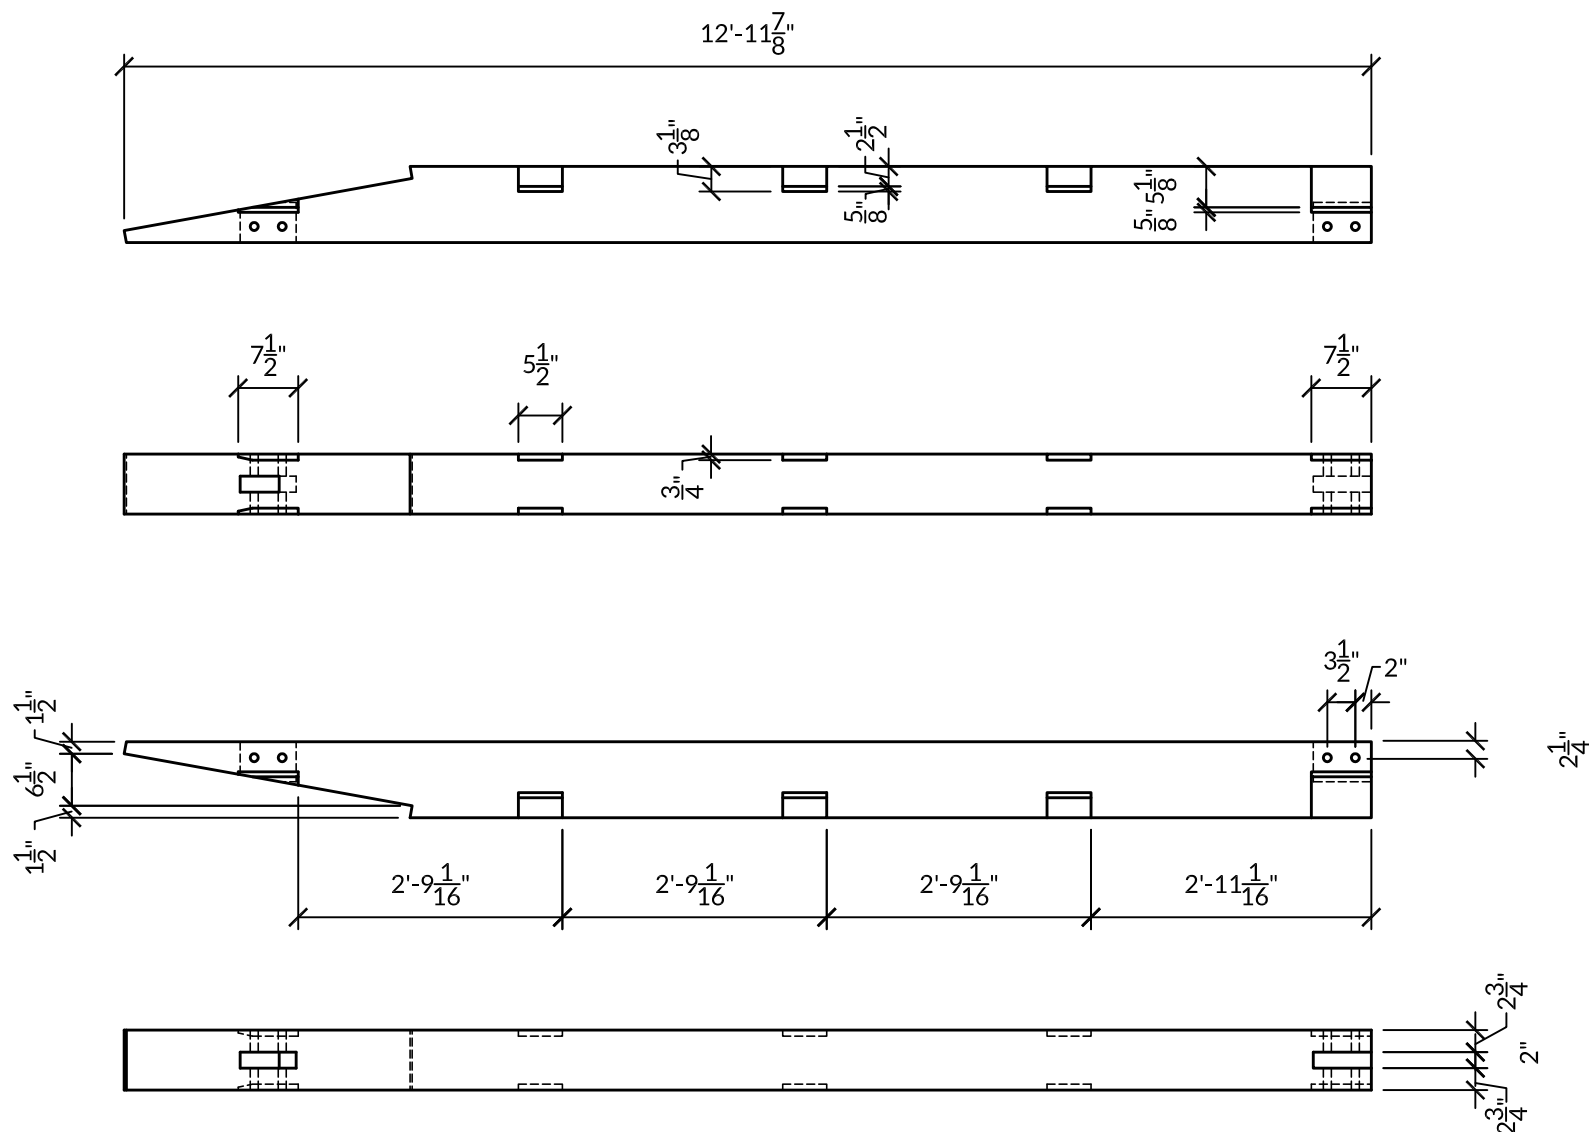



Qty: 1

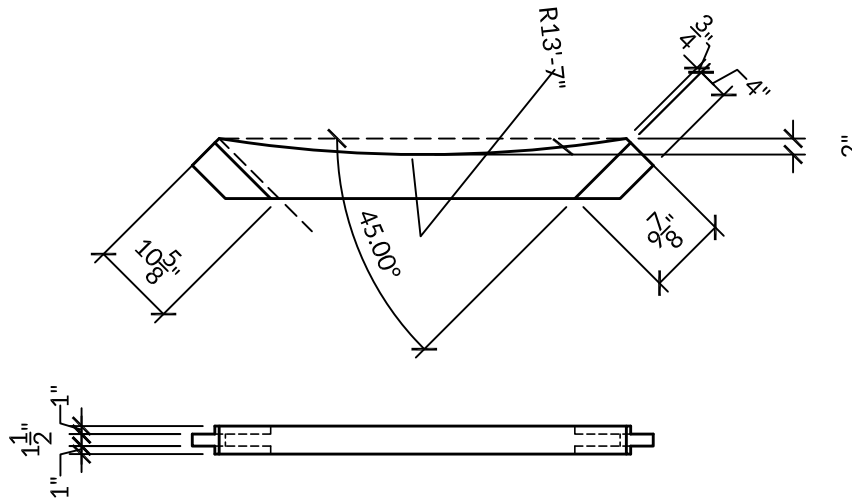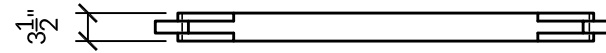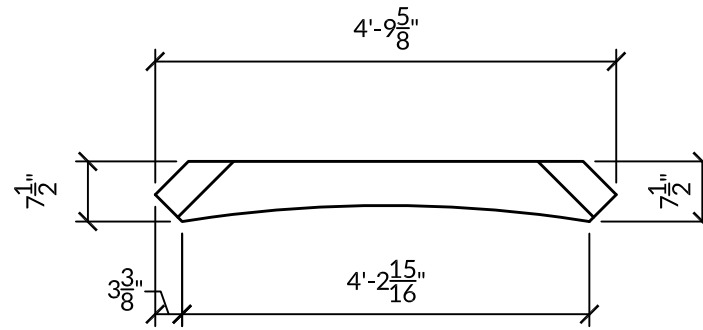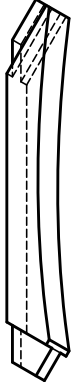


Knee Brace
Qty: 14

  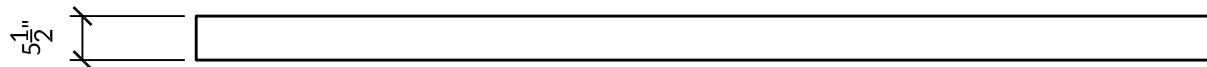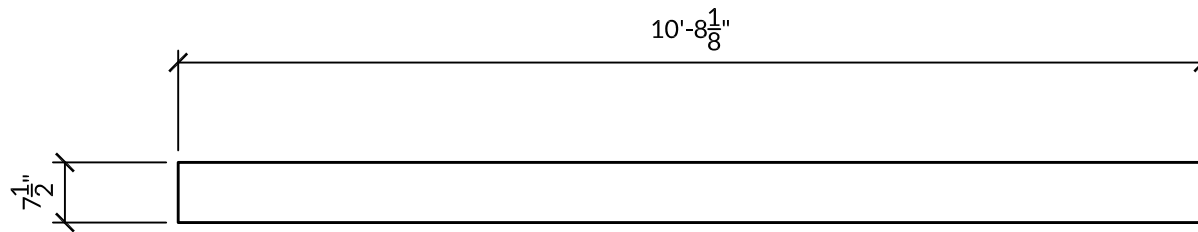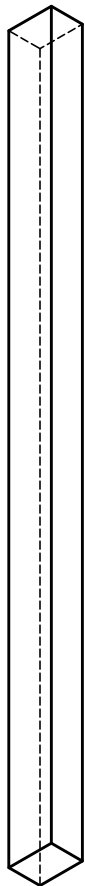


Joist
Qty: 7

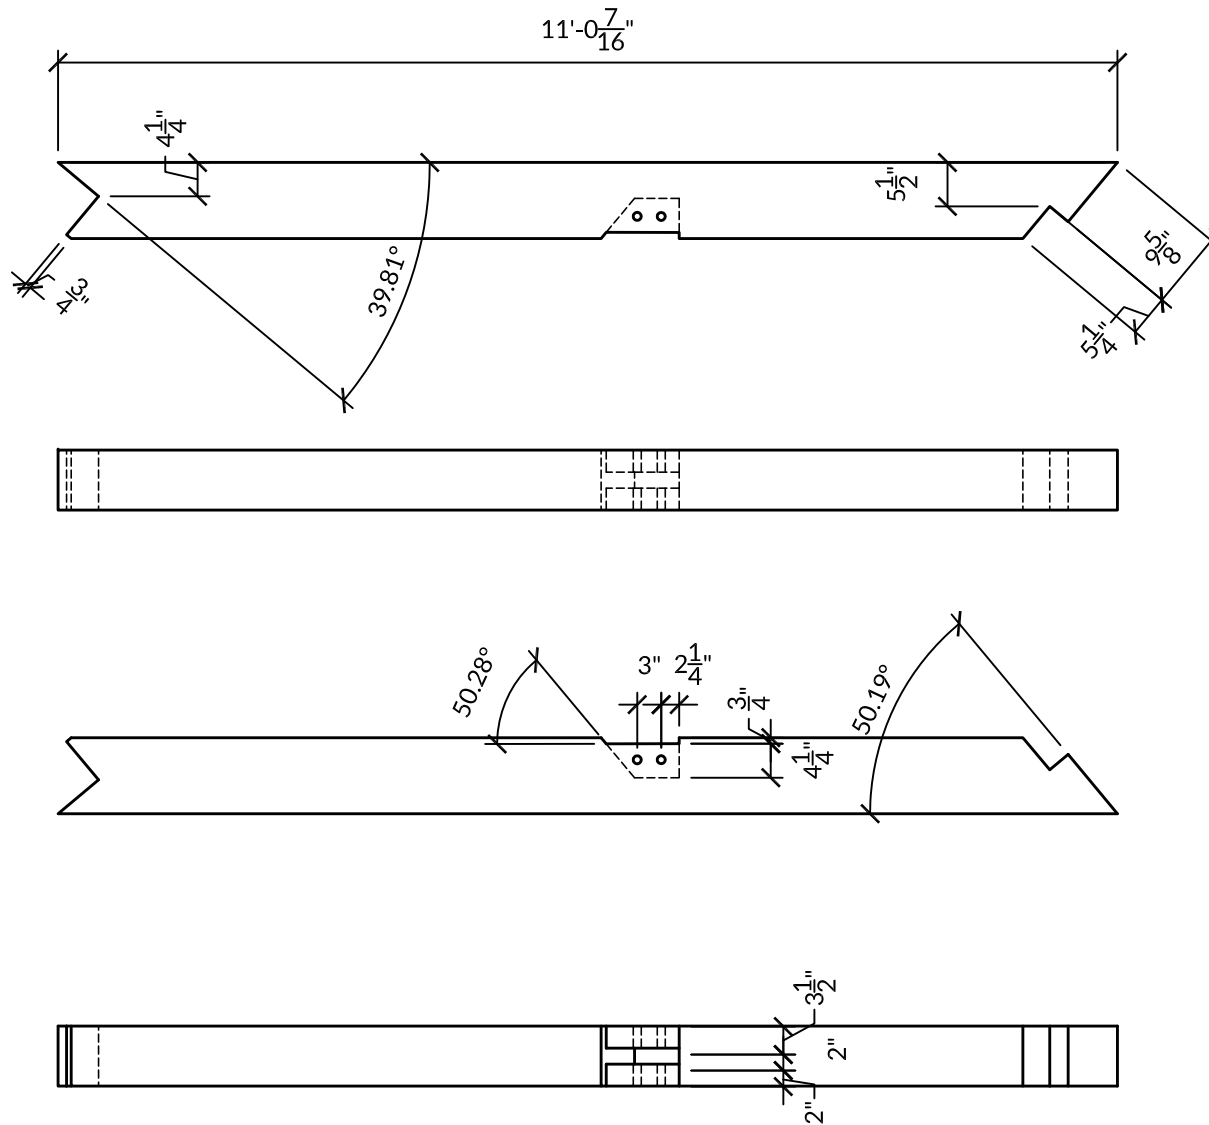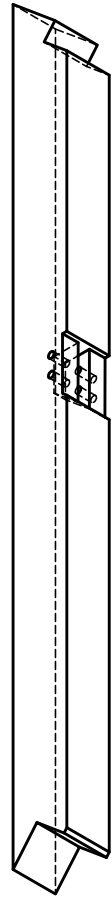


Principal Rafter
Qty: 6 - (3) Mirrored

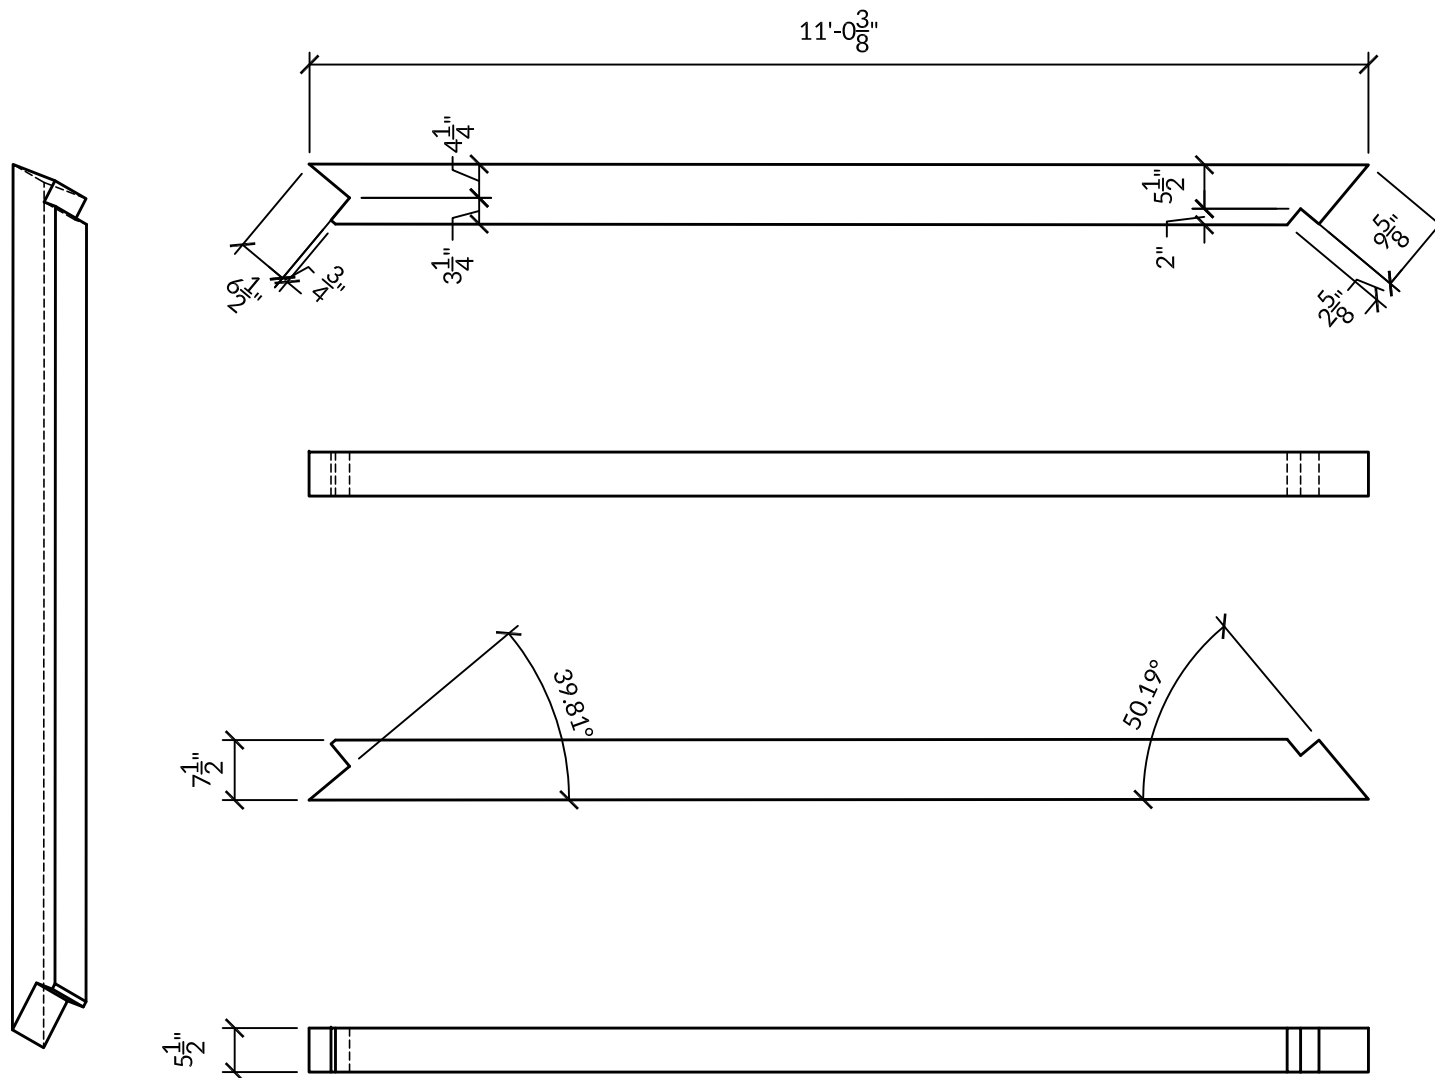

Common Rafter
Qty: 12

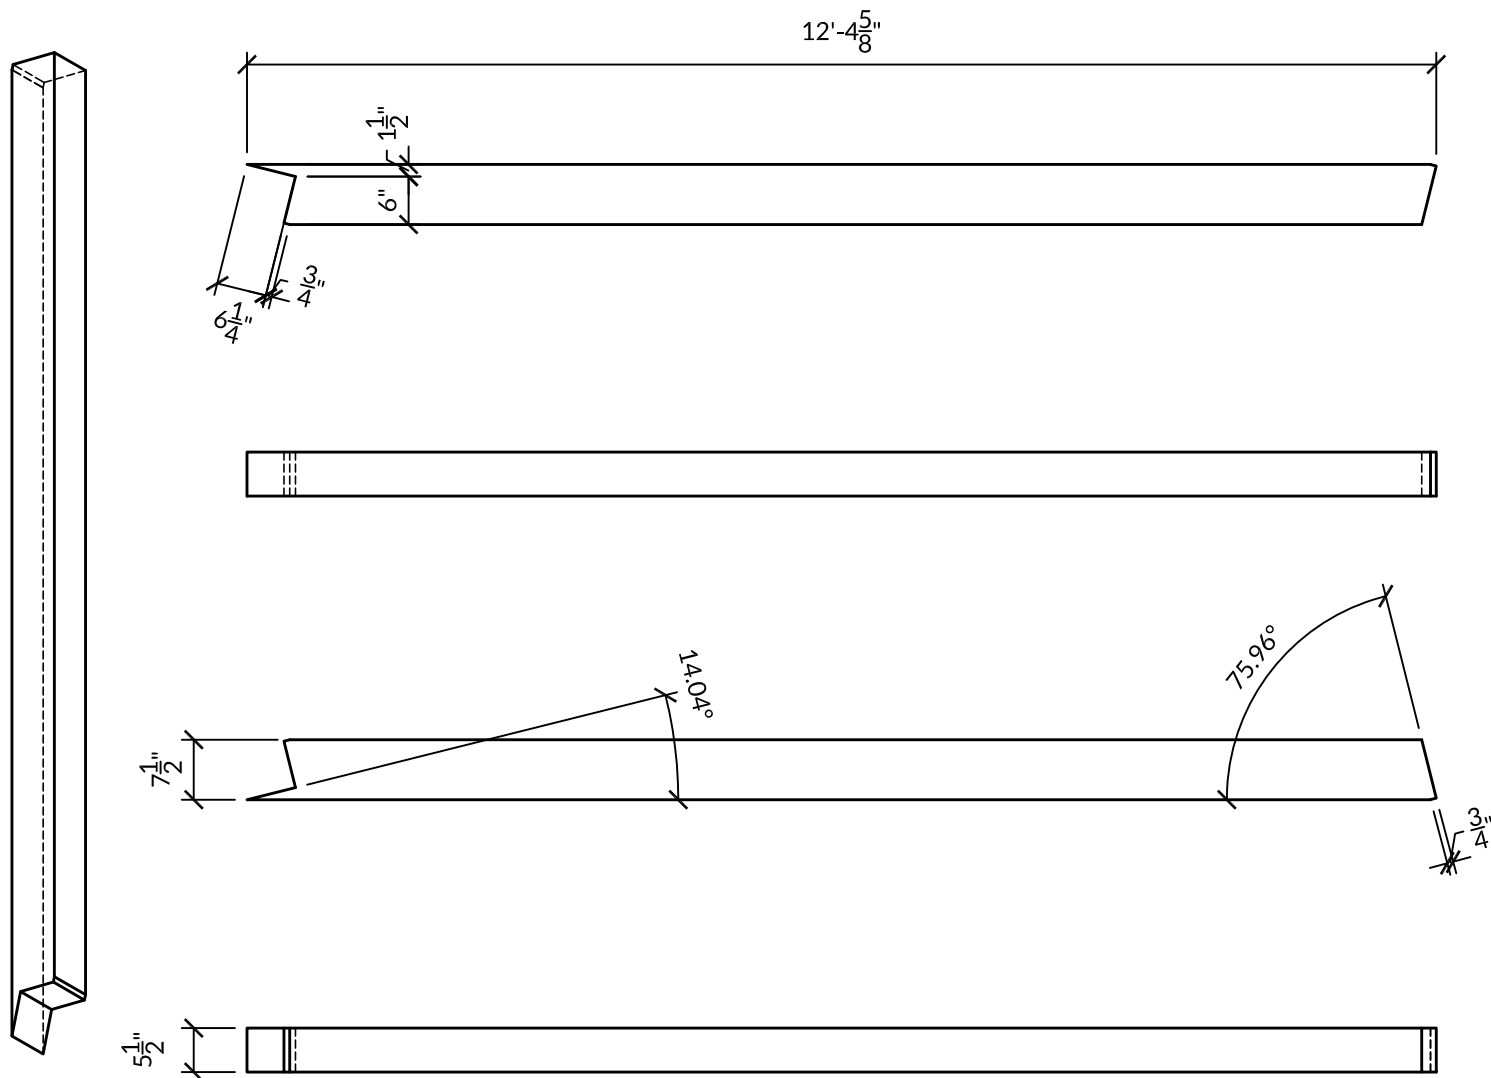

Shed Rafter
Qty: 8

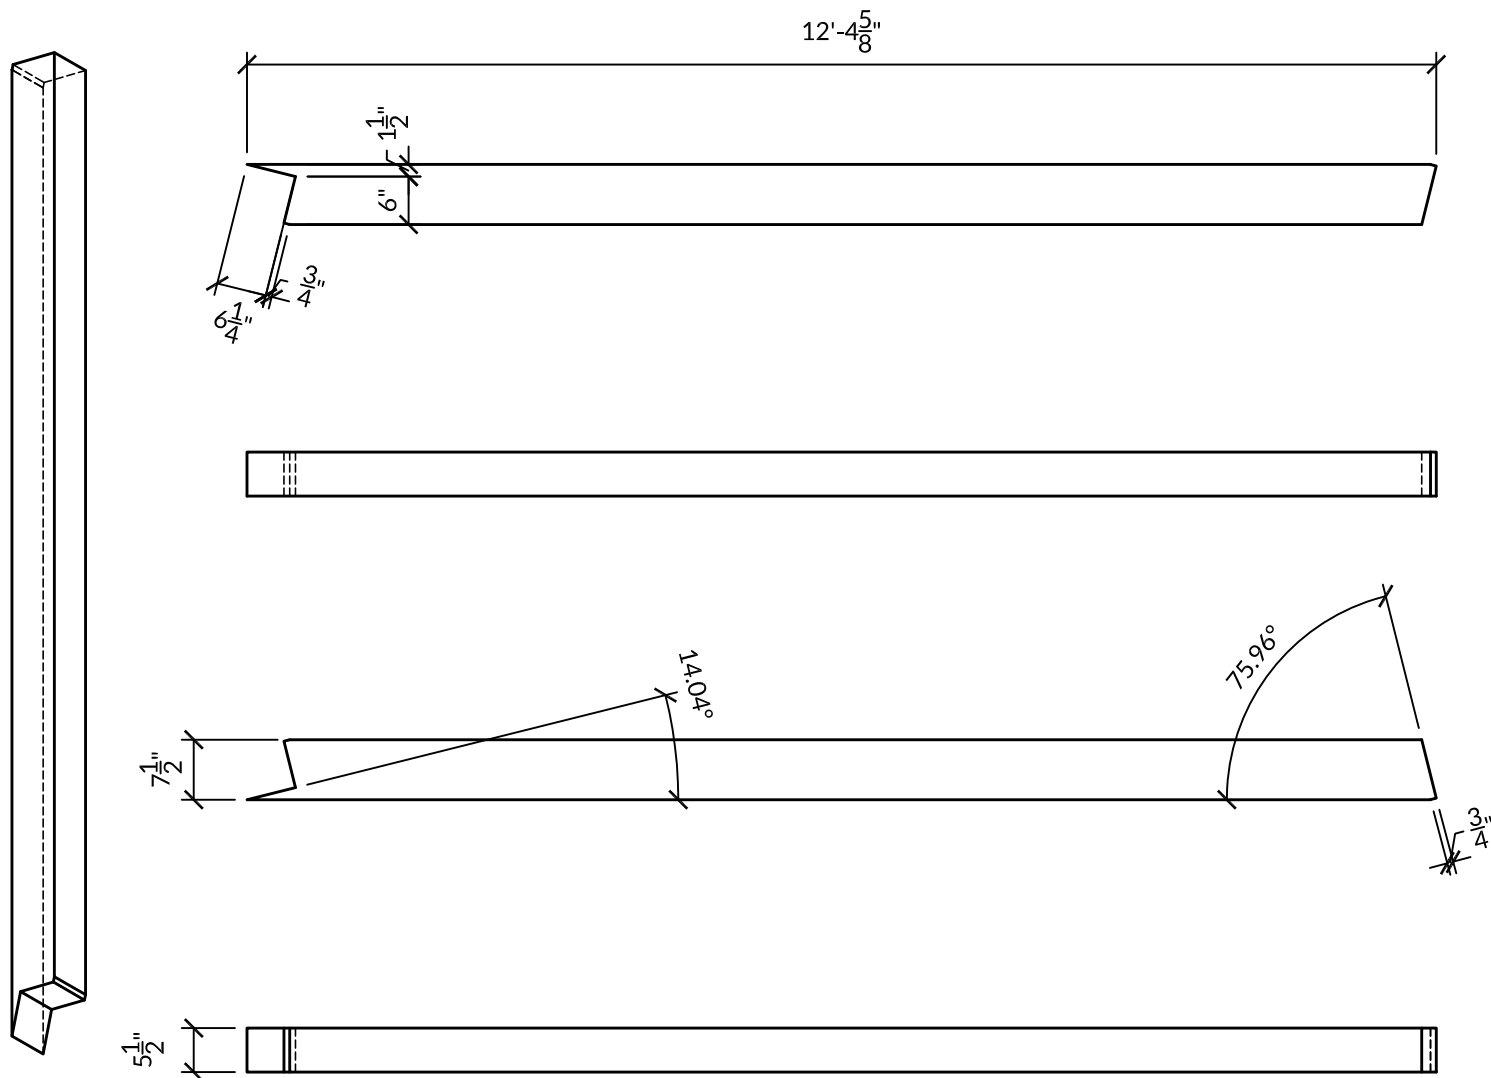

Shed Rafter
Qty: 8